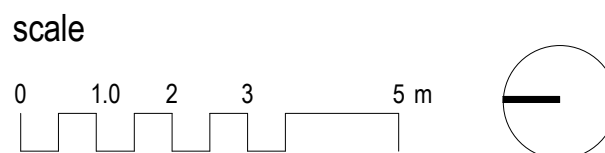


**CQU ROCKHAMPTON
TAFE
CONSOLIDATION -
STAGE 2**554/700 Yaamba Rd, Norman
Gardens QLD 4701

B	2026-03-05	ISSUED FOR TENDER	BC
A	2026-02-12	ISSUED FOR TENDER	BC
2	2026-01-30	60% DRAFT ISSUE	BC
1	2026-01-22	CONSULTANT ISSUE	BC

rev	date	details	init.
-----	------	---------	-------

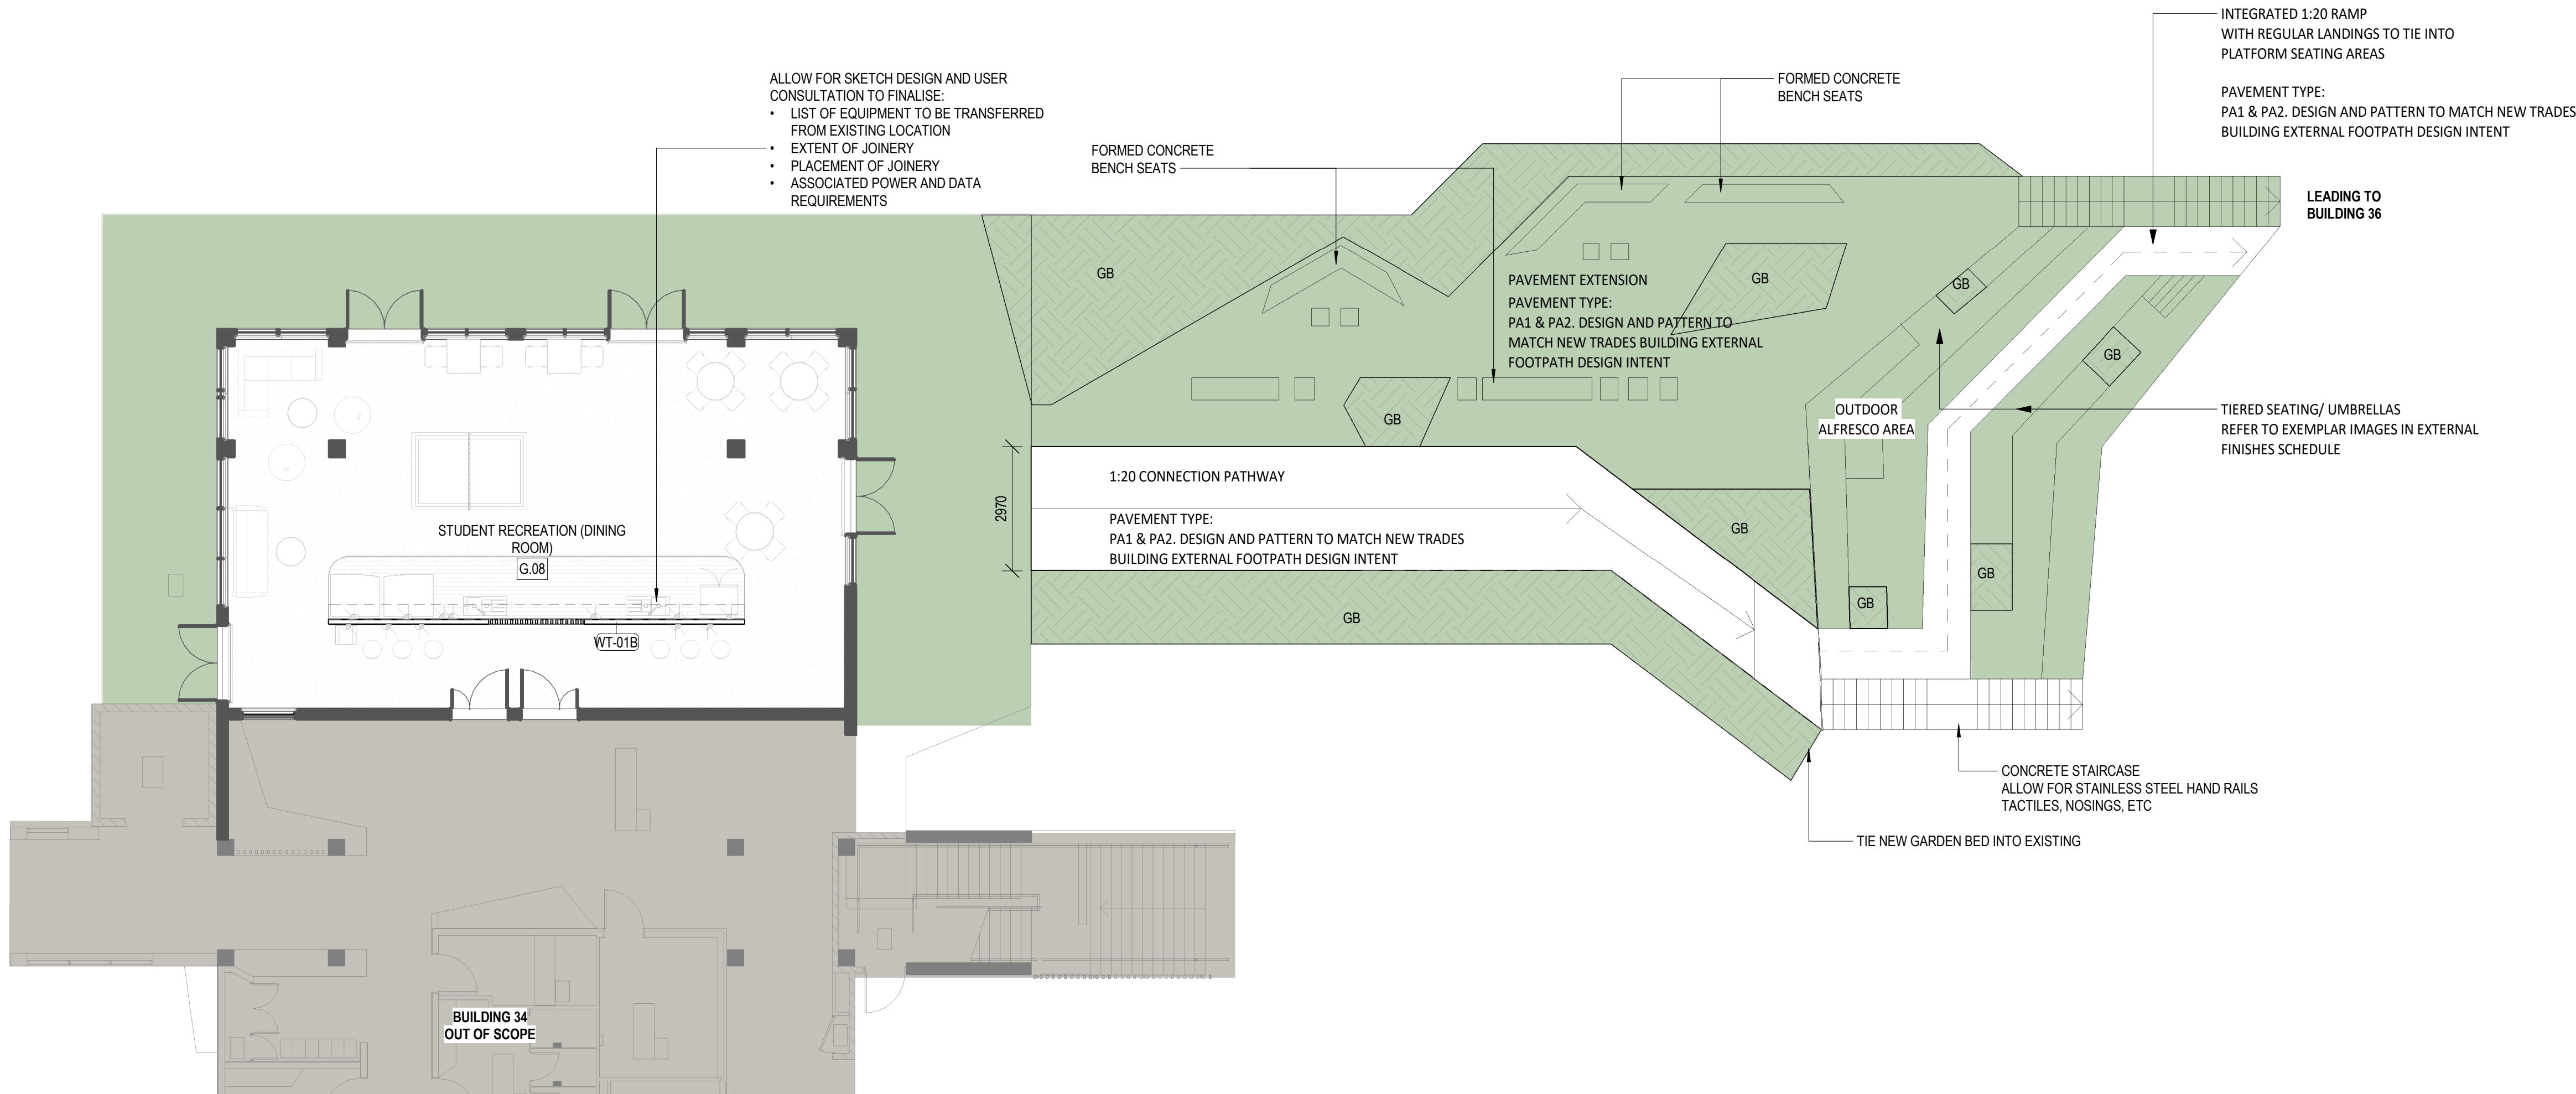
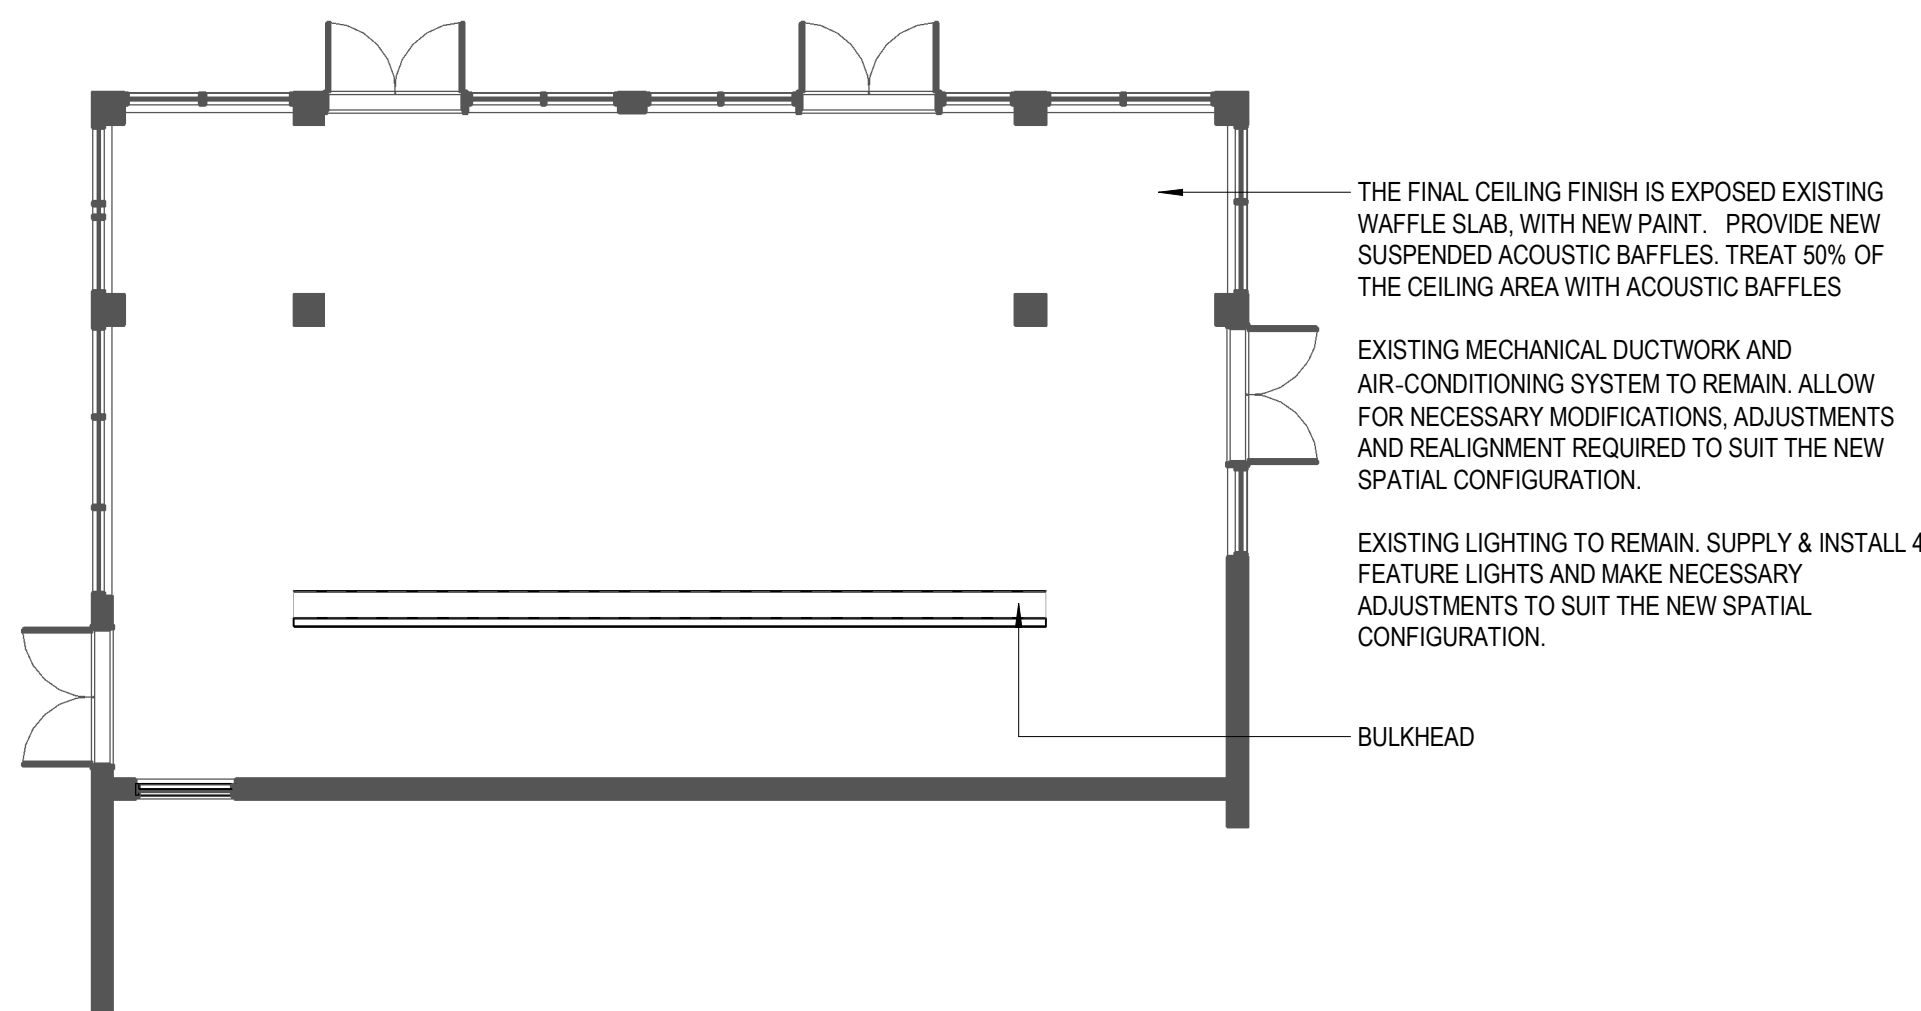
drawn	date
JT/JS	19/01/2026
checked	date
SS	12/02/2026
verified	date

**FLOOR & CEILING PLAN -
GROUND G.08 - PROPOSED**scale project no.
As indicated @ A1 25.0236.17revision
B

sheet no.

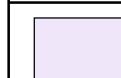
CQU-ROK-034-GN-ARC-21-01

original sheet size - A1 (594mm x 841mm)

**1**
31-00 **GROUND FLOOR - PROPOSED**
1 : 100**2**
31-00 **GROUND FLOOR - CEILING PLAN - GROUND FLOOR**
1 : 100**WALL LEGEND**

WT-01B_SF 92_PB 13 / PB WP 13	WT-01B
13mm PLASTERBOARD LINING, FLUSH SET	13mm STEEL STUD
13mm WATERPROOF PLASTERBOARD LINING, FLUSH SET	

SCOPE LEGEND

	INCLUDED SCOPE
	MASTER PLANNED SCOPE CONTRACTOR TO PROVIDE A 'BELOW THE LINE' COST FOR THESE WORKS SHOWN IN GREEN HATCH. THIS ADDITIONAL SCOPE MAY BE INCLUDED. THESE 'FUTURE' WORKS DO NOT FORM PART OF THE CORE SCOPE OF WORKS REQUIRED FOR THE STAGE 2 TAFE CONSOLIDATION.
	GB - GARDEN BED. CONTRACTOR TO ALLOW FOR LANDSCAPE DESIGN AND INSTALL BASED OFF LANDSCAPE ARCHITECT'S PLANTING PALETTE

CEILING LEGEND

2700	CEILING HEIGHT ABOVE FFL
CT1	CEILING FINISHES

CEILING LEGEND	
CT1-01	1200x600 CEILING TILES
CT1-02	1200x600 ACOUSTIC CEILING TILES
C/PB-S1	FLUSH SET PLASTERBOARD SHEETING
C/PB-S2	WATERPROOF PLASTERBOARD SHEETING
C/FC-01	FLUSH SET FIBRE CEMENT SHEETING

GENERAL NOTE

- INSTALL NEW WALL LINING. MAKE GOOD.
- CONTRACTOR TO CONFIRM EXISTING STRUCTURE & SERVICES ON SITE PRIOR BUILDING WORKS.
- REFER TO CQU DESIGN GUIDELINES FOR DESIGN AND CONSTRUCTION REQUIREMENTS.
- DRAWINGS TO BE READ IN CONJUNCTION WITH SERVICES, CIVIL AND STRUCTURAL DRAWINGS.
- REFER TO ROOM LAYOUT SHEET FOR EXTENT OF WORK INCLUDING GLAZED DOOR AND TO REFER FOR ALL FURNITURE SETOUT
- REFER TO OUTLINE SPECIFICATION & SCHEDULE FOR FF&E AND FINISHES
- DOOR NOTES
 - CQU TO CONFIRM ACCESS REQUIREMENT FOR STUDENT RECREATION SPACE
 - PROVIDE DOOR CLOSERS TO ALL DOORS ENCLOSING AIR-CONDITIONED SPACES
- CEILING NOTES
 - ALL REFLECTED CEILING PLANS ARE TO BE READ IN CONJUNCTION WITH SERVICE ENGINEERING DRAWINGS FOR MECHANICAL, FIRE, ELECTRICAL AND ALIKE.
 - SETOUT OF CEILING TILES TO BE CONFIRMED

INSULATION NOTE

- COMPLY WITH ACOUSTIC REPORT TO ACHIEVE THE NOMINATED ACOUSTIC RATING AND SECTION J REPORT FOR THE REQUIRED EXTERNAL WALLS R VALUES.
- COMPLY WITH THE CQU DESIGN GUIDELINES FOR MINIMUM ACOUSTIC SEPARATION BETWEEN ROOMS. WHERE THE ACOUSTIC REPORT NOMINATES HIGHER PERFORMANCE REQUIREMENTS, THE HIGHER RW RATINGS ARE TO APPLY.
- NEW STUD TO GO UP TO UNDERSIDE OF SLAB, UNLESS SPECIFIED.

ISSUED FOR TENDER