




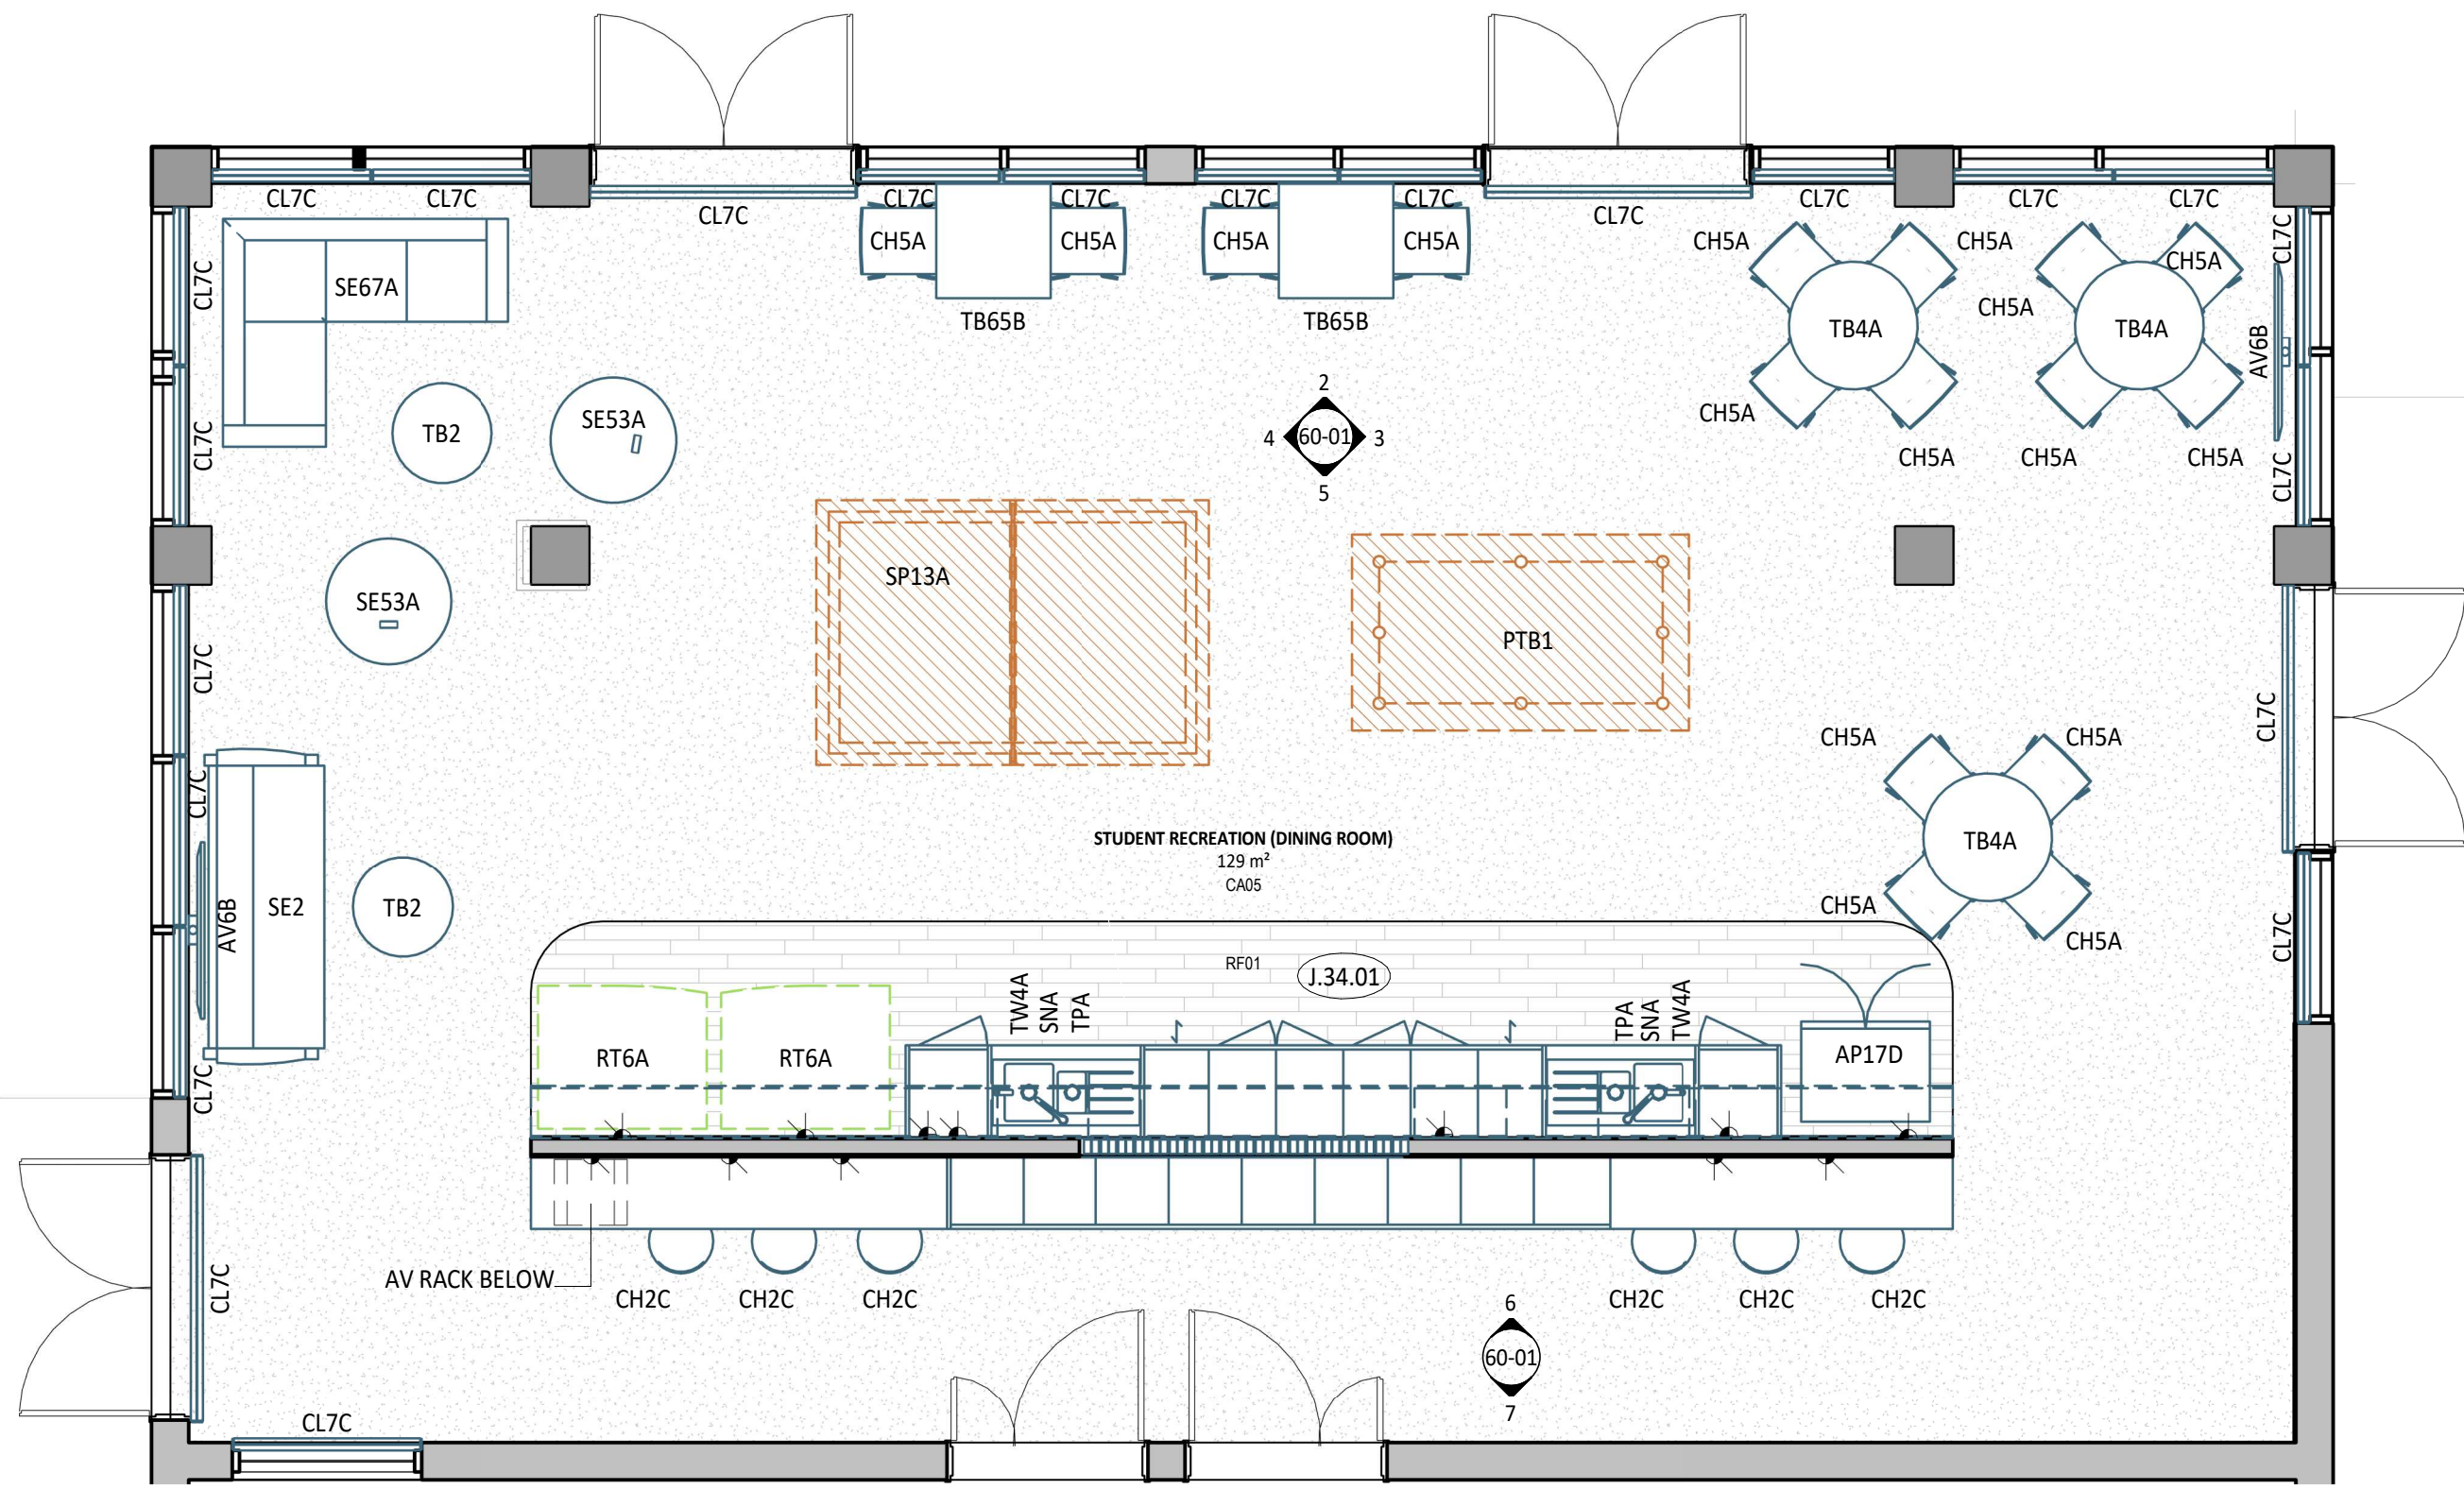


1 PLAN DETAIL
1 : 50

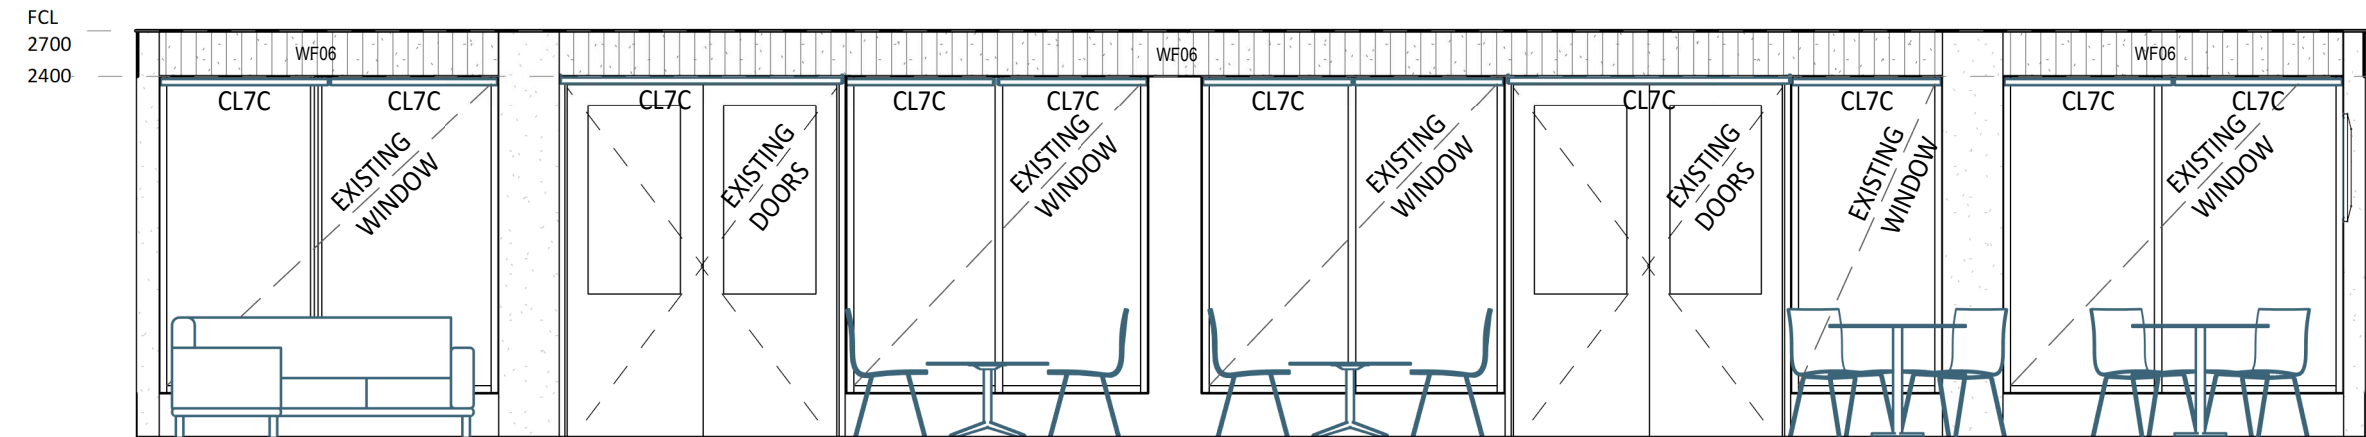

2 ELEVATION DETAIL
1 : 50

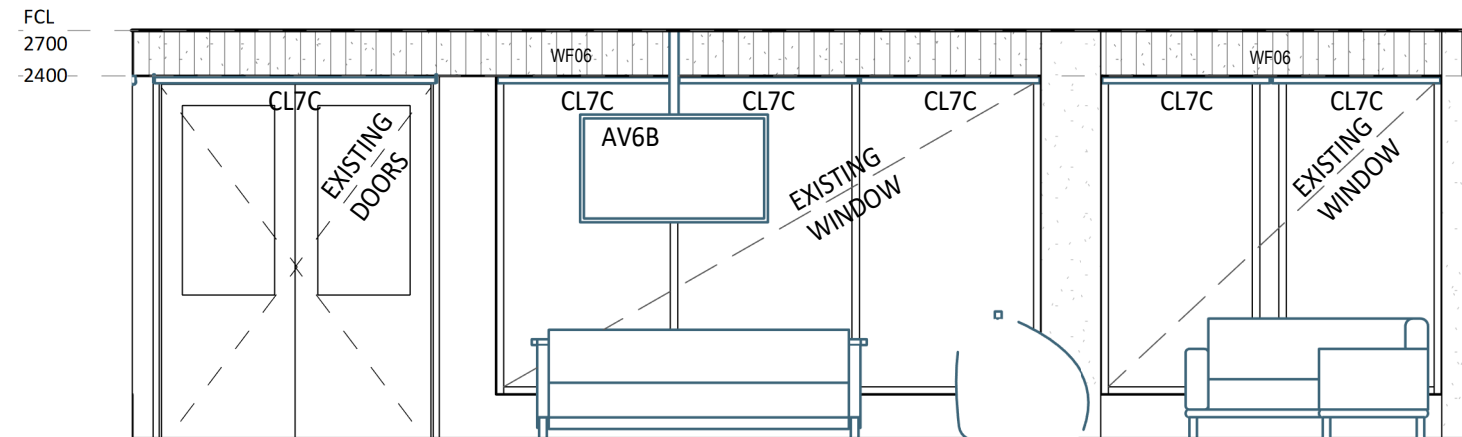

4 ELEVATION DETAIL
1 : 50

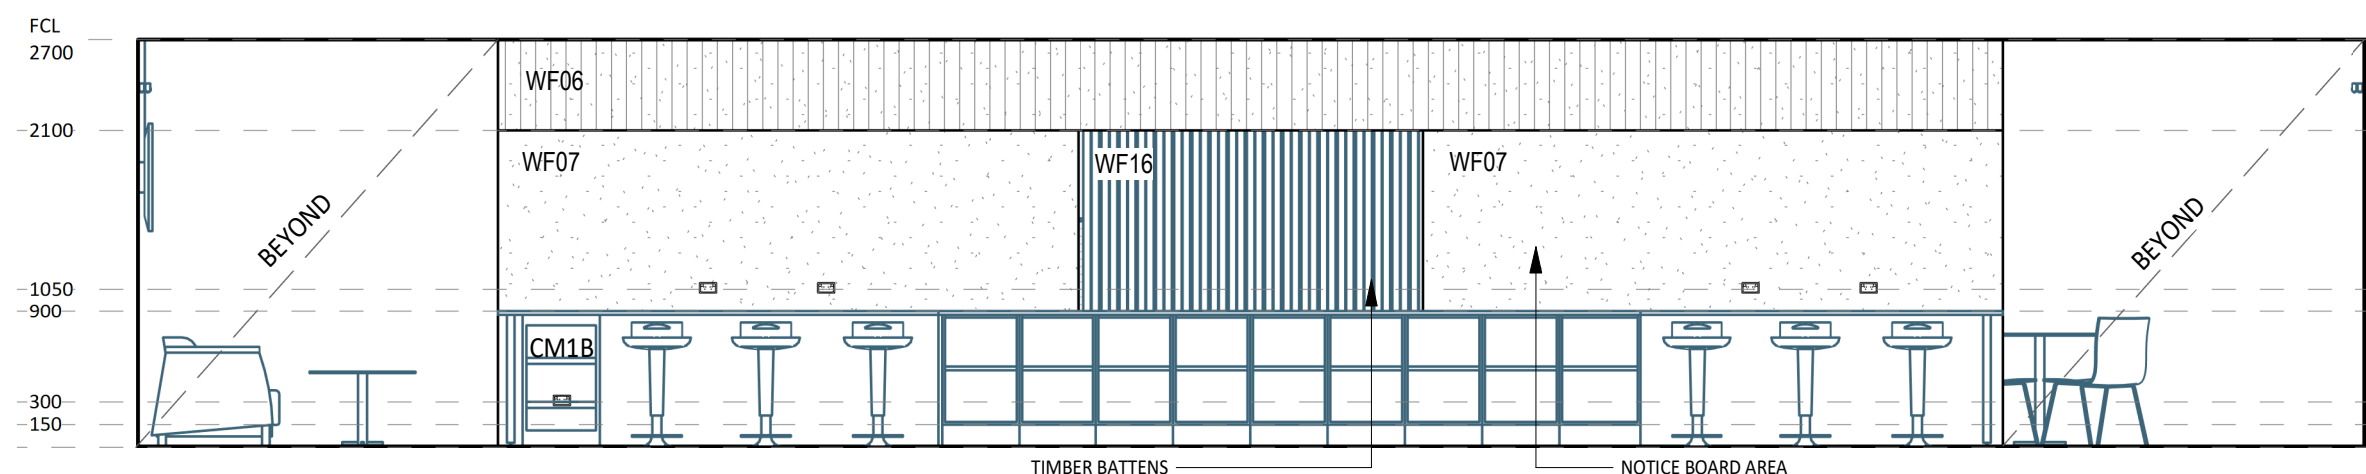

6 ELEVATION DETAIL
1 : 50

60-LEGEND JOINERY - BUILDING 34	
Joinery Code	Description
J.34.01	Benchtop, Underbench Cupboards, Knee Clearance Unit, Underbench Drawers, Underbench Bin Drawers, Overhead Shelvings, Bulkhead, Splashback
J.34.02	Benchtop, Underbench Cupboards, Full Height Shelving, Acoustic Pin Board Splashback

40-LEGEND FFE - STUDENT RECREATION (DININ...			
Z	Description	Group	Count
AP17D	Refrigerator - Freezer Below	1	1
AV6B	Ceiling Mounted Screen with Speakers	1	2
CH2C	Chair - Breakout	1	6
CH5A	Chair - Breakout	1	16
CL7C	Double Roller Blinds - Blockout	1	22
CM1B	AV Rack	1	1
SE2	Lounge - Three Seater Sofa	1	1
SE53A	Bean bag	1	2
SE67A	Lounge - L Shaped With Siderests	1	1
SNA	Sink - Accessible	1	2
TB2	Table - 700DIA x 500H - Round Coffee	1	2
TB4A	Table - 900DIA x 720H - Round Dining	1	3
TB65B	Table - Dining X Base - 800W x 800D x 720H	1	2
TPA	Mixer - Sink Accessible	1	2
TW4A	Tapware - Hot and Cold Water Boiling Unit	1	2
PTB1	Pool Table	2T	1
SP13A	Table - Table Tennis	2T	1
RT6A	Vending Machine - Snacks	3	2


FF&E LEGEND	
GROUP 1 ITEMS (PROVIDED & FITTED UNDER CONTRACT)	
GROUP 2 ITEMS (PROVIDED BY CLIENT & FITTED UNDER CONTRACT)	
GROUP 2T ITEMS - EXISTING EQUIPMENT (PROVIDED BY CLIENT & FITTED UNDER CONTRACT)	
GROUP 3 ITEMS (PROVIDED & INSTALLED BY CLIENT)	
PLANS TO BE PRINTED IN COLOUR	
SCH_Code	FF&E TAG
JO.PROC	JOINERY TAG

ELECTRICAL LEGEND	
SINGLE POWER OUTLET	LIGHT SWITCH
DOUBLE POWER OUTLET	TV
SINGLE DATA	
DOUBLE DATA	
REFER TO ELECTRICAL ENGINEER'S DRAWINGS FOR DETAILS	


- NOTE:**
- LOCATION OF EXISTING CROWD DJ AND SPEAKERS TO BE CONFIRMED
 - ALLOW FOR SKETCH DESIGN AND USER CONSULTATION TO FINALISE:
 - LIST OF EQUIPMENT TO BE TRANSFERRED FROM EXISTING LOCATION
 - EXTENT OF JOINERY
 - PLACEMENT OF JOINERY & FFE
 - ASSOCIATED POWER AND DATA REQUIREMENTS

- RLS NOTES**
- ALL ARCHITECTURAL DRAWINGS TO BE READ IN CONJUNCTION WITH OTHER DISCIPLINES.
 - REFER TO FF&E, SANITARYWARE SCHEDULES FOR ALL FURNITURE, FIXTURES, AND EQUIPMENT.
 - REFER TO HYDRAULIC ENGINEER'S DRAWINGS FOR HYDRAULIC SERVICES. FINISH OF VALVE/BOX COVERS TO MATCH ADJACENT WALL/JOINERY FINISH.
 - REFER TO ELECTRICAL DOCUMENTATION FOR OUTLET DETAILS (ie. POWER, DATA, COMMS etc.)
 - REFER TO AUDIO VISUAL DOCUMENTATION (VideoPro) FOR AV REQUIREMENTS AND DETAILS.
 - AV SUPPLIER TO CONFIRM EXACT POSITIONS OF EQUIPMENT ON SITE.
 - ALL FF&E ITEMS ARE TO BE READ IN CONJUNCTION WITH FF&E SCHEDULES AND CQU DESIGN MANUAL.
 - ALL FF&E AND TRANSFER ITEMS TO BE REVIEWED AND CONFIRMED WITH CLIENT PRIOR TO COMMENCING ON SITE.
 - PROVIDE ALLOWANCE AND ADD SUPPORT TO WALLS, WHERE FITTINGS ARE WALL MOUNTED. THIS INCLUDES BUT NOT LIMITED TO HANDBASINS, HANDRAILS, SCREENS, PROJECTORS, etc.
 - FF&E COUNT IS FOR INFORMATION ONLY. THE TOTAL NUMBER OF FF&E ITEMS ARE TO BE CONFIRMED WITH CLIENT AND ARCHITECTS BEFORE PURCHASE OF ITEMS.
 - CONFIRM ALL DIMENSIONS ON SITE FOR JOINERY ITEMS.
 - ALL SANITARY FIXINGS & FIXTURES IN PWD TOILETS TO BE INSTALLED IN ACCORDANCE WITH AS1428.1
 - ALLOW FOR FIRE EXTINGUISHERS & FIRE BLANKETS AS PER AS2444.2001
 - POWER AND DATA POINTS SHOWN ON THE ROOM LAYOUT SHEETS WERE SHOWN AND DISCUSSED DURING USER GROUP BRIEFING. THESE RELATE TO PARTICULAR EQUIPMENT THAT WAS DISCUSSED AS REQUIRING POWER AND DATA. THESE REFLECT STAKEHOLDER EXPECTATIONS FOR SPECIFIC POWER AND DATA POINTS AND HAVE REMAINED IN THE DOCUMENTATION AS A USEFUL REFERENCE FOR THE CONTRACTOR. THESE ARE NOT A COMPLETE QUANTITY AND SPECIFICATION OF POWER AND DATA. THE CONTRACTOR IS TO REFER TO ELECTRICAL ENGINEER'S DOCUMENTATION FOR ALLOWANCE. REFER TO ELECTRICAL DOCUMENTATION FOR AMPS AND 3 PHASE POWER REQUIREMENTS. REFER TO AUDIO VISUAL (VIDEOPRO) DOCUMENTATION FOR ADDITIONAL POWER AND DATA REQUIREMENTS
 - ALLOW FOR STRUCTURAL PLY BACKING BEHIND PLASTERBOARD FOR FULL EXTENT OF WALLS WITH MOUNTED AUDIO VISUAL EQUIPMENT. REFER TO AUDIO VISUAL (VIDEOPRO) DOCUMENTATION FOR LOCATIONS OF WALL MOUNTED EQUIPMENT.
 - ALLOW FOR PRIVACY FILM TO ALL INTERNAL GLAZING (DOORS AND WINDOWS) TO OFFICES AND MEETING ROOMS. CONFIRM SET OUT PRIOR TO INSTALLATION
 - ALLOW FOR DOUBLE BLOCK OUT BLINDS TO ALL WINDOWS UNLESS NOTED OTHERWISE
 - ALL INTERNAL DOORS ARE TO BE SOLID CORE DOORS WITHIN ALUMINIUM FRAMED SUITES UNLESS NOTED OTHERWISE.
 - FLOOR BOXES MUST BE COORDINATED WITH BOTH THE STRUCTURAL AND ELECTRICAL ENGINEERS. BEFORE ANY CUTTING OF THE EXISTING SLAB OCCURS, CONFIRM THE EXACT LOCATIONS AND REQUIREMENTS WITH THE STRUCTURAL ENGINEER.
 - HEARING AUGMENTATION TO AUSTRALIAN STANDARDS - REFER VIDEOPRO AND ELECTRICAL SPECIFICATION

3 ELEVATION DETAIL
1 : 50

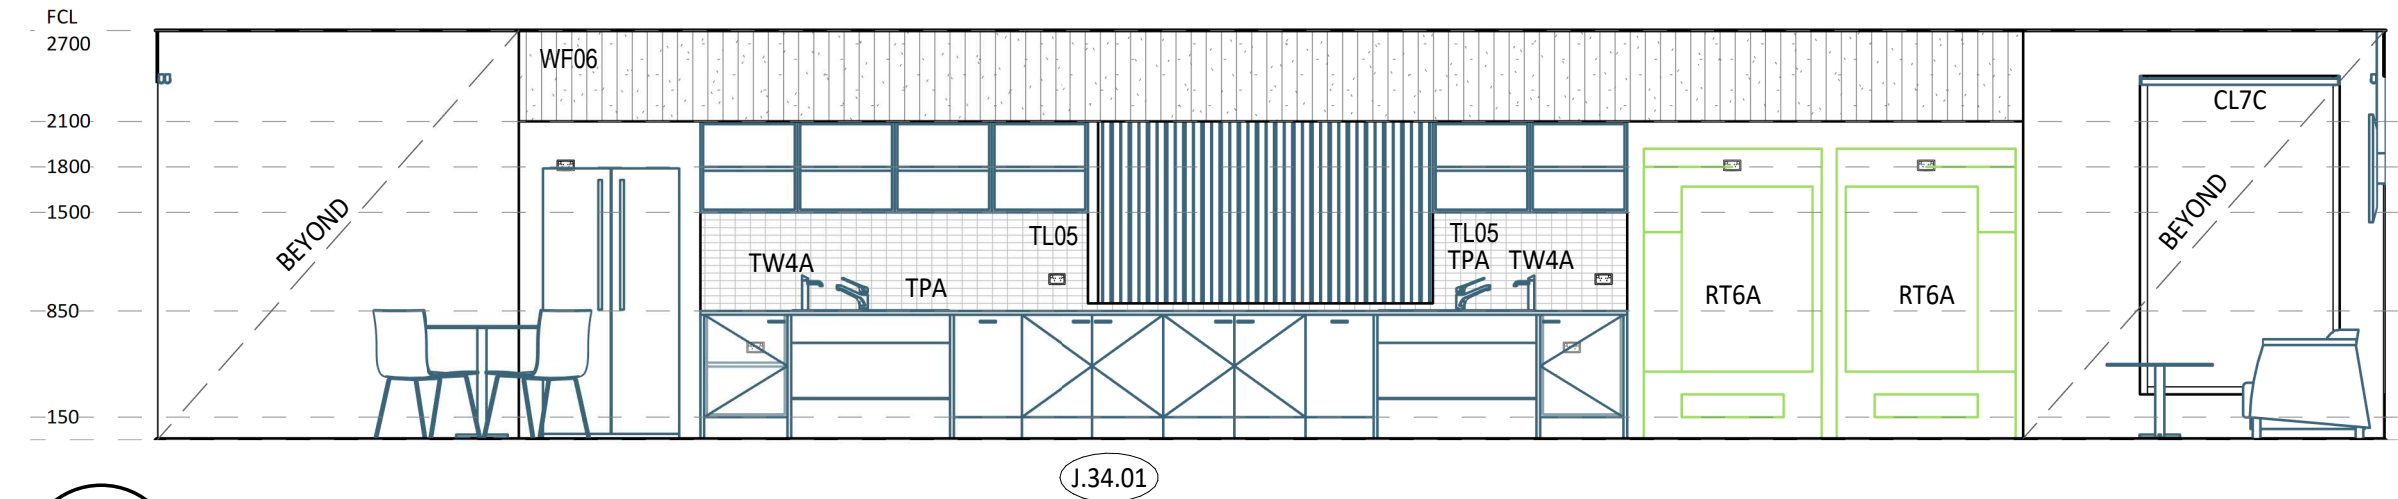

5 ELEVATION DETAIL
1 : 50

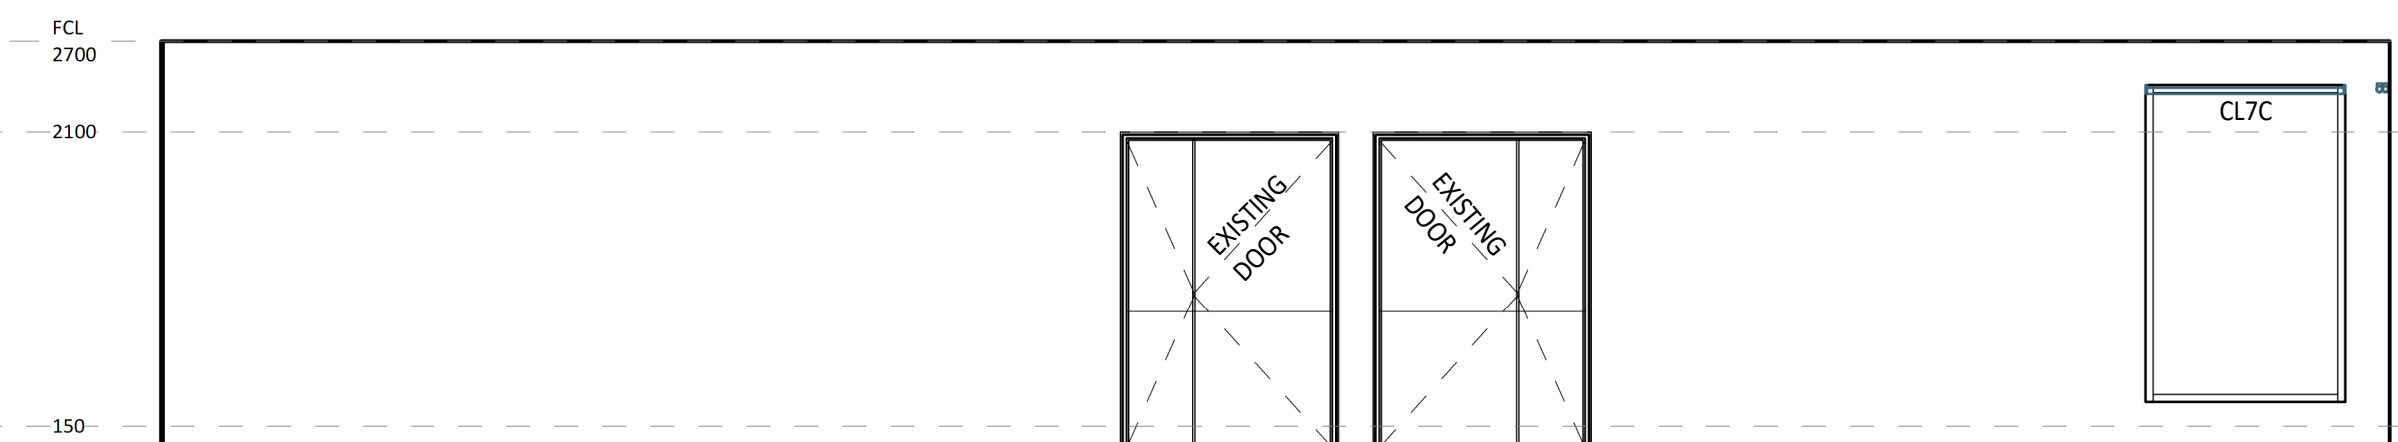

7 ELEVATION DETAIL
1 : 50