


INFORMATION REFLECTED ON THIS DRAWING REPRESENTS ELECTRICAL SERVICES DESIGN DEVELOPED FOR D&C TENDER ADVICE ONLY, AND SHOULD NOT BE REGARDED AS COMPLETE. THE D&C CONTRACTOR SHOULD REFER TO ALL ASSOCIATED ARCHITECTURAL AND OTHER DISCIPLINE DRAWINGS, PROJECT BRIEFS AND CLIENT REQUIREMENTS AND MAKE ADEQUATE ALLOWANCES FOR ALL NECESSARY ELECTRICAL SERVICES WORKS TO MEET THESE REQUIREMENTS, EQUIPMENT SCHEDULES AND COMPLIANCE WITH THE NCC & APPROPRIATE AUSTRALIAN STANDARDS

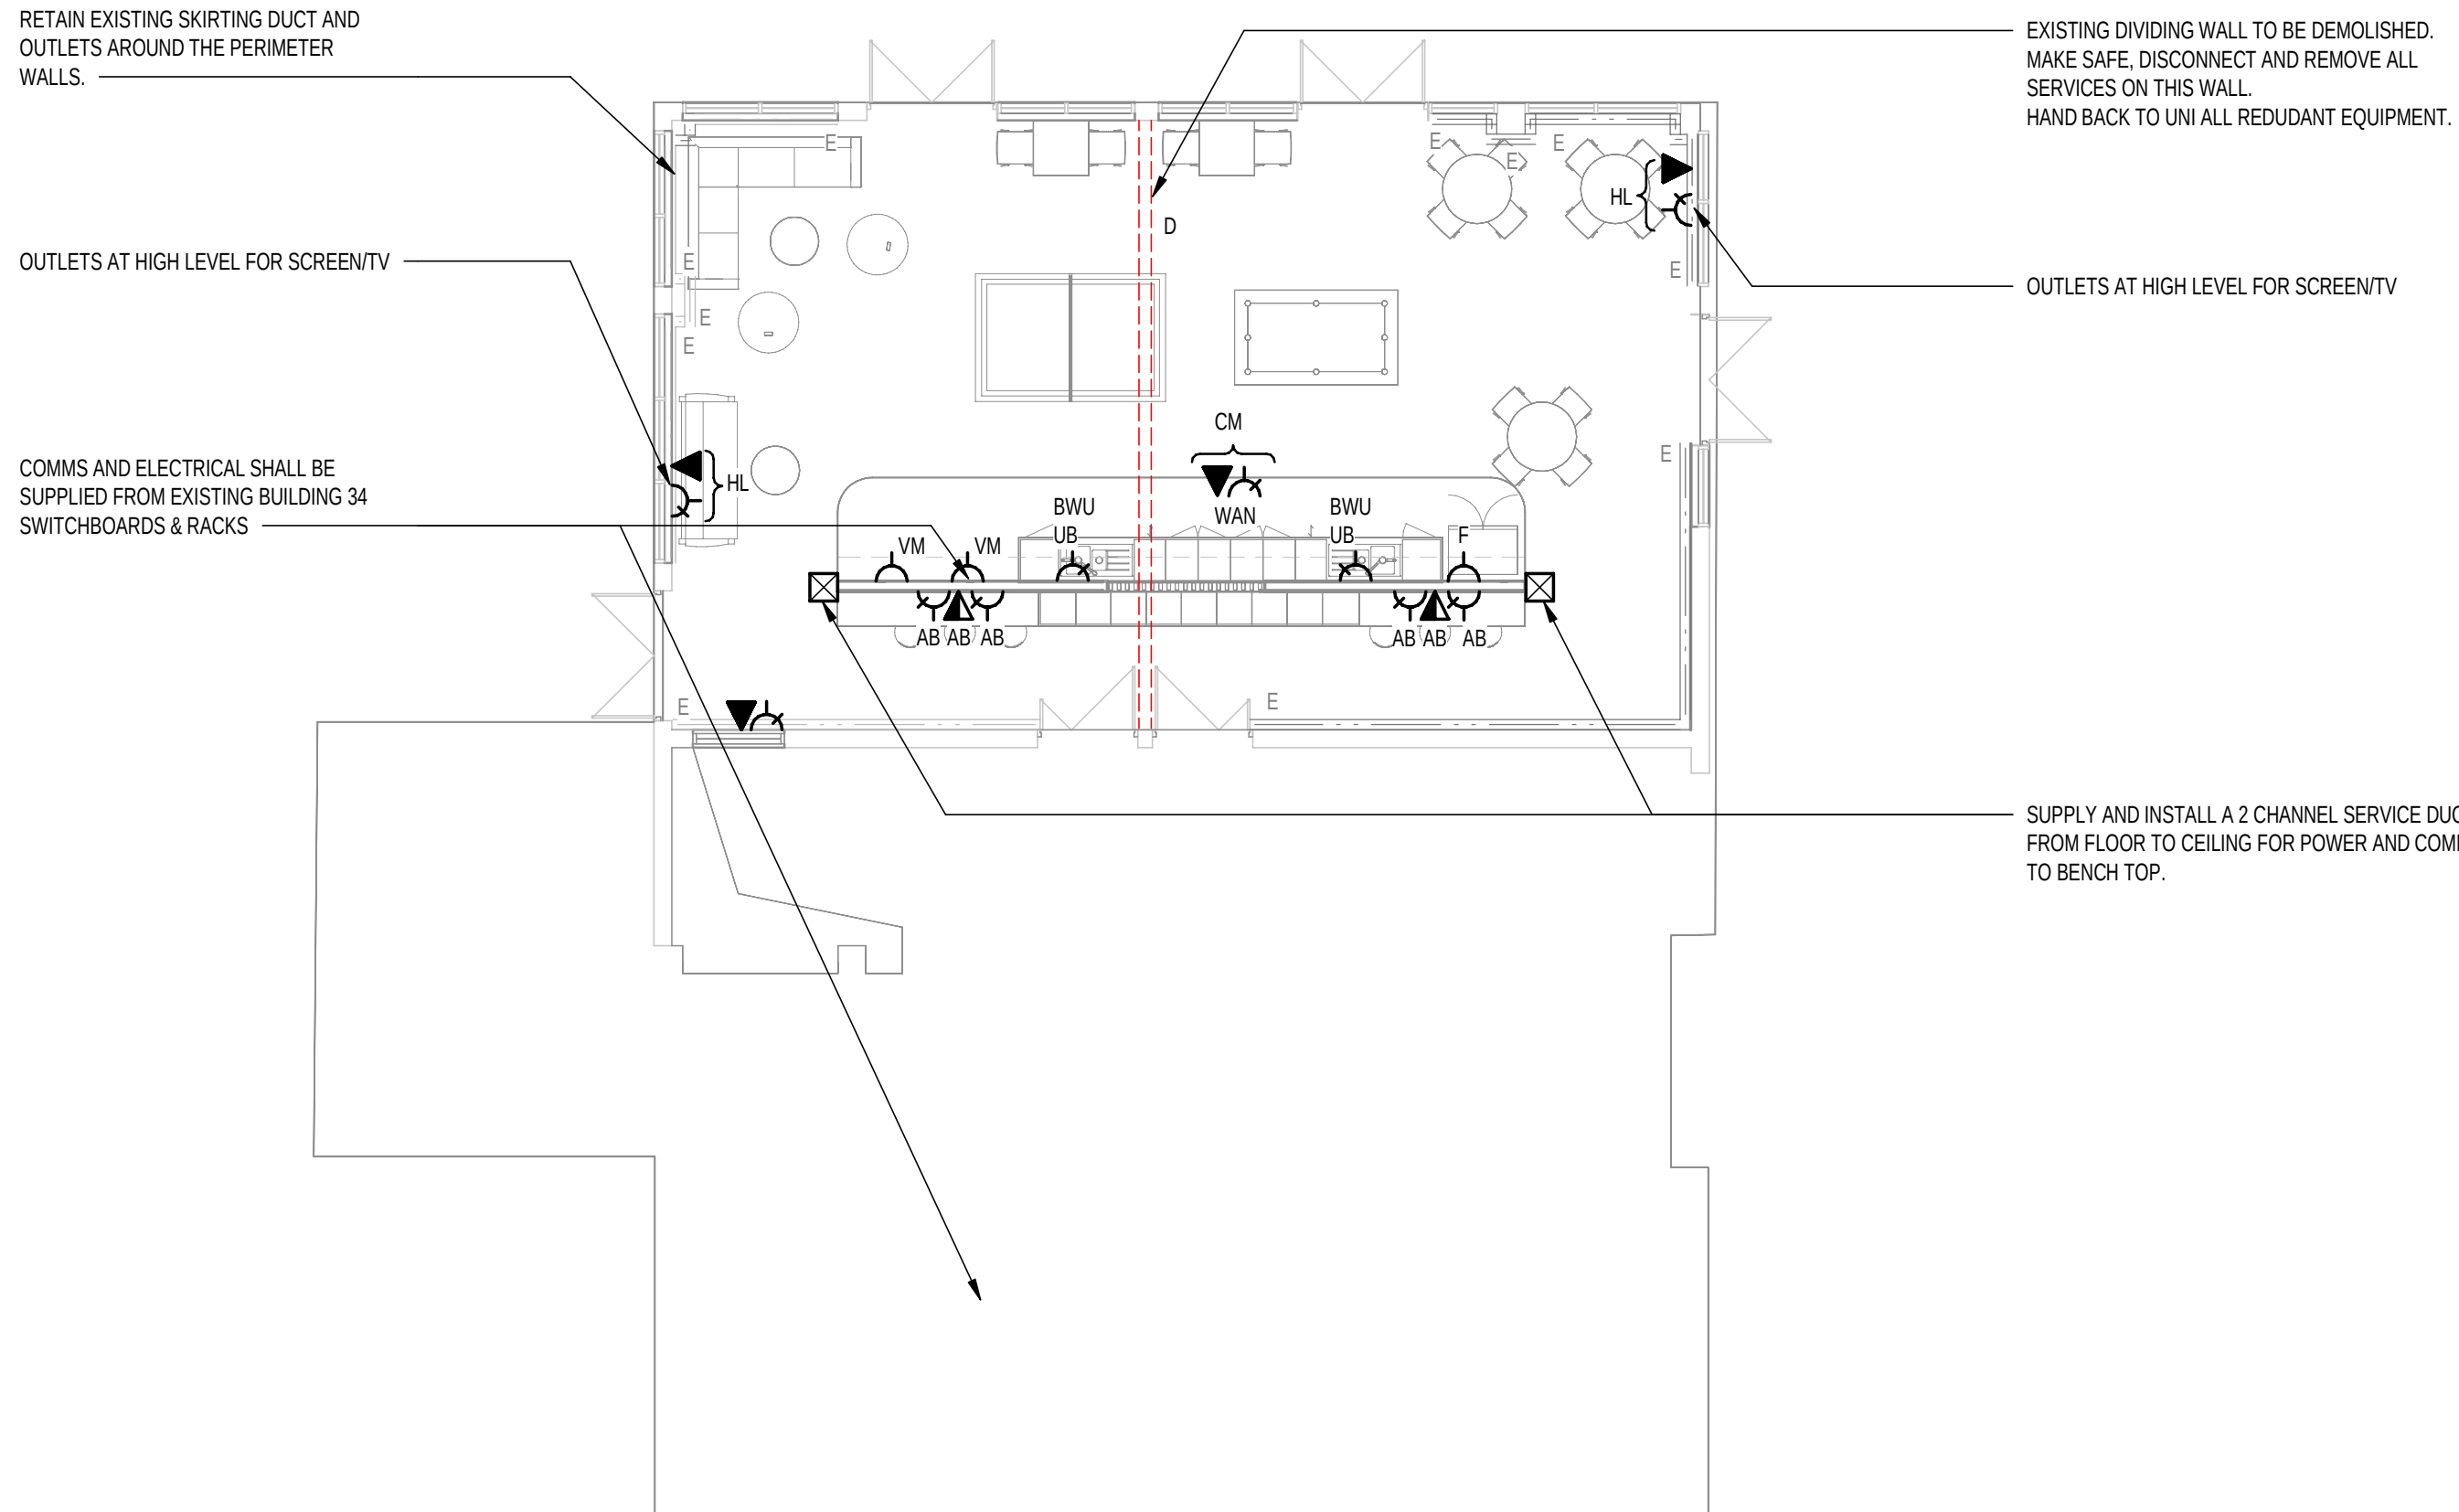

B	12.02.2026	MM	ISSUED FOR D&C TENDER	TP	SM
A	30.01.2026	MM	DRAFT 60% DD ISSUE FOR REVIEW	TP	SM
REV	DATE	BY	DESCRIPTION	CHK	APP

DOMESTIC STATUS:

DESIGN DEVELOPMENT

DESIGN DEVELOPMENT

DESIGN DEVELOPMENT



100 Ann Street, Level 12, Fortitude Valley 4
Tel: +61-7-3854-6200 Fax: +61-7-3854-65
<http://www.wsp.com>

CLIENT: COL

ARCHITECT: THOMSON ADSETT / PEDDLE THORP

PROJECT: CQU ROCKHAMPTON TAFE CONSOLIDATION

TITLE: ELECTRICAL SERVICES
BUILDING 34 - GROUND LEVEL - POWER AND
COMMS LAYOUT

SCALE @ A0: 1:100	CHECKED: TP	APPROVED: SM
PROJECT NUMBER: PS229518	DRAWN: MM	DATE: JAN 2026

DRAWING No:	REV:
B34-EL-DR-520-L00-34-00-00	

© WSP Australia Pty Ltd