


INFORMATION REFLECTED ON THIS DRAWING REPRESENTS MECHANICAL SERVICES DESIGN DEVELOPED FOR D&C TENDER ADVISE ONLY, AND SHOULD NOT BE REGARDED AS COMPLETE. THE D&C CONTRACTOR SHOULD REFER TO ALL ASSOCIATED ARCHITECTURAL AND OTHER DISCIPLINE DRAWINGS, PROJECT BRIEFS AND CLIENT REQUIREMENTS AND MAKE ADEQUATE ALLOWANCES FOR ALL NECESSARY MECHANICAL SERVICES WORKS TO MEET THESE REQUIREMENTS, EQUIPMENT SCHEDULES AND COMPLIANCE WITH THE NCC & APPROPRIATE AUSTRALIAN STANDARDS

[illegible]

DESIGN DEVELOPMENT

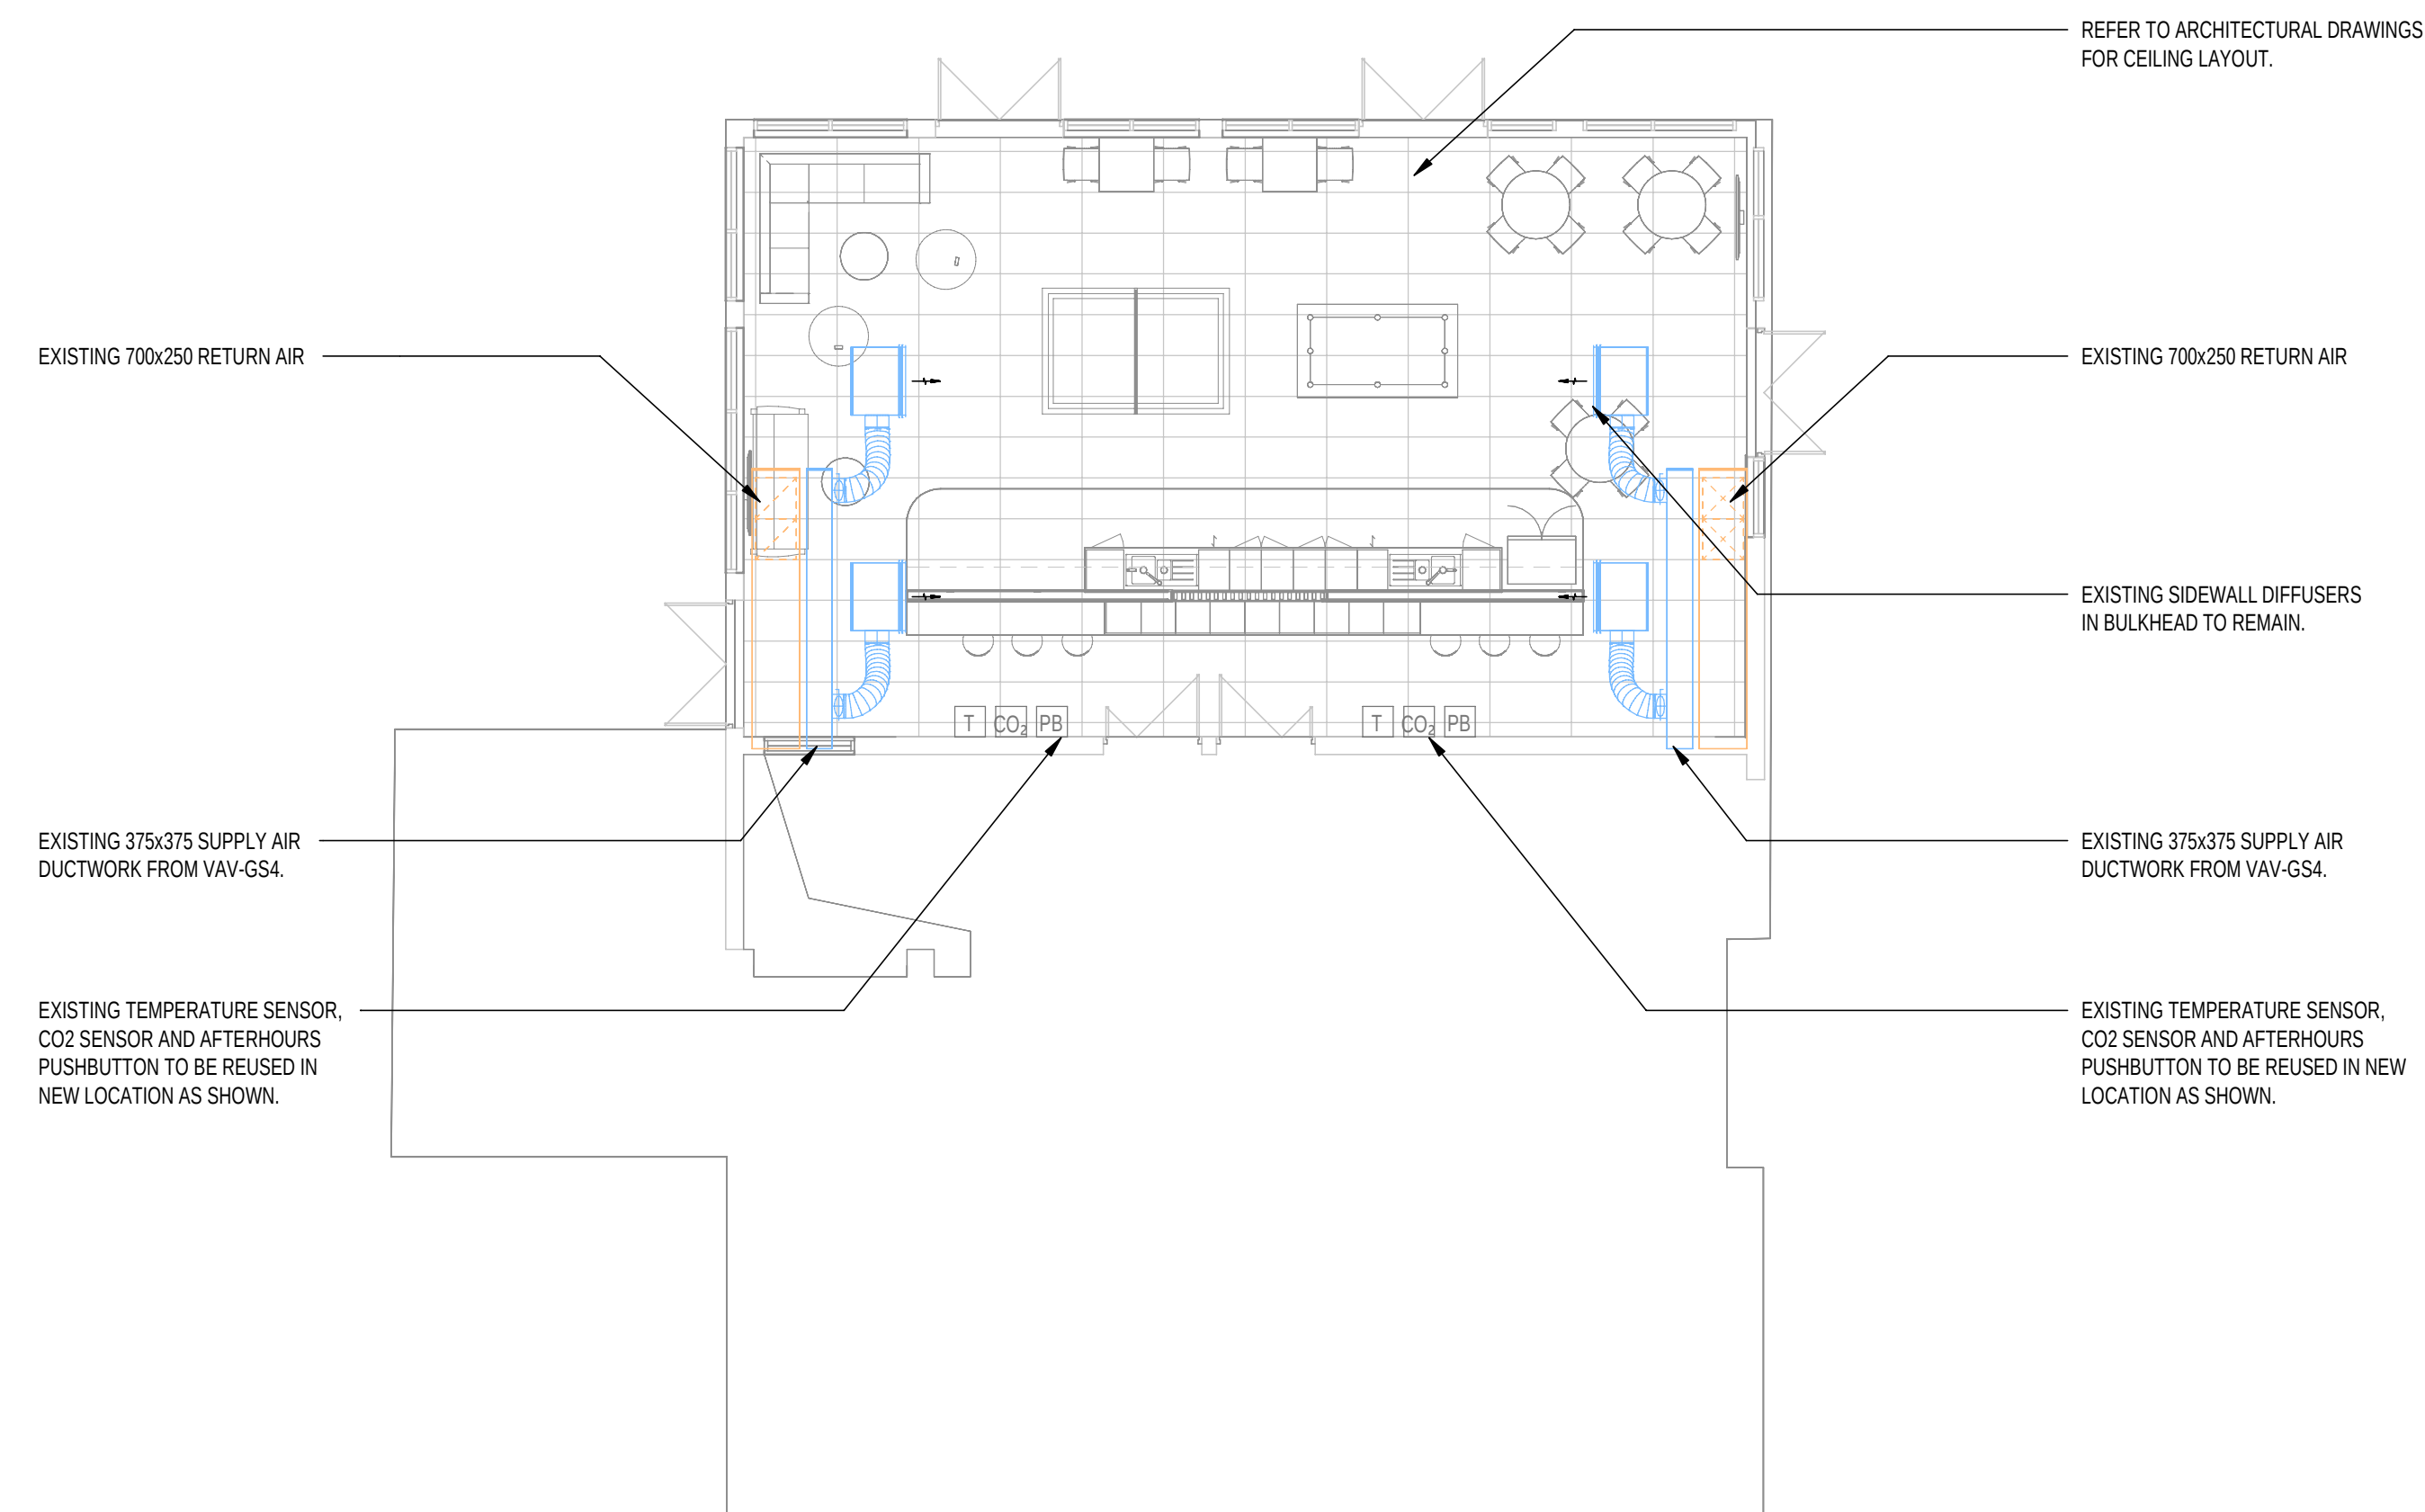

100 Ann Street, Level 12, Fortitude Valley 4006
Tel: +61-7-3854-6200 Fax: +61-7-3854-6500
<http://www.wsp.com>

CLIENT: CQU

ARCHITECT: THOMSON ADSETT / PEDDLE THORP

CQU ROCKHAMPTON TAFE CONSOLIDATION

TITLE:

MECHANICAL SERVICES
BUILDING 34 - GROUND LEVEL - HVAC LAYOUT

SCALE @ A0: 1:100	CHECKED: MB	APPROVED: SM
PROJECT NUMBER: PS229518	DRAWN: RD	DATE: FEB 2026

B34-ME-DR-510-L00-00-00

© WSP Australia Pty Ltd