


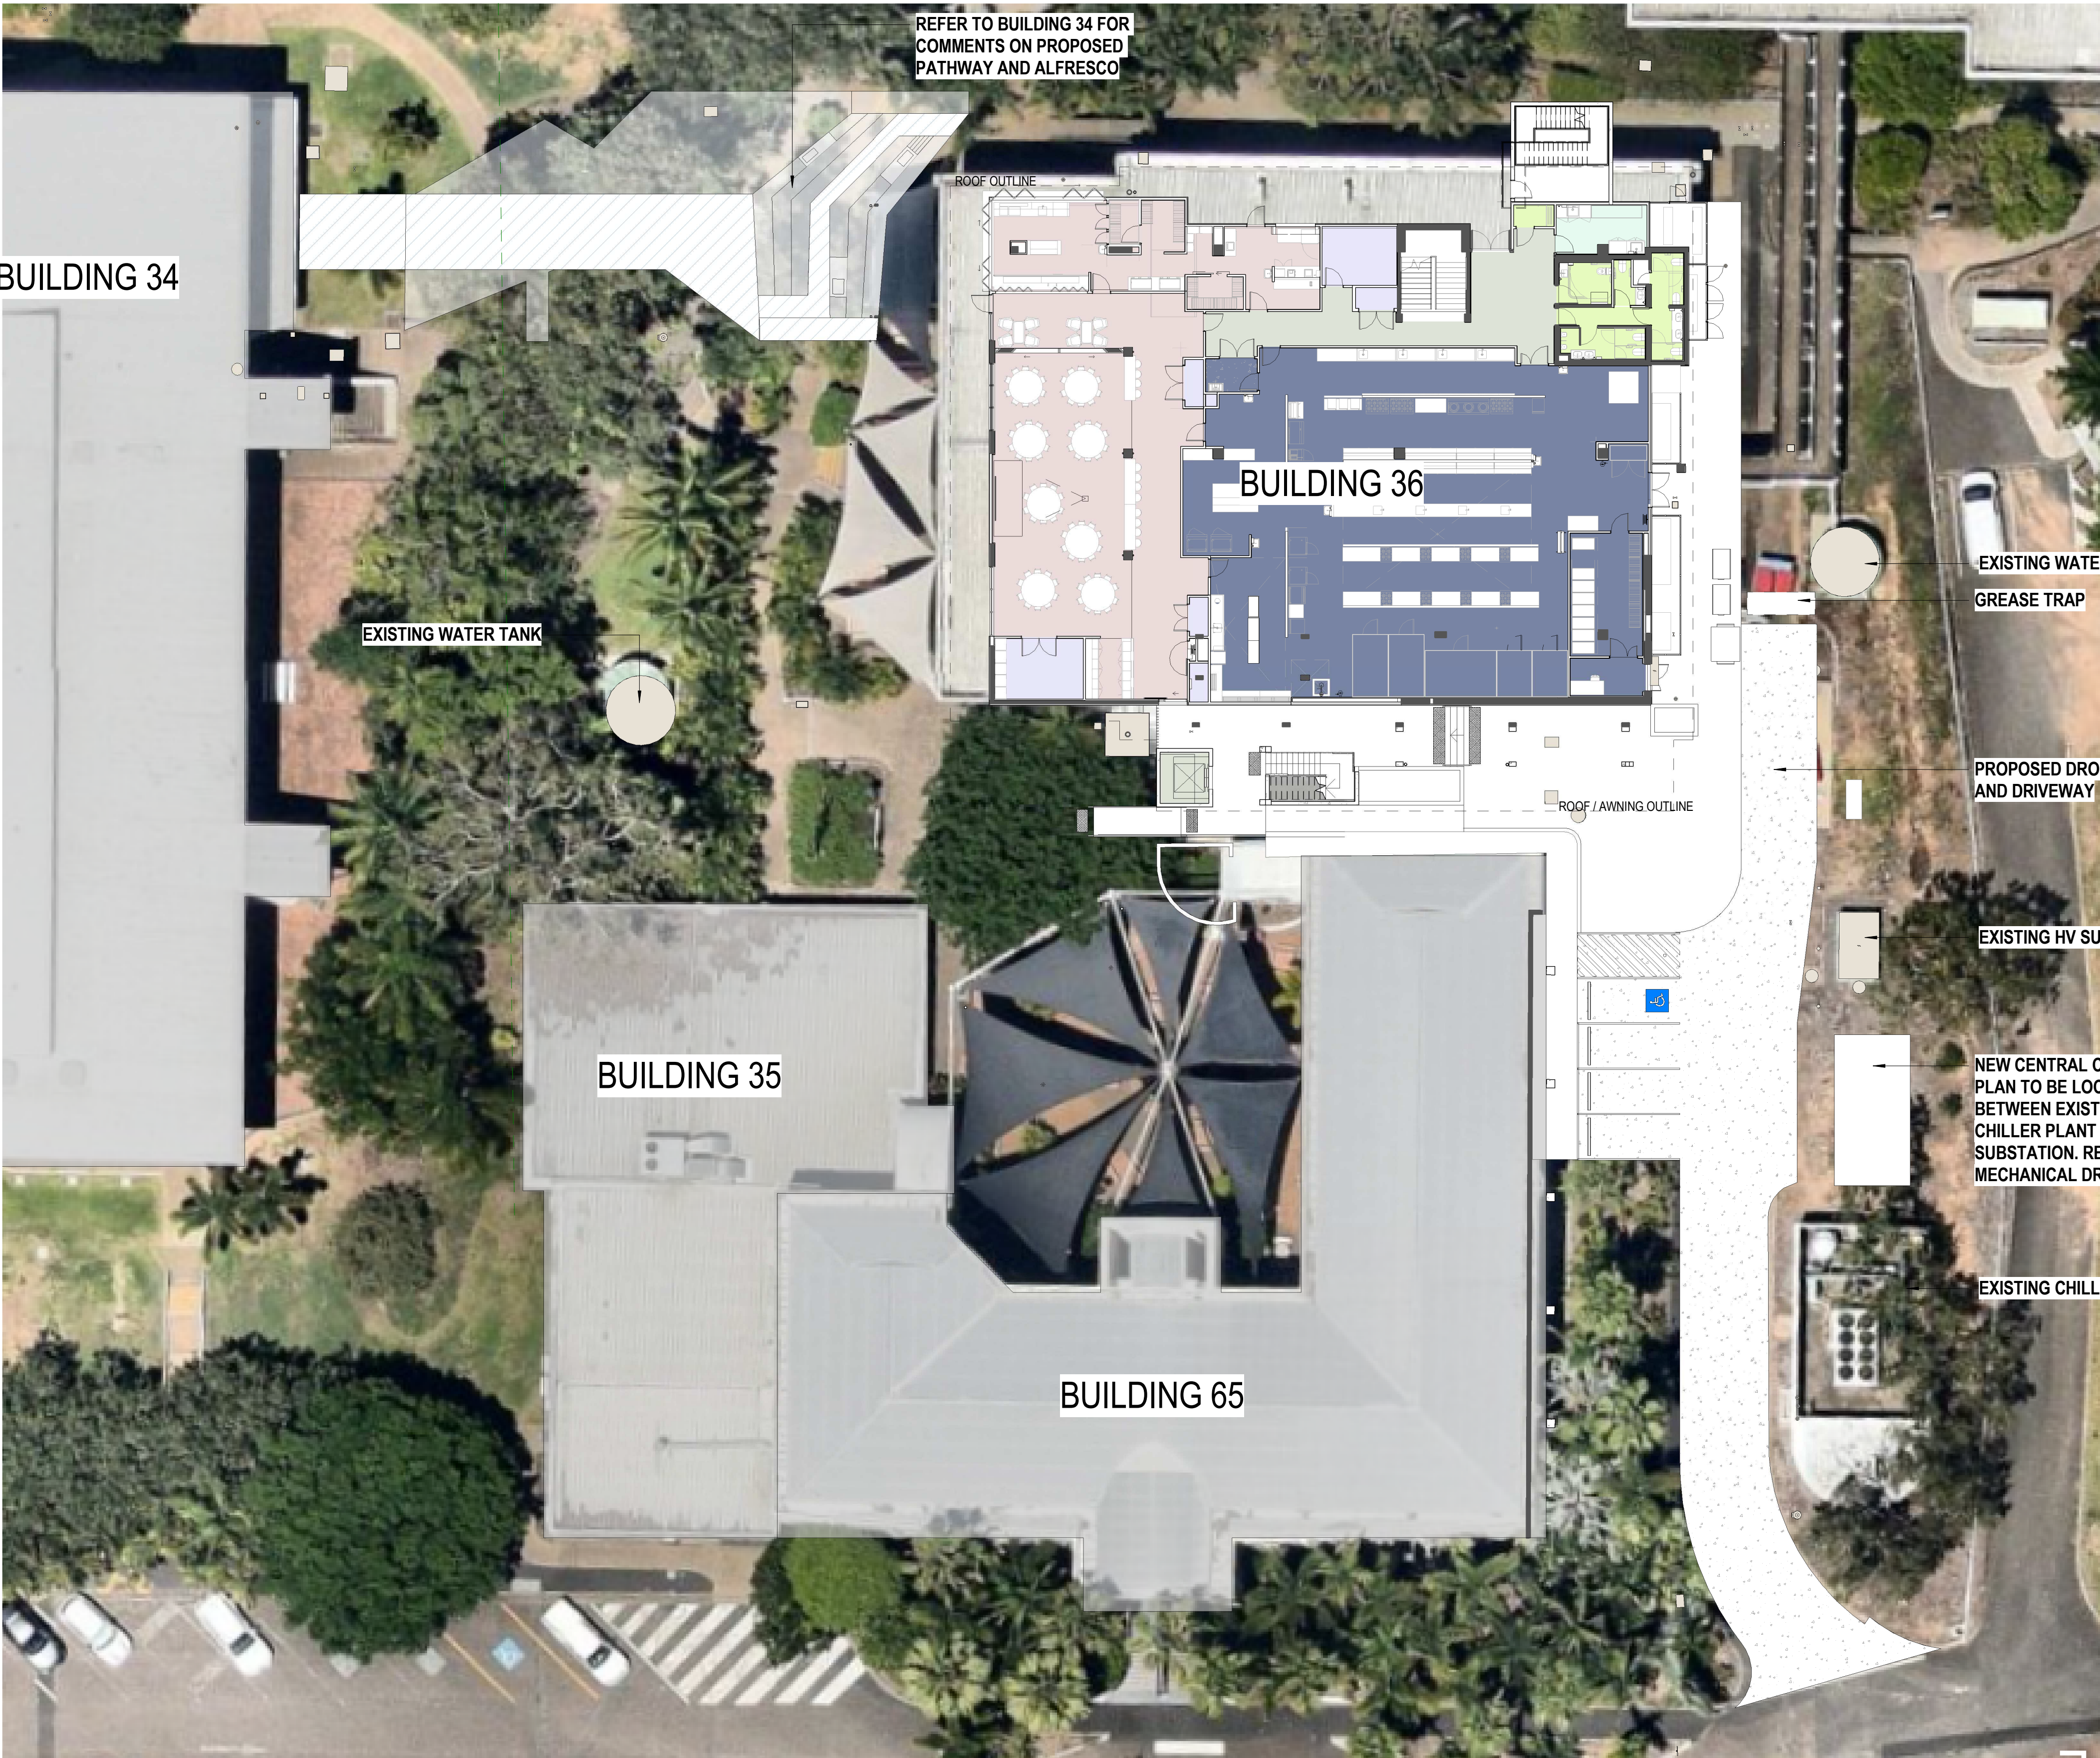

BUILDING 34

REFER TO BUILDING 34 FOR
COMMENTS ON PROPOSED
PATHWAY AND ALFRESCO

BUILDING 36

EXISTING WATER TANK

EXISTING WATER TANK

GREASE TRAP

PROPOSED DROP-OFF AREA
AND DRIVEWAY

EXISTING HV SUBSTATION

NEW CENTRAL CHILLER
PLAN TO BE LOCATED
BETWEEN EXISTING
CHILLER PLANT AND
SUBSTATION. REFER TO
MECHANICAL DRAWING.

EXISTING CHILLER PLANT

BUILDING 35

BUILDING 65

GENERAL NOTE

- REFER TO SURVEY DRAWINGS FOR MORE INFORMATION ON SITE FEATURES, CONDITIONS AND SERVICES
- CONTRACTOR TO CONFIRM EXISTING STRUCTURES AND SERVICES ON SITE PRIOR BUILDING WORK
- REFER TO LANDSCAPE AND CIVIL DRAWINGS FOR EXTENT OF EXTERNAL WORKS

thomson
adsett

PEDDLE THORP
architecture | interiors | health | planning

Telephone +61 7 3840 9999
bne@thomsonadsett.com
Level 9, 470 St Pauls Terrace
Fortitude Valley
Qld 4006 Australia
thomsonadsett.com

© Copyright
These drawings and designs and the copyright thereof are the property of Thomson Adsett Pty Ltd and must not be used, retained or copied without written permission of Thomson Adsett Pty Ltd. ABN 76 105 314 654 Trading as ThomsonAdsett. Dimensions take precedence over scaling. Do not measure off drawings as print sizes may vary


**CQU ROCKHAMPTON
TAFE
CONSOLIDATION -
STAGE 2**

554/700 Yaamba Rd, Norman
Gardens QLD 4701

for
**CQUniversity
AUSTRALIA**

B	2026-03-05	UPDATED ISSUED FOR TENDER	BC
A	2026-02-12	ISSUED FOR TENDER	BC
1	2026-01-30	60% DRAFT ISSUE	BC
rev	date	details	init.

drawn	date
JS/BC	19/01/2026
checked	date
SS	12/02/2026
verified	date

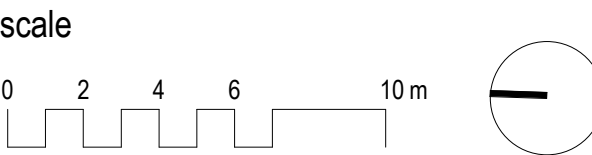

**SITE CONTEXT PLAN -
BUILDING 36**

scale
As indicated @ A1

project no.
25.0236.17

revision
B

sheet no.
CQU-ROK-036-00-ARC-10-00

ISSUED FOR TENDER