

CQU ROCKHAMPTON TAFE CONSOLIDATION - STAGE 2


554/700 Yaamba Rd, Norman
Gardens QLD 4701



B	2026-03-05	UPDATED ISSUED FOR TENDER	BC
A	2026-02-12	ISSUED FOR TENDER	BC
4	2026-01-30	60% DRAFT ISSUE	BC
3	2026-01-23	CONSULTANTS ISSUE	BC
2	2025-12-19	UPDATED ISSUE	BC
1	2025-12-17	CONSULTANTS REVIEW	BC

rev	date	details	init.
-----	------	---------	-------

drawn	date
JS/BC	19/01/2026
checked	date
SS	12/02/2026
verified	date

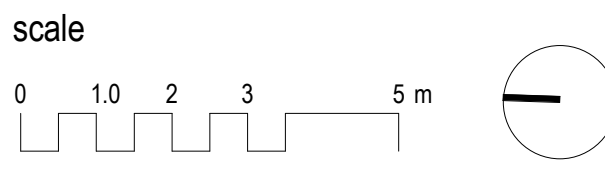


FLOOR PLAN - GROUND FLOOR - PROPOSED

scale
1 : 100 @ A1

project no.
25.0236.17

revision
B

sheet no.
CQU-ROK-036-GN-ARC-21-01

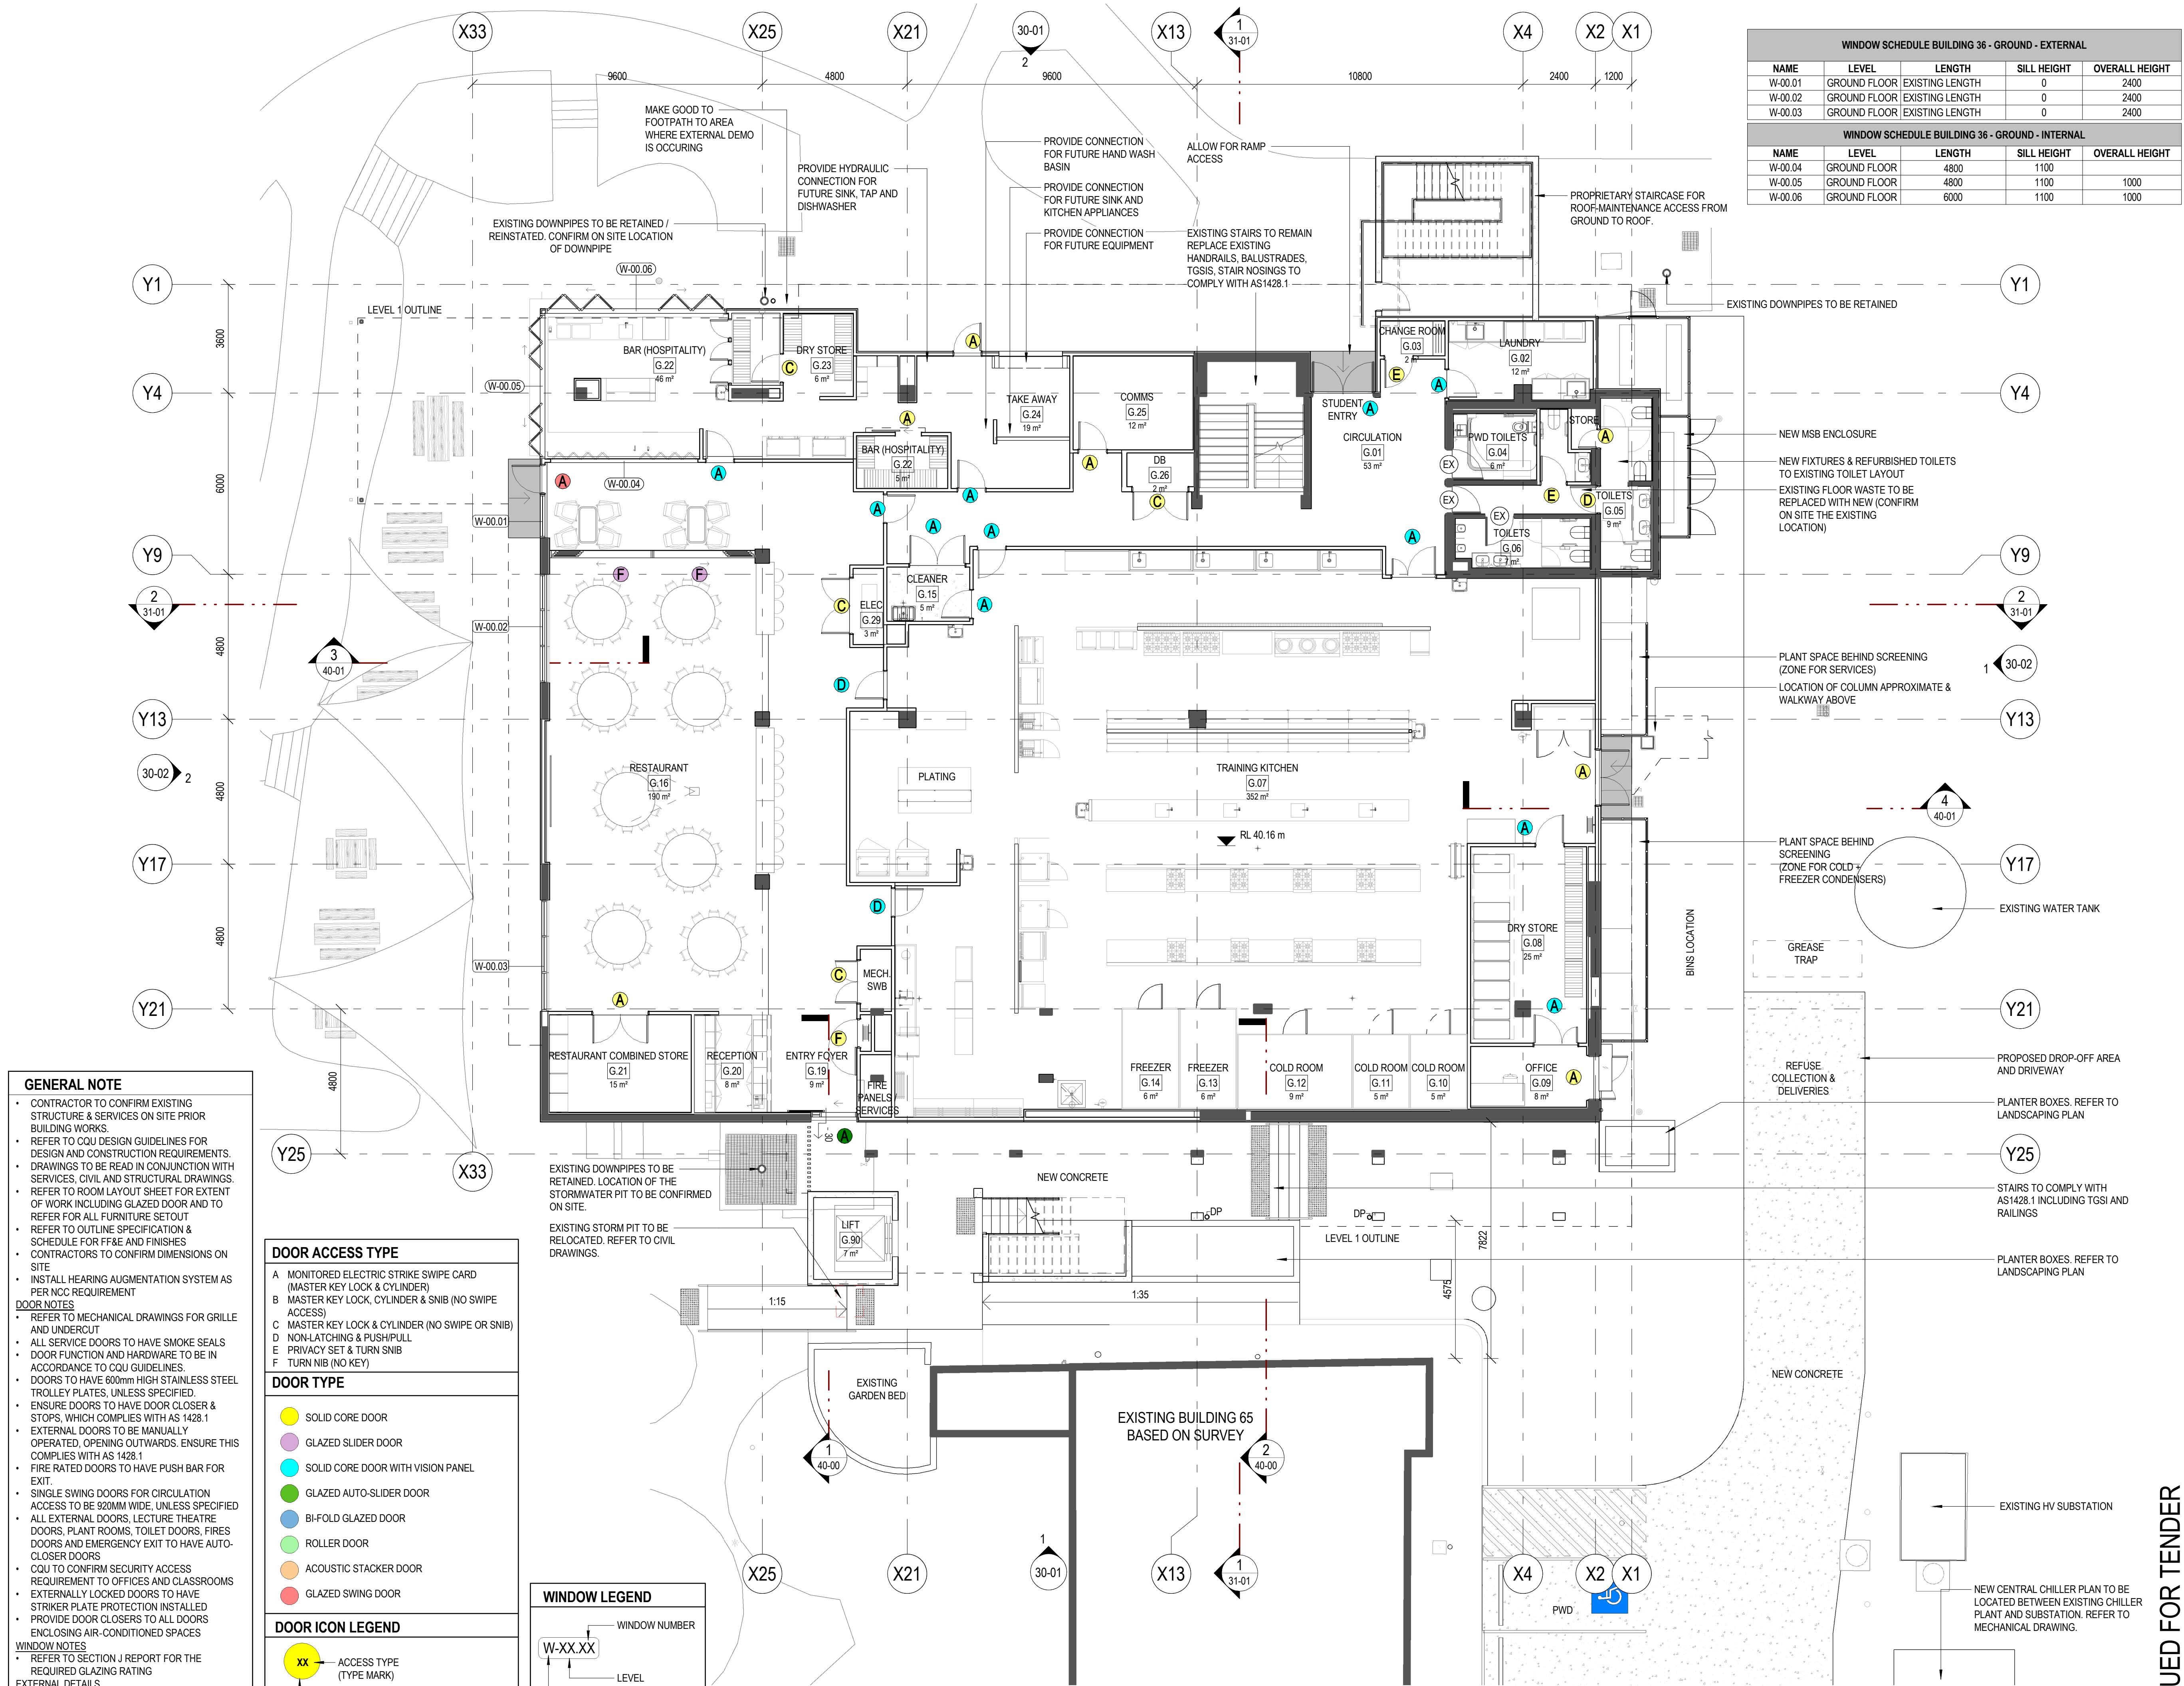

GENERAL NOTE

- CONTRACTOR TO CONFIRM EXISTING STRUCTURE & SERVICES ON SITE PRIOR BUILDING WORKS.
- REFER TO CQU DESIGN GUIDELINES FOR DESIGN AND CONSTRUCTION REQUIREMENTS.
- DRAWINGS TO BE READ IN CONJUNCTION WITH SERVICES, CIVIL AND STRUCTURAL DRAWINGS.
- REFER TO ROOM LAYOUT SHEET FOR EXTENT OF WORK INCLUDING GLAZED DOOR AND TO REFER FOR ALL FURNITURE SETOUT
- REFER TO OUTLINE SPECIFICATION & SCHEDULE FOR FF&E AND FINISHES
- CONTRACTORS TO CONFIRM DIMENSIONS ON SITE
- INSTALL HEARING AUGMENTATION SYSTEM AS PER RCC REQUIREMENT

DOOR NOTES

- REFER TO MECHANICAL DRAWINGS FOR GRILLE AND UNDERCUT
- ALL SERVICE DOORS TO HAVE SMOKE SEALS
- DOOR FUNCTION AND HARDWARE TO BE IN ACCORDANCE TO CQU GUIDELINES.
- DOORS TO HAVE 600mm HIGH STAINLESS STEEL TROLLEY PLATES, UNLESS SPECIFIED.
- ENSURE DOORS TO HAVE DOOR CLOSER & STOPS, WHICH COMPLIES WITH AS 1428.1
- EXTERNAL DOORS TO BE MANUALLY OPERATED, OPENING OUTWARDS. ENSURE THIS COMPLIES WITH AS 1428.1
- FIRE RATED DOORS TO HAVE PUSH BAR FOR EXIT.
- SINGLE SWING DOORS FOR CIRCULATION ACCESS TO BE 920MM WIDE, UNLESS SPECIFIED
- ALL EXTERNAL DOORS, LECTURE THEATRE DOORS, PLANT ROOMS, TOILET DOORS, FIRES DOORS AND EMERGENCY EXIT TO HAVE AUTO-CLOSER DOORS
- CQU TO CONFIRM SECURITY ACCESS REQUIREMENT TO OFFICES AND CLASSROOMS
- EXTERNALLY LOCKED DOORS TO HAVE STRIKER PLATE PROTECTION INSTALLED
- PROVIDE DOOR CLOSERS TO ALL DOORS ENCLOSING AIR-CONDITIONED SPACES

WINDOW NOTES

- REFER TO SECTION J REPORT FOR THE REQUIRED GLAZING RATING
- SITE DETAILS SHOWN IN HALF TONE
- NOTED FOR REFERENCE ONLY

DOOR ACCESS TYPE

- A MONITORED ELECTRIC STRIKE SWIPE CARD (MASTER KEY LOCK & CYLINDER)
- B MASTER KEY LOCK, CYLINDER & SNIB (NO SWIPE ACCESS)
- C MASTER KEY LOCK & CYLINDER (NO SWIPE OR SNIB)
- D NON-LATCHING & PUSH/PULL
- E PRIVACY SET & TURN SNIB
- F TURN NIB (NO KEY)

DOOR TYPE

- SOLID CORE DOOR
- GLAZED SLIDER DOOR
- SOLID CORE DOOR WITH VISION PANEL
- GLAZED AUTO-SLIDER DOOR
- BI-FOLD GLAZED DOOR
- ROLLER DOOR
- ACOUSTIC STACKER DOOR
- GLAZED SWING DOOR

DOOR ICON LEGEND

- xx ACCESS TYPE (TYPE MARK)
- DOOR TYPE (COLOUR SHADE)

WINDOW LEGEND

- WINDOW NUMBER
- LEVEL
- WINDOW PREFIX

WINDOW SCHEDULE BUILDING 36 - GROUND - EXTERNAL				
NAME	LEVEL	LENGTH	SILL HEIGHT	OVERALL HEIGHT
W-00.01	GROUND FLOOR	EXISTING LENGTH	0	2400
W-00.02	GROUND FLOOR	EXISTING LENGTH	0	2400
W-00.03	GROUND FLOOR	EXISTING LENGTH	0	2400

WINDOW SCHEDULE BUILDING 36 - GROUND - INTERNAL				
NAME	LEVEL	LENGTH	SILL HEIGHT	OVERALL HEIGHT
W-00.04	GROUND FLOOR	4800	1100	
W-00.05	GROUND FLOOR	4800	1100	1000
W-00.06	GROUND FLOOR	6000	1100	1000

ISSUED FOR TENDER