


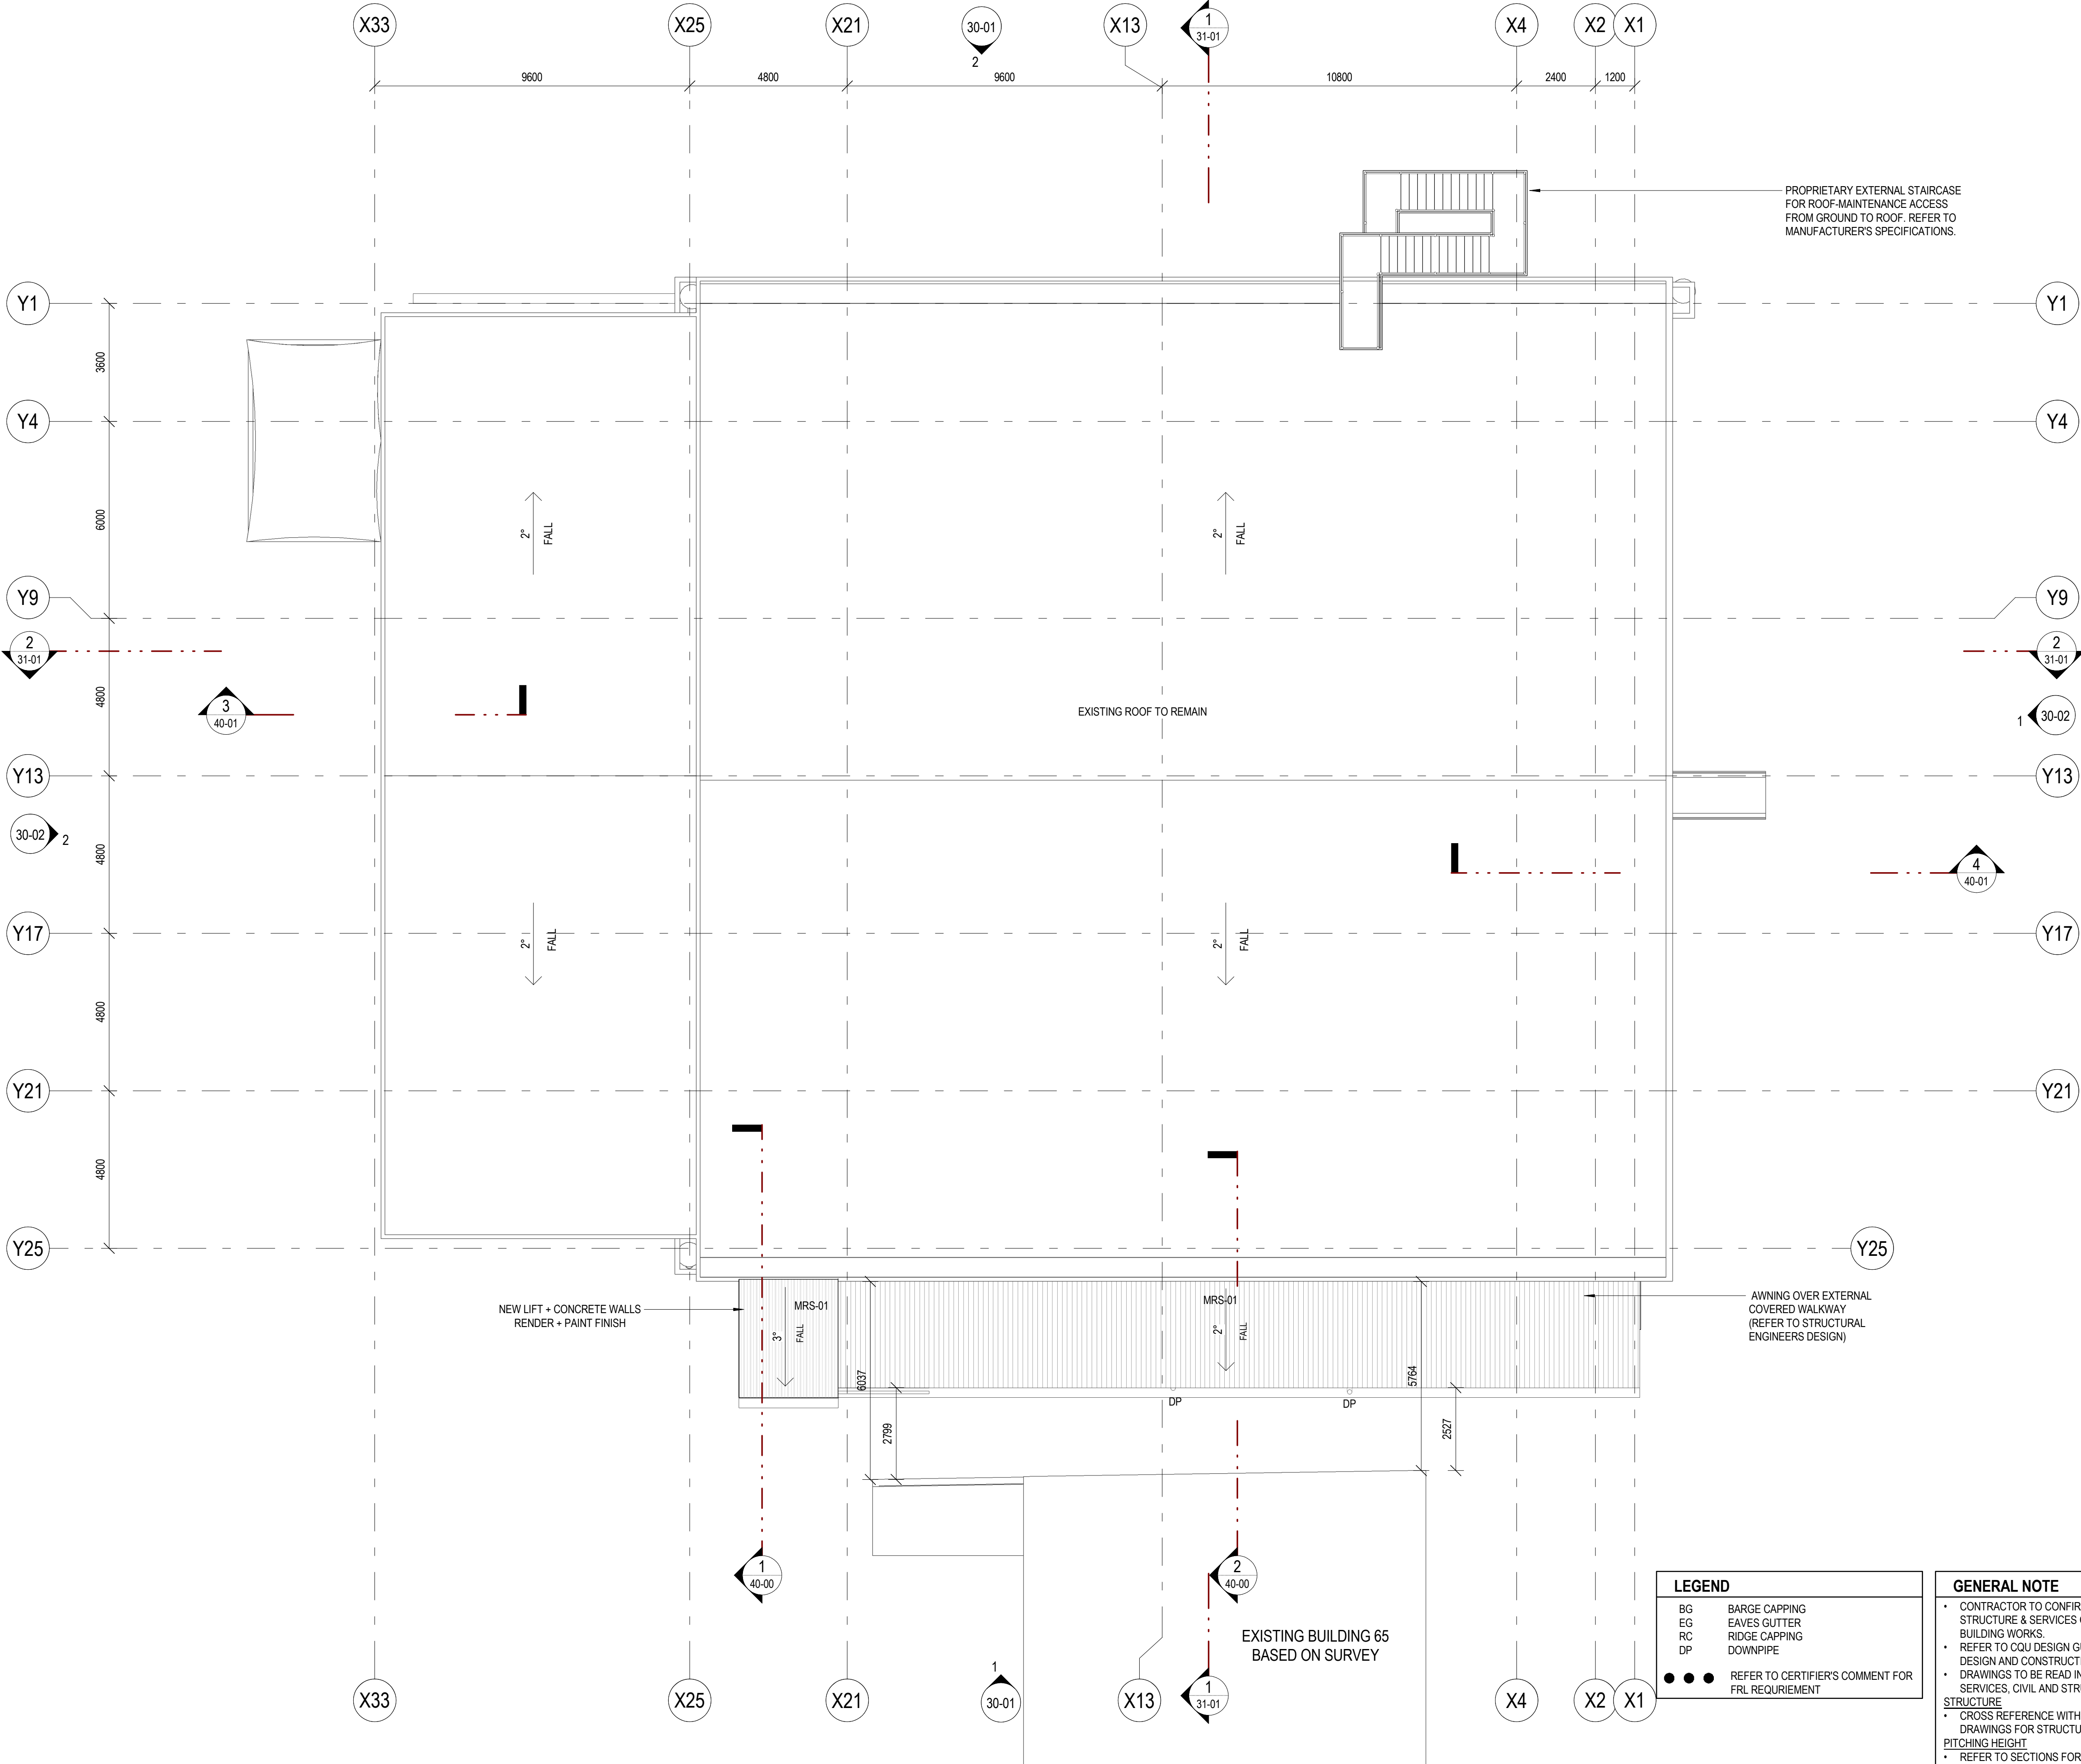


**CQU ROCKHAMPTON
TAFE
CONSOLIDATION -
STAGE 2**

554/700 Yaamba Rd, Norman
Gardens QLD 4701



B	2026-03-05	UPDATED ISSUED FOR TENDER	BC
A	2026-02-12	ISSUED FOR TENDER	BC
3	2026-01-30	60% DRAFT ISSUE	BC
2	2026-01-23	CONSULTANTS ISSUE	BC
1	2025-12-19	UPDATED ISSUE	BC

drawn	date
JS/BC	19/01/2026
checked	date
SS	12/02/2026
verified	date

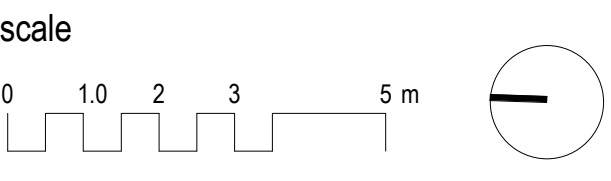

**FLOOR PLAN - ROOF
PLAN_PROPOSED**

scale	project no.
1 : 100 @ A1	25.0236.17

revision
B
sheet no.
CQU-ROK-036-RF-ARC-21-03

ISSUED FOR TENDER

GENERAL NOTE

- CONTRACTOR TO CONFIRM EXISTING STRUCTURE & SERVICES ON SITE PRIOR BUILDING WORKS.
- REFER TO CQU DESIGN GUIDELINES FOR DESIGN AND CONSTRUCTION REQUIREMENTS.
- DRAWINGS TO BE READ IN CONJUNCTION WITH SERVICES, CIVIL AND STRUCTURAL DRAWINGS.

STRUCTURE

- CROSS REFERENCE WITH ENGINEERS DRAWINGS FOR STRUCTURAL MEMBER SIZE

PITCHING HEIGHT

- REFER TO SECTIONS FOR ROOF PITCHING HEIGHTS

ROOF SAFETY

- ROOF ACCESS SYSTEM TO BE DESIGNED AND INSTALLED BY BUILDER. ACCESS TO BE PROVIDED TO GUTTER, SKYLIGHTS & ROOF WINDOWS (CLERESTORY), SOLAR PANELS, ROOF MOUNTED PLANT & ALL PENETRATIONS.

LEGEND	
BG	BARGE CAPPING
EG	EAVES GUTTER
RC	RIDGE CAPPING
DP	DOWNPIPE
● ● ●	REFER TO CERTIFIER'S COMMENT FOR FRL REQUIREMENT