


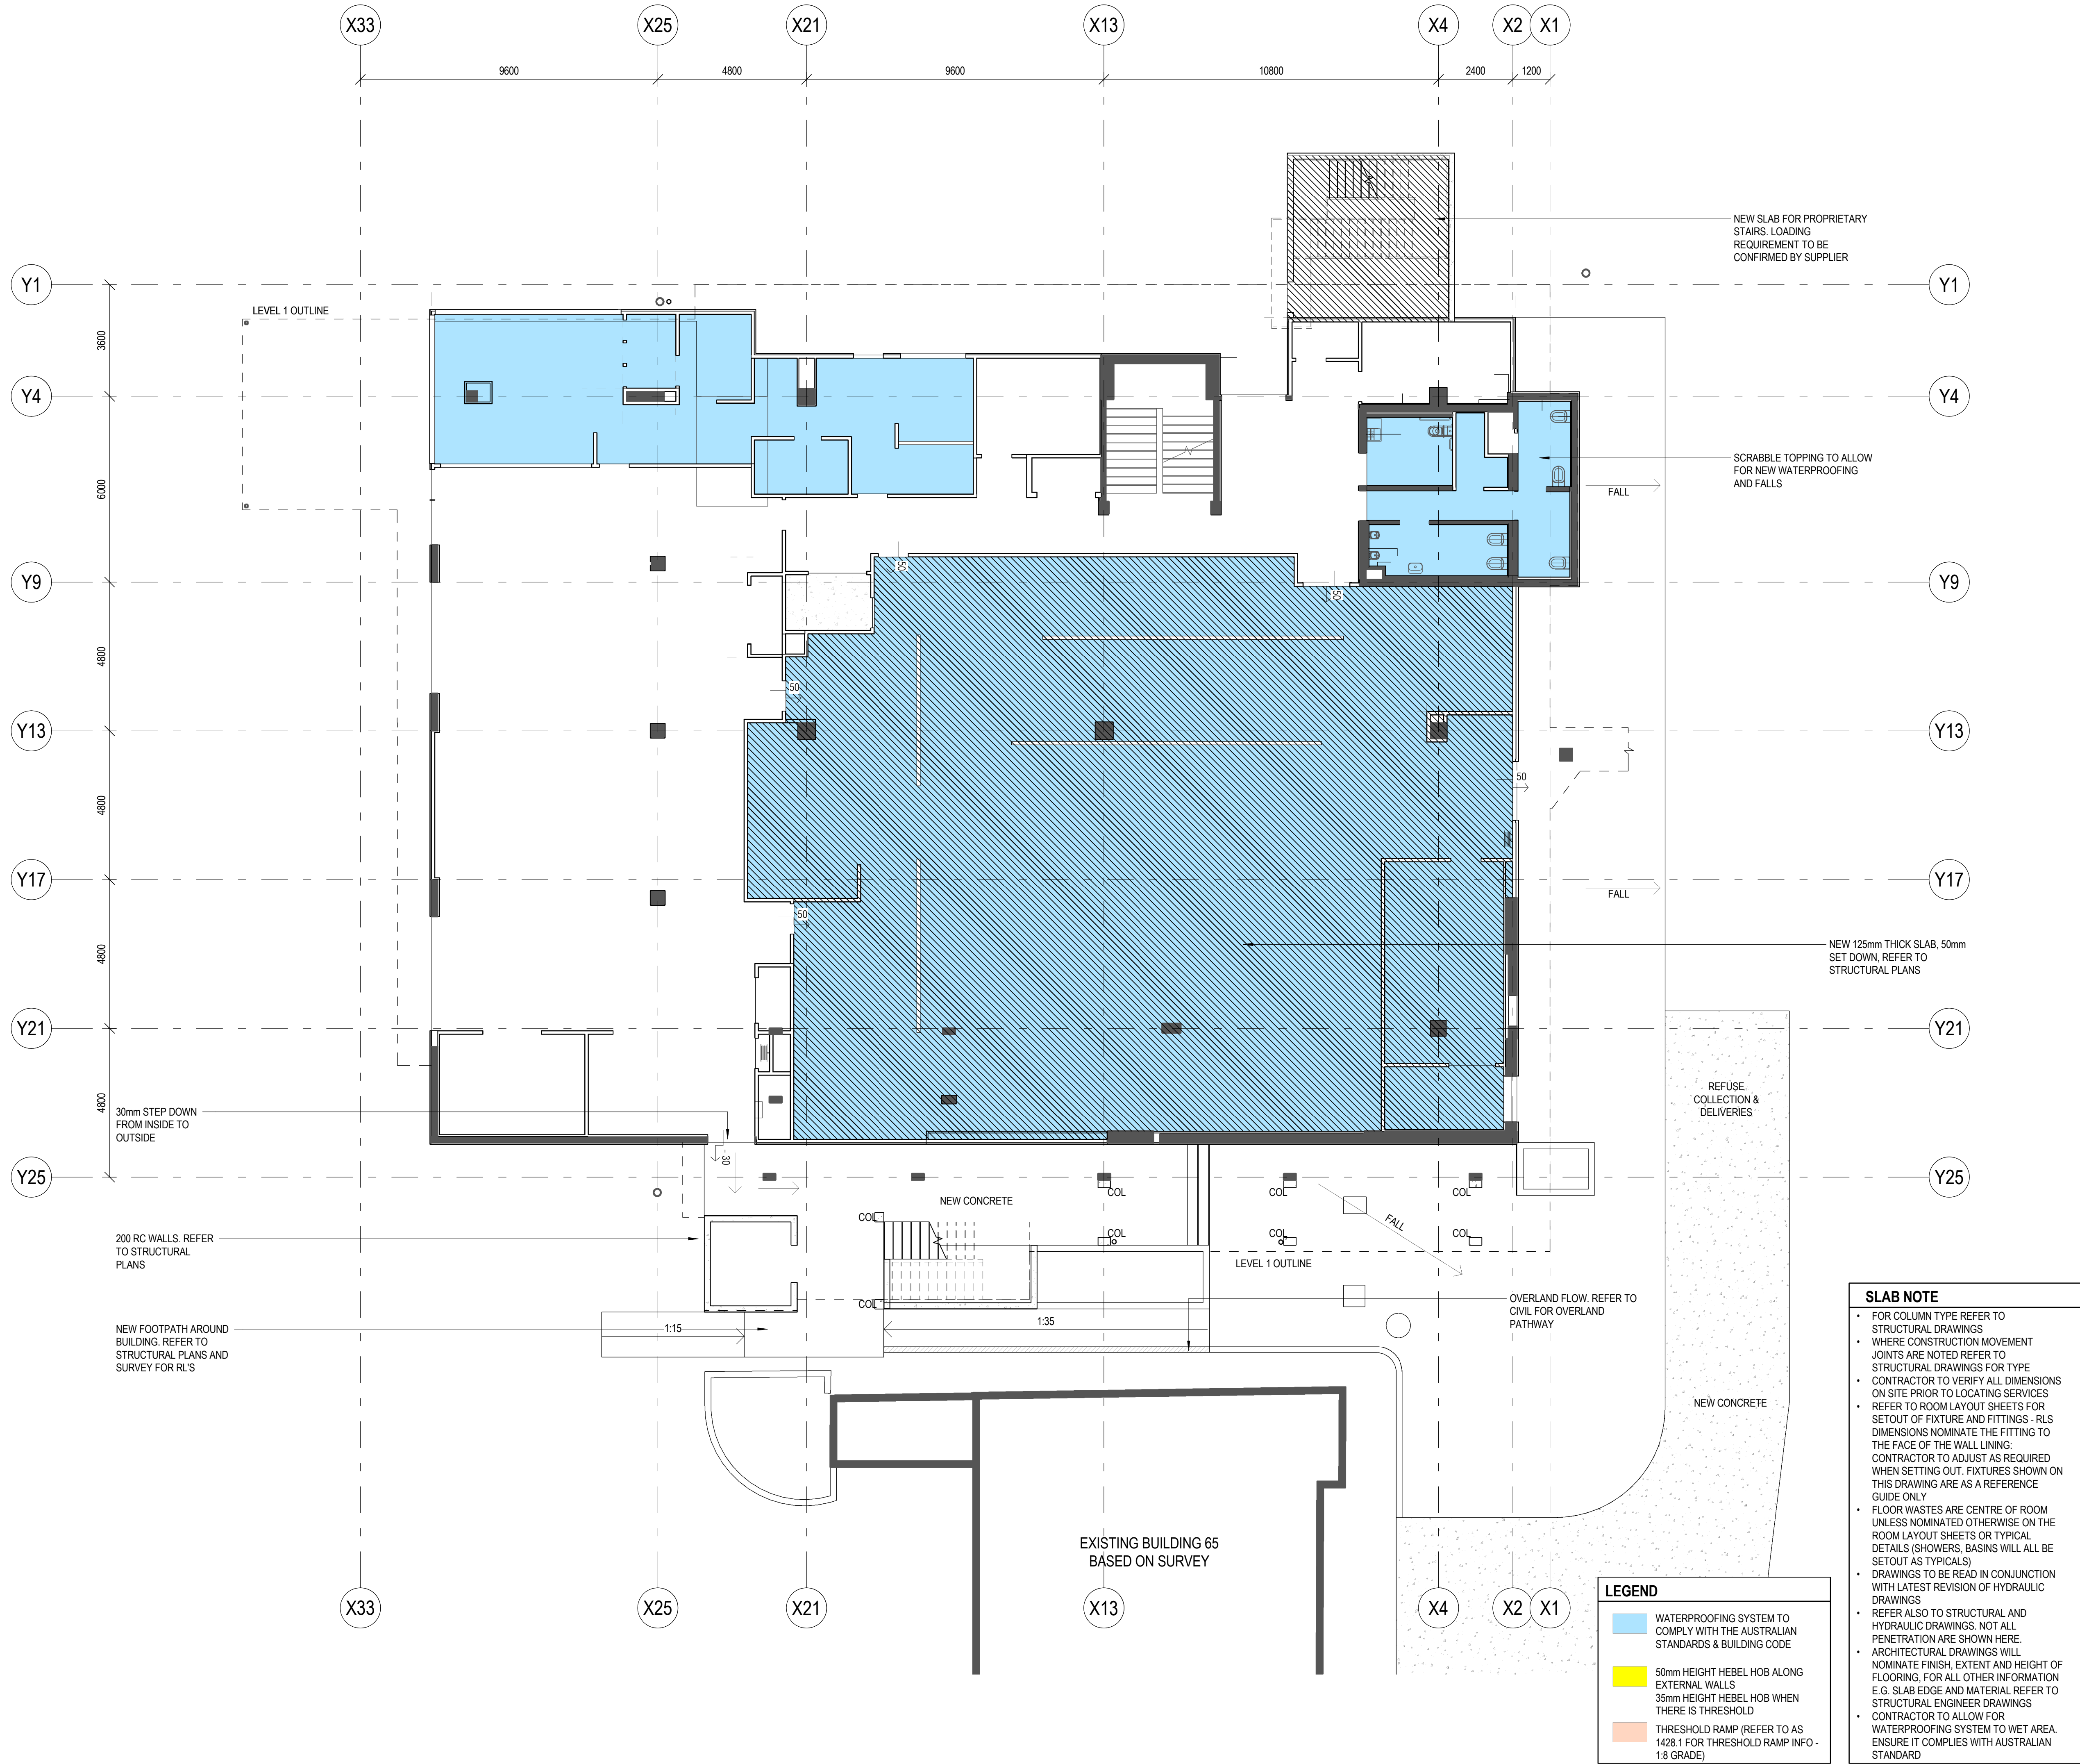


CQU ROCKHAMPTON TAFE CONSOLIDATION - STAGE 2

554/700 Yaamba Rd, Norman
Gardens QLD 4701



B	2026-03-05	UPDATED ISSUED FOR TENDER	BC
A	2026-02-12	ISSUED FOR TENDER	BC
1	2026-01-30	60% DRAFT ISSUE	BC
rev	date	details	init.

drawn	date
JS/BC	19/01/2026
checked	date
SS	12/02/2026
verified	date

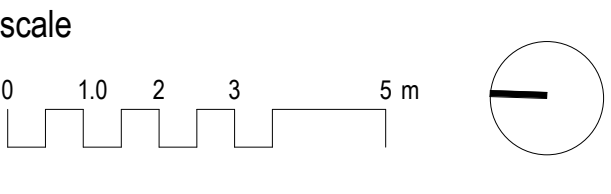

SLAB PLAN - GROUND FLOOR

scale	project no.
1 : 100 @ A1	25.0236.17

revision	
B	

sheet no.	
CQU-ROK-036-GN-ARC-23-01	

ISSUED FOR TENDER