

**CQU ROCKHAMPTON
TAFE
CONSOLIDATION -
STAGE 2**

554/700 Yaamba Rd, Norman
Gardens QLD 4701

for



CQUniversity
AUSTRALIA

B	2026-03-05	UPDATED ISSUED FOR TENDER	BC
A	2026-02-12	ISSUED FOR TENDER	BC
1	2026-01-30	60% DRAFT ISSUE	BC
rev	date	details	init
drawn	date		
JS/BC	19/01/2026		
checked	date		
SS	12/02/2026		
verified	date		

scale




0 1.0 2 3 5 m





PARTITION PLAN - GROUND FLOOR

scale project no.
As indicated @ A1 25.0236.17
revision
B
sheet no.
CQU-ROK-036-GN-ARC-26-0

original sheet size - A1 (594mm x 841mm)

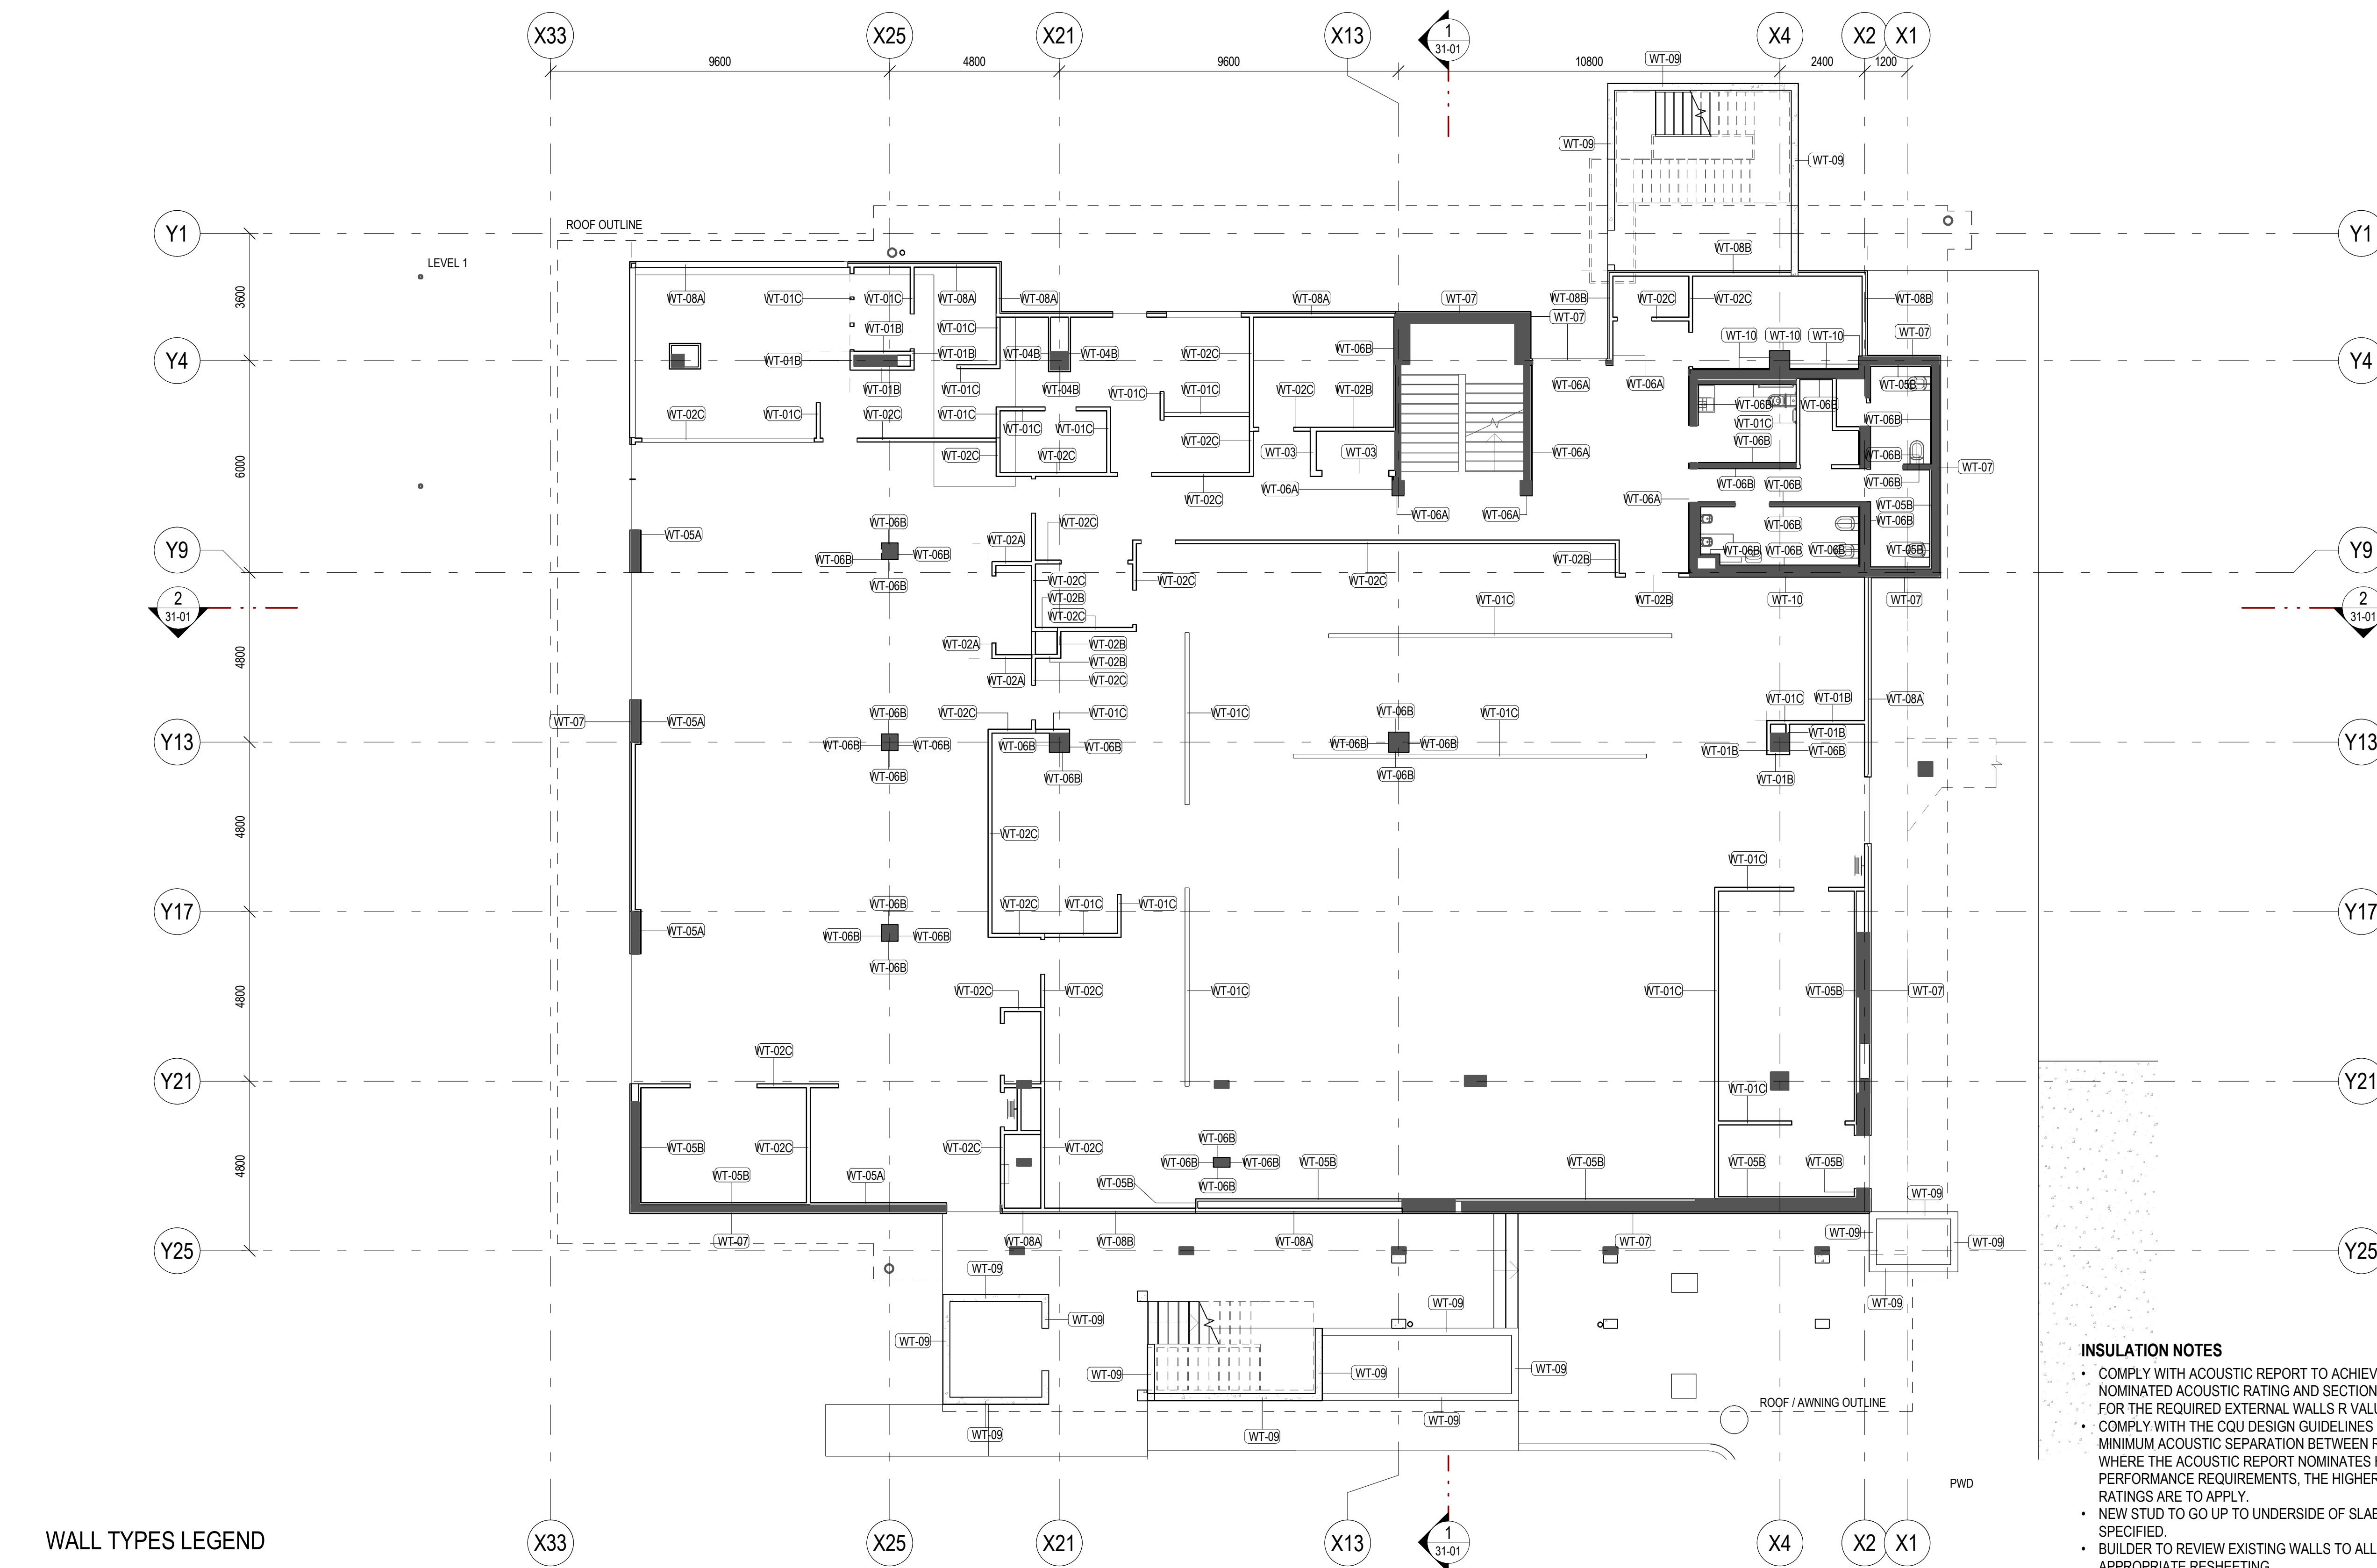


WALL TYPES LEGEND

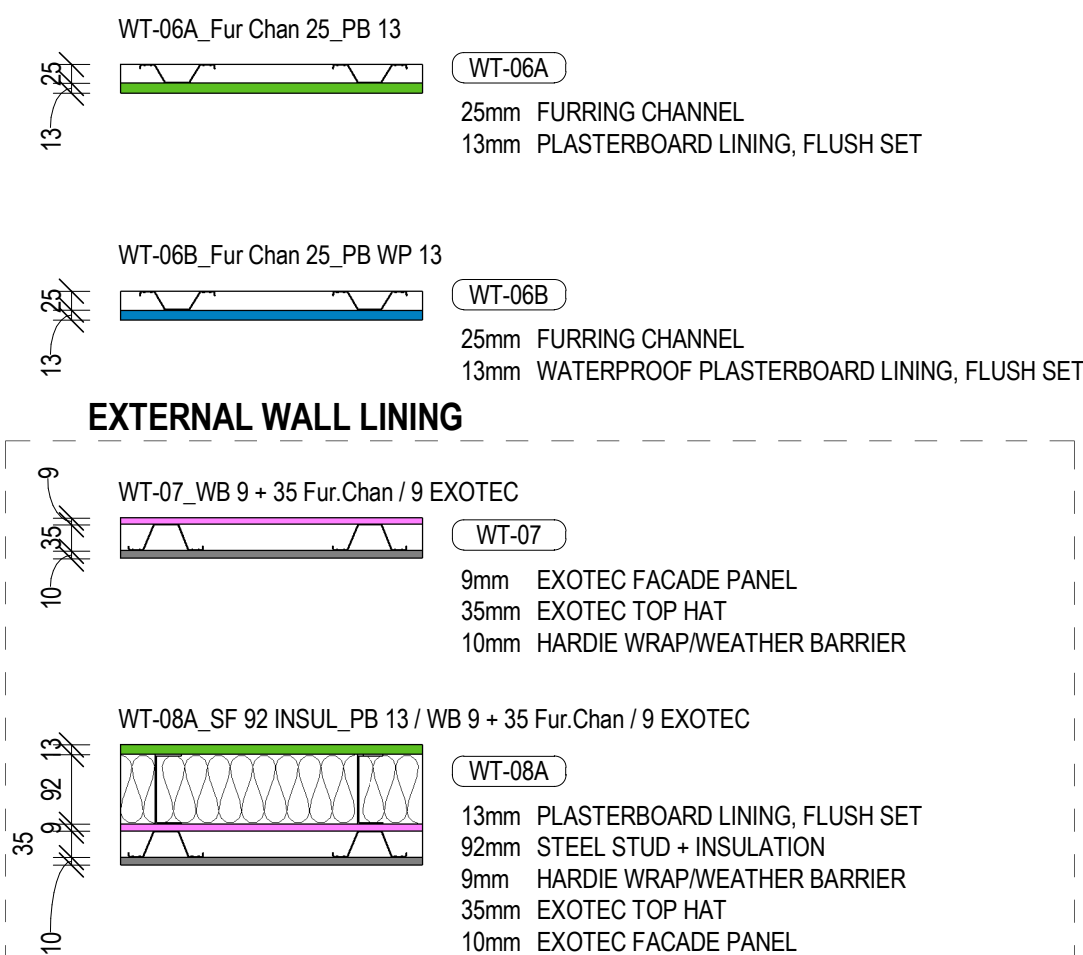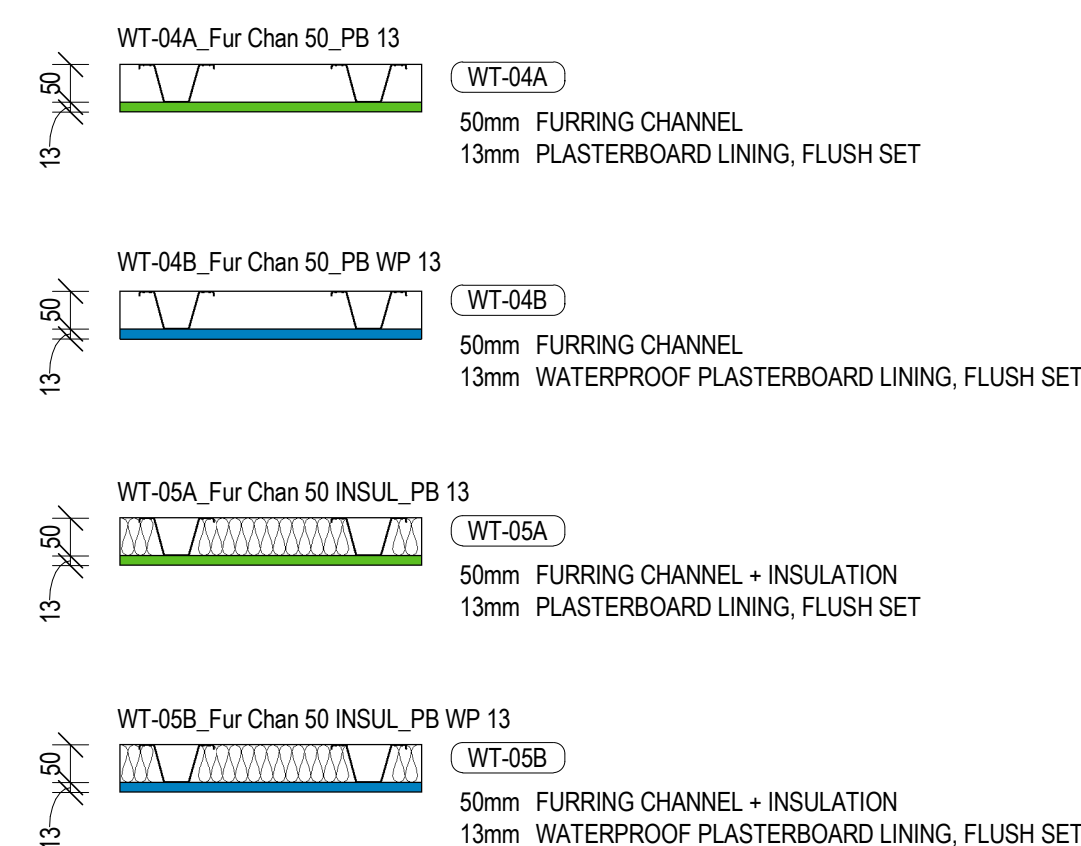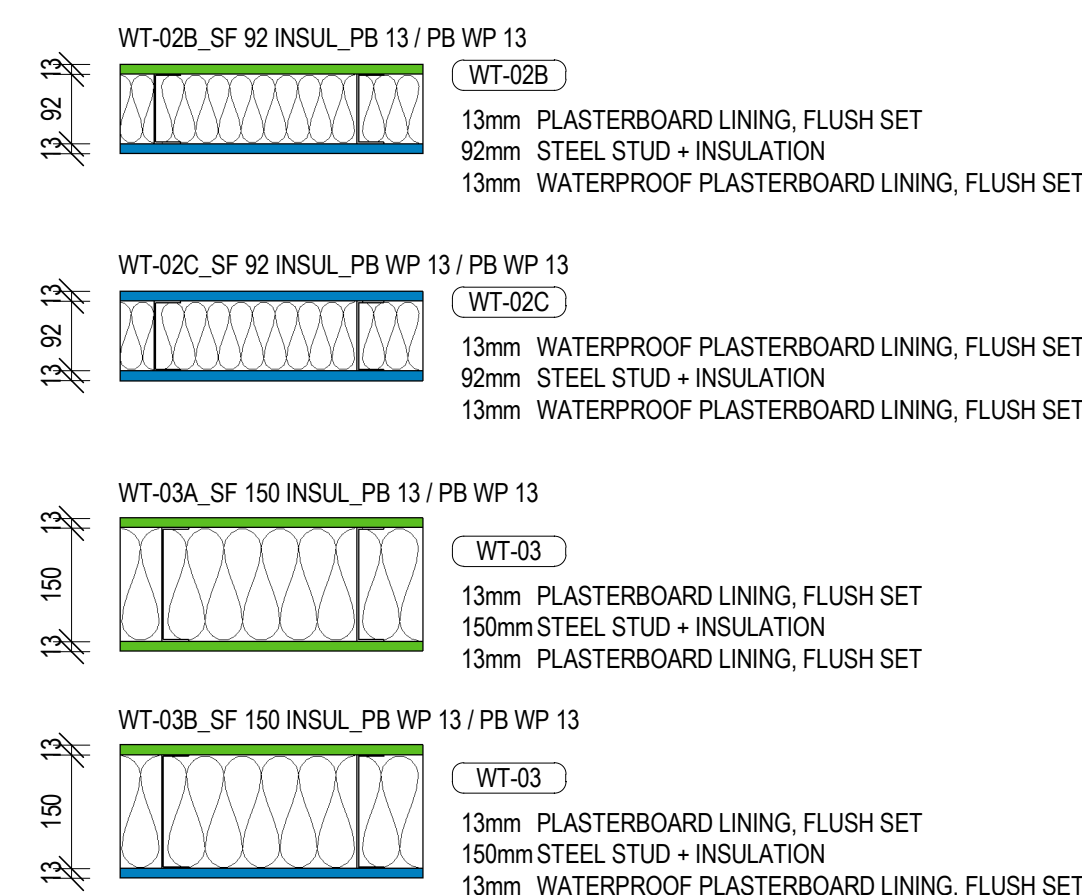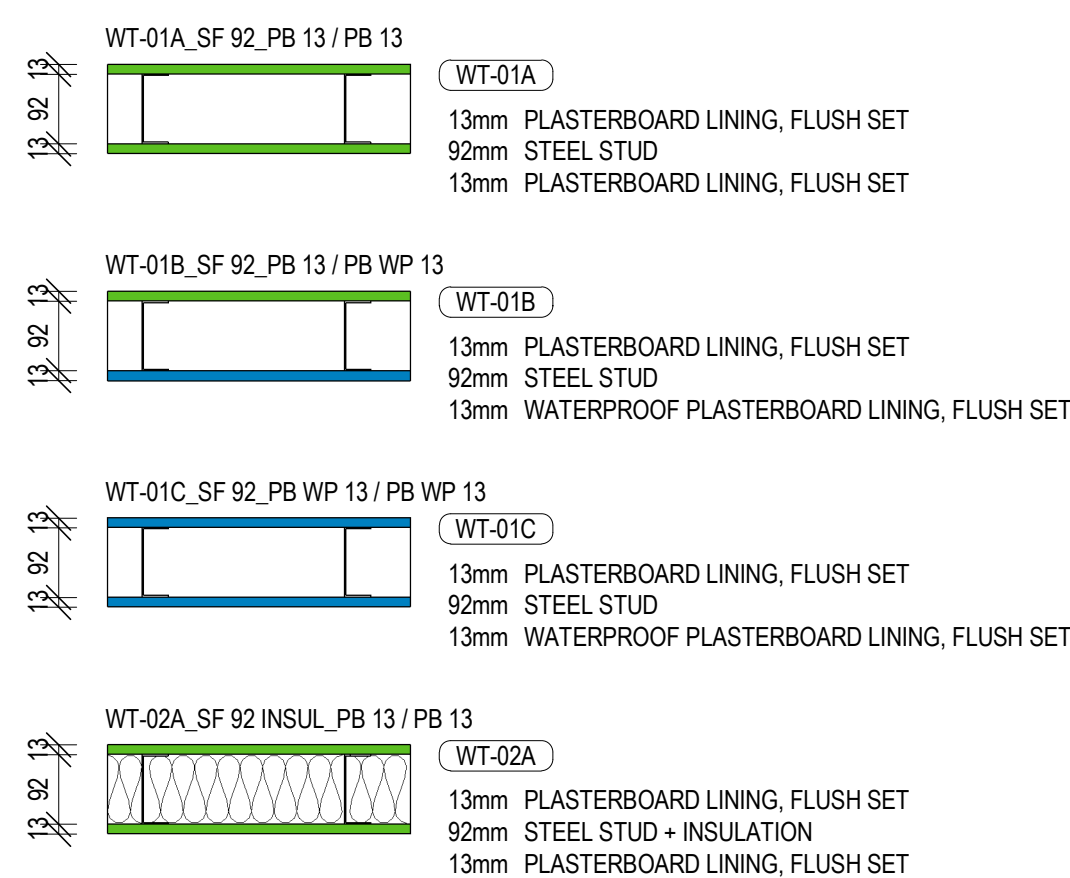

INSULATION NOTES

- COMPLY WITH ACOUSTIC REPORT TO ACHIEVE THE NOMINATED ACOUSTIC RATING AND SECTION J REPORT FOR THE REQUIRED EXTERNAL WALLS R VALUES.
- COMPLY WITH THE CQU DESIGN GUIDELINES FOR MINIMUM ACOUSTIC SEPARATION BETWEEN ROOMS. WHERE THE ACOUSTIC REPORT NOMINATES HIGHER PERFORMANCE REQUIREMENTS, THE HIGHER RW RATINGS ARE TO APPLY.
- NEW STUD TO GO UP TO UNDERSIDE OF SLAB, UNLESS SPECIFIED.
- BUILDER TO REVIEW EXISTING WALLS TO ALLOW FOR APPROPRIATE RESEETING

EXTERNAL WALL LINING

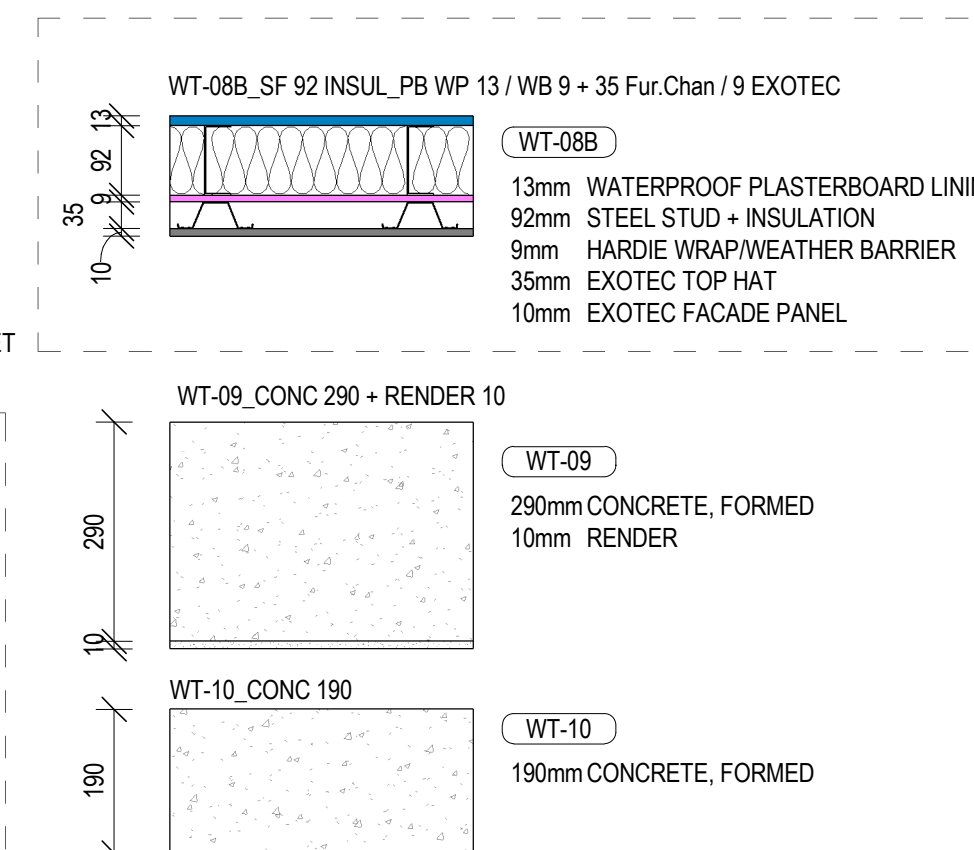

ISSUED FOR TENDER