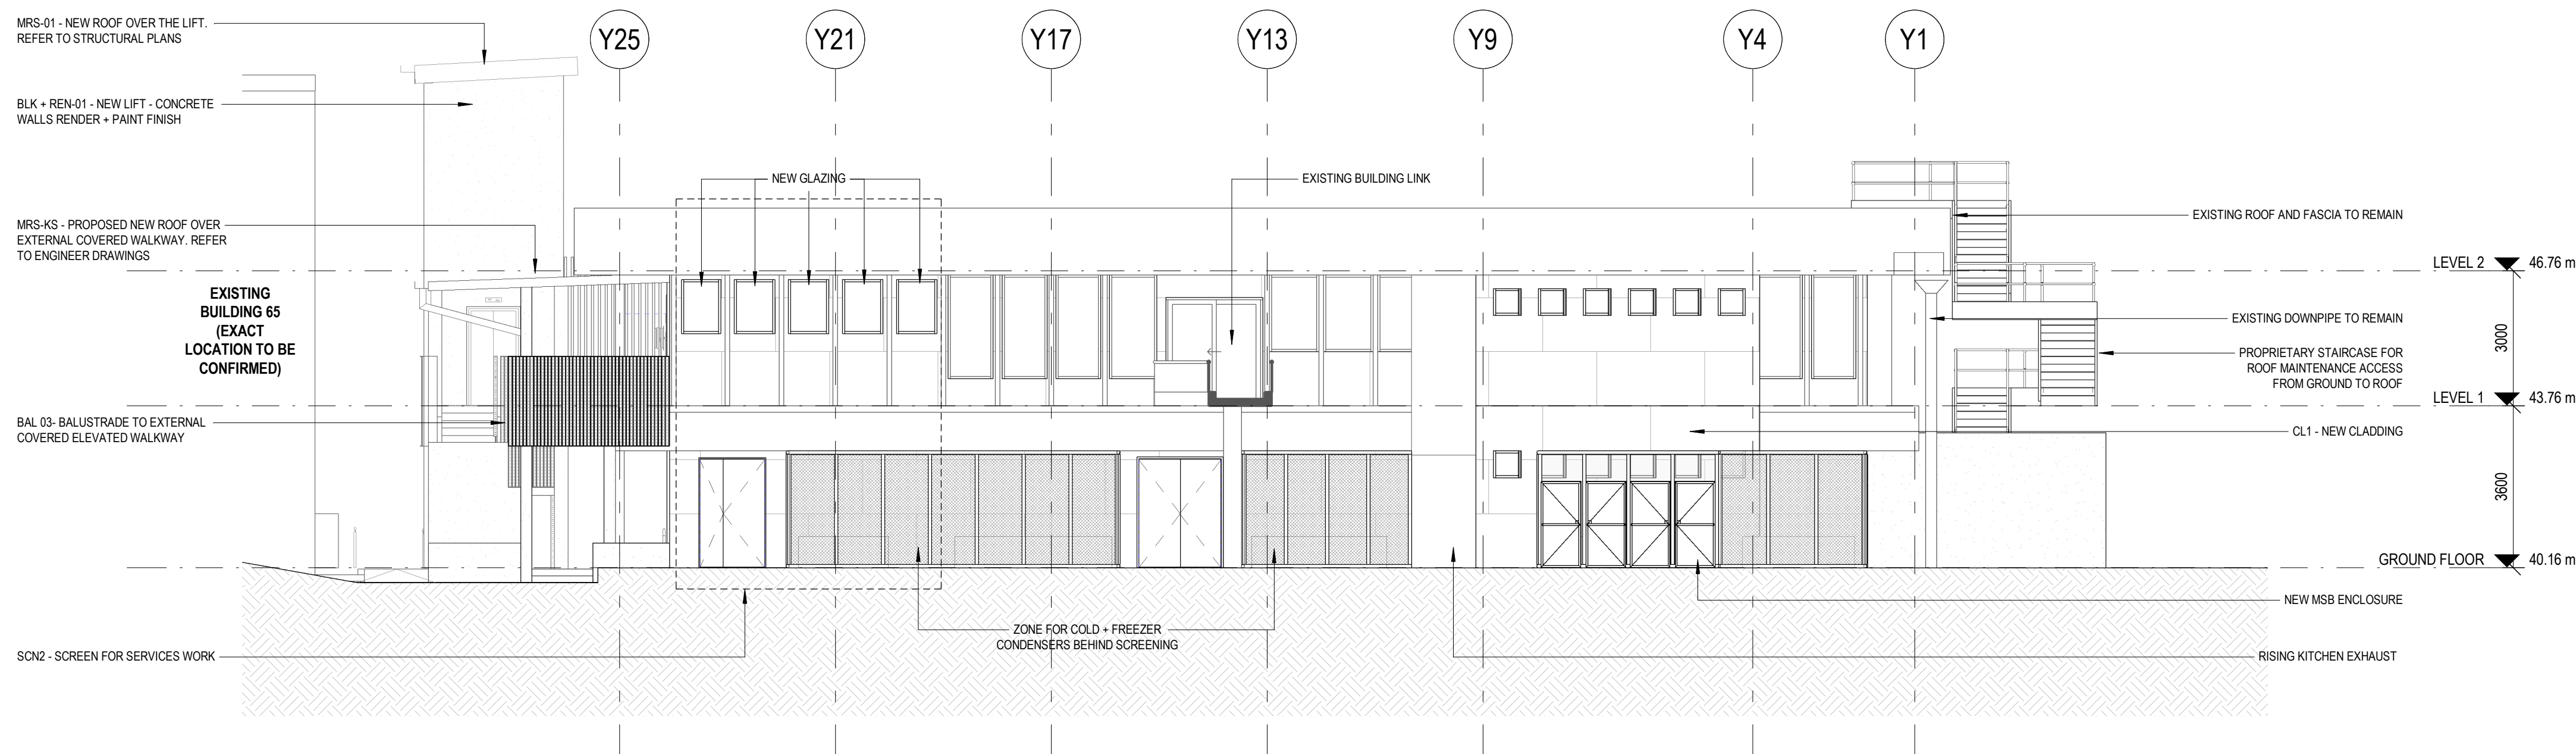
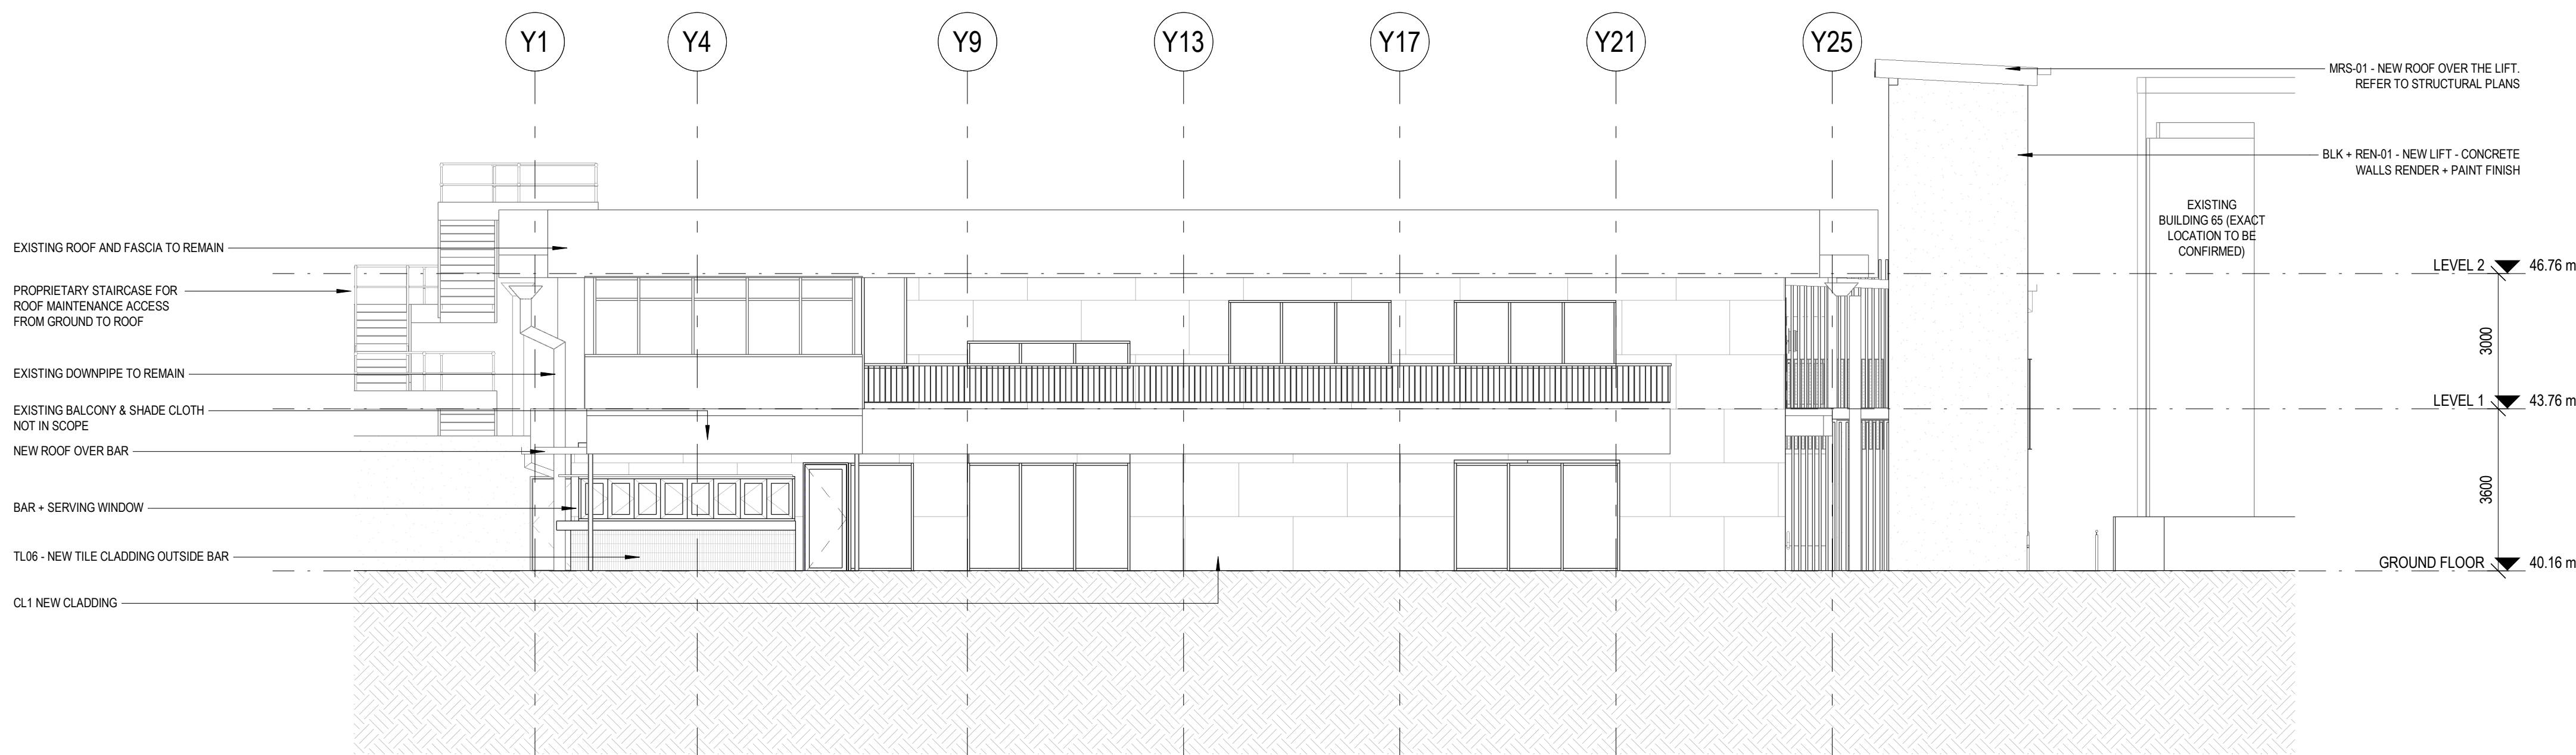


**CQU ROCKHAMPTON
TAFE
CONSOLIDATION -
STAGE 2**554/700 Yaamba Rd, Norman
Gardens QLD 4701

for


**1 SOUTH ELEVATION - PROPOSED**
21-01 1 : 100**2 NORTH ELEVATION - PROPOSED**
21-01 1 : 100**GENERAL NOTE**

- REFER TO CQU DESIGN GUIDELINES FOR DESIGN AND CONSTRUCTION REQUIREMENTS.
- REFER TO OUTLINE SPECIFICATION & SCHEDULE FOR FINISHES

B	2026-03-05	UPDATED ISSUED FOR TENDER	BC
A	2026-02-12	ISSUED FOR TENDER	BC
2	2026-01-30	60% DRAFT ISSUE	BC
1	2025-12-19	UPDATED ISSUE	BC

rev	date	details	init.
-----	------	---------	-------

drawn	date
JS/BC	19/01/2026
checked	date
SS	12/02/2026
verified	date

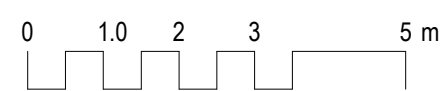scale**BUILDING ELEVATIONS -
PROPOSED**

scale 1 : 100 @ A1 project no. 25.0236.17

revision

B

sheet no.

CQU-ROK-036-00-ARC-30-02