


**CQU ROCKHAMPTON
TAFE
CONSOLIDATION -
STAGE 2**

554/700 Yaamba Rd, Norman
Gardens QLD 4701




B	2026-03-05	UPDATED ISSUED FOR TENDER	BC
A	2026-02-12	ISSUED FOR TENDER	BC
2	2026-01-30	60% DRAFT ISSUE	BC
1	2025-12-19	UPDATED ISSUE	BC
rev	date	details	init.

drawn	date
JS/BC	19/01/2026
checked	date
SS	12/02/2026
verified	date

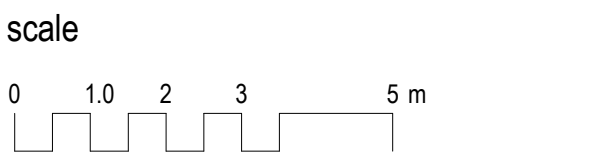


**BUILDING SECTIONS -
PROPOSED**

scale project no.
1 : 100 @ A1 25.0236.17
revision
B
sheet no.
CQU-ROK-036-00-ARC-31-01

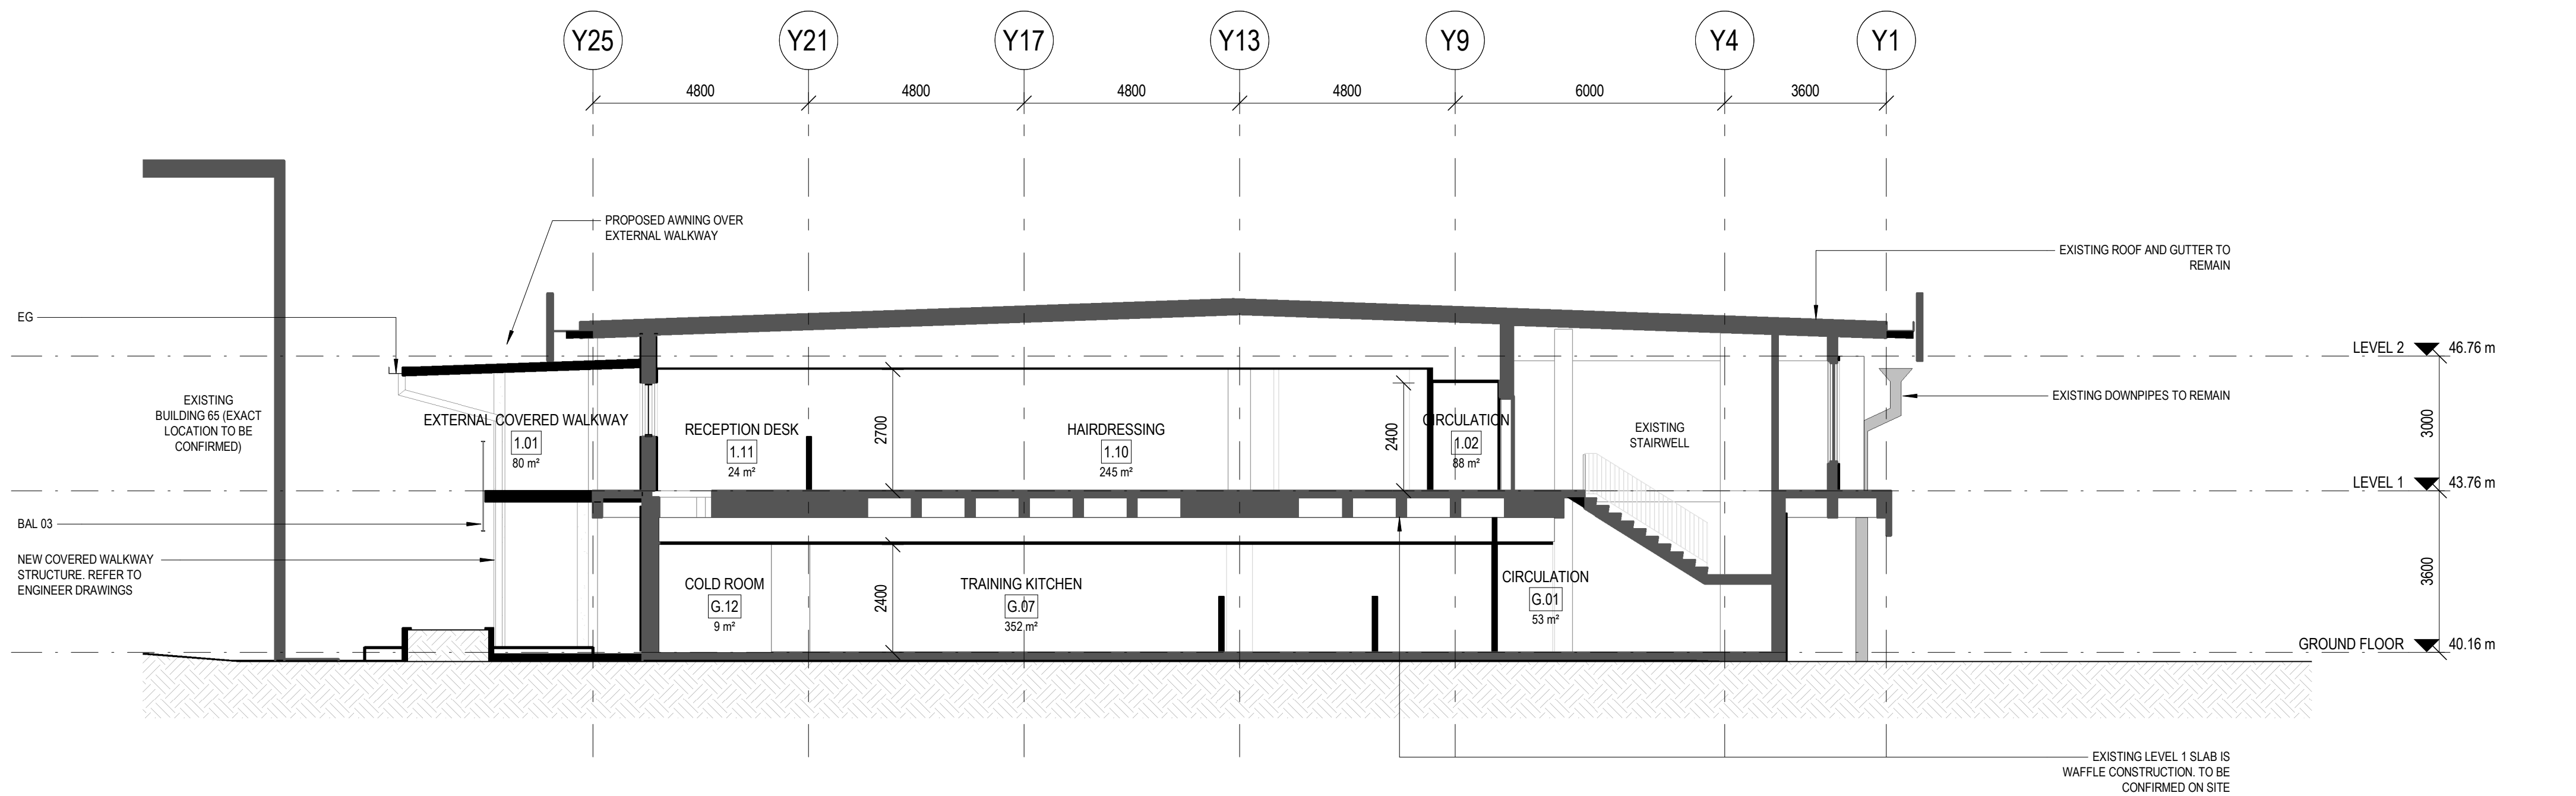

1 SECTION E-W - PROPOSED
1 : 100
21-01

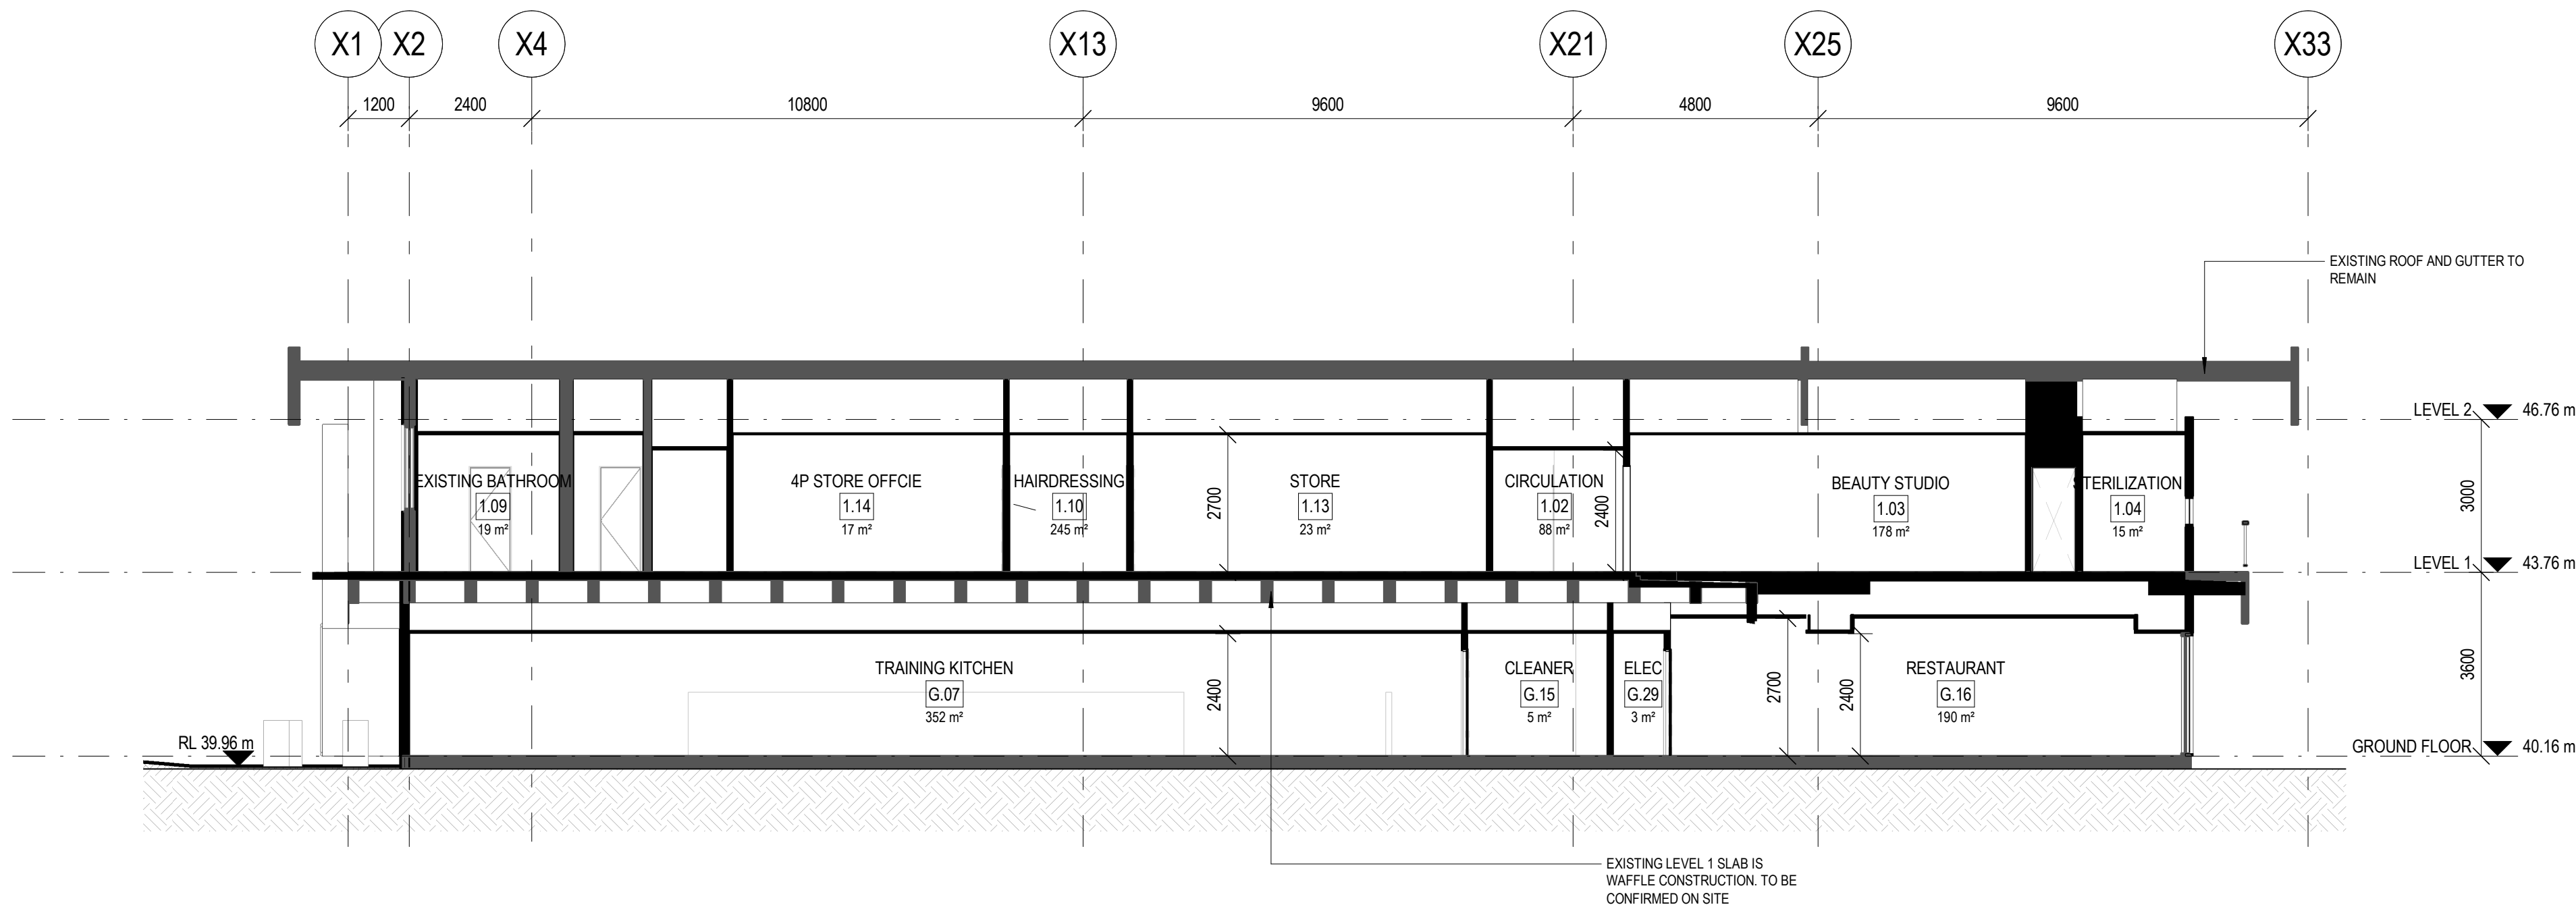

2 SECTION N-S - PROPOSED
1 : 100
21-01

ISSUED FOR TENDER