


CQU ROCKHAMPTON TAFE CONSOLIDATION - STAGE 2


554/700 Yaamba Rd, Norman
Gardens QLD 4701

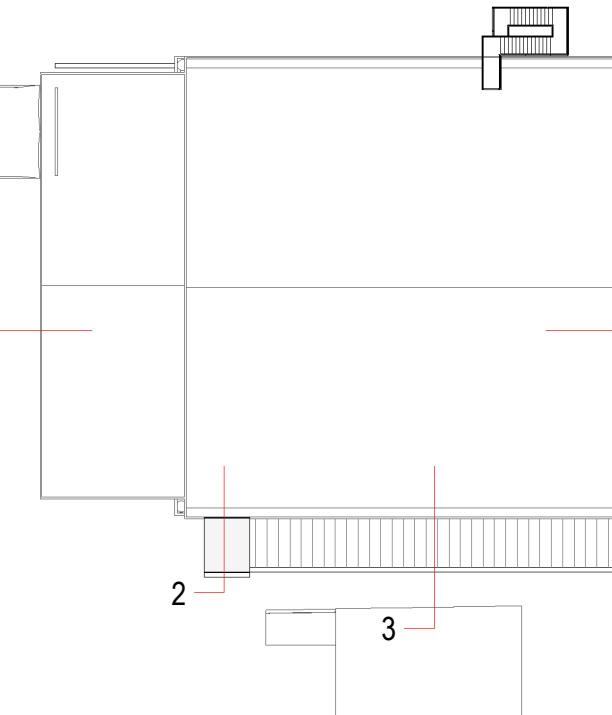

B	2026-03-05	UPDATED ISSUED FOR TENDER	BC
A	2026-02-12	ISSUED FOR TENDER	BC
1	2026-01-30	60% DRAFT ISSUE	BC

rev	date	details	init.
-----	------	---------	-------


drawn	date
JS/BC	19/01/2026
checked	date
SS	12/02/2026
verified	date

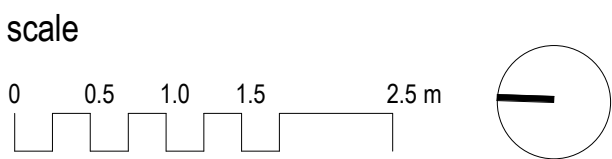


CONSTRUCTION DETAILS

scale project no.
As indicated @ A1 25.0236.17

revision
B
sheet no.
CQU-ROK-036-00-ARC-40-00

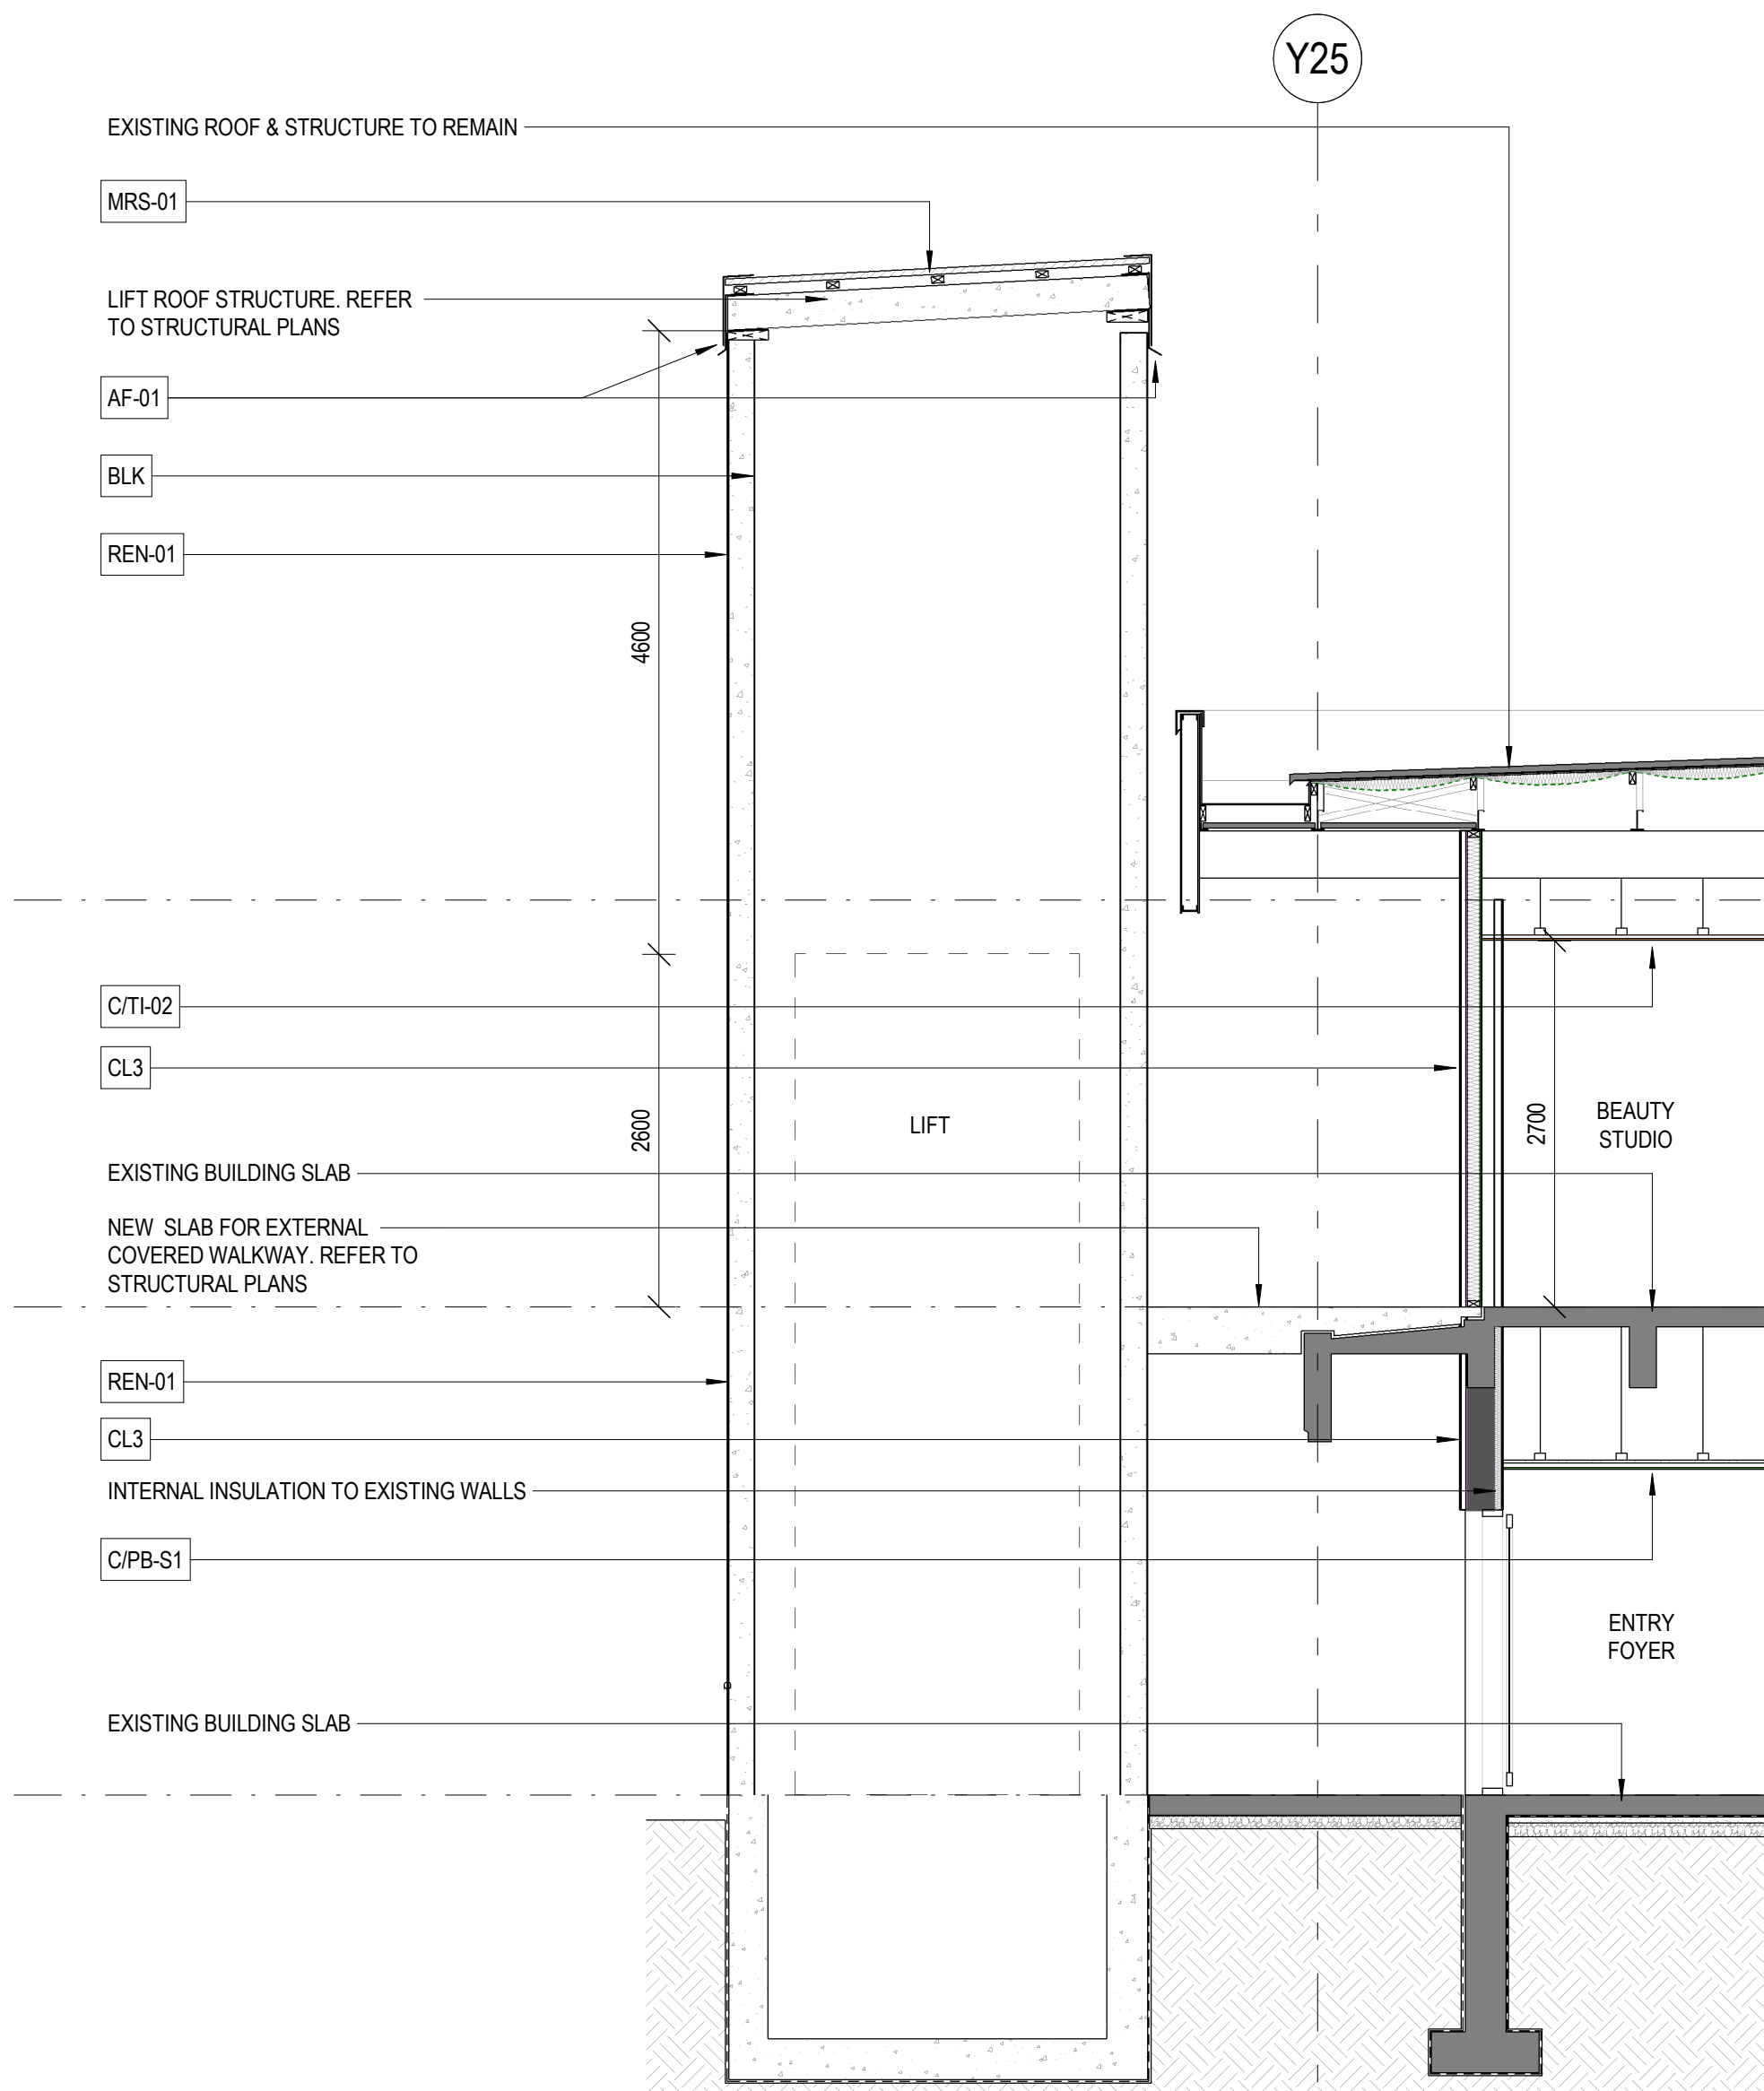

1 WALL SECTION 2
21-01 1 : 50

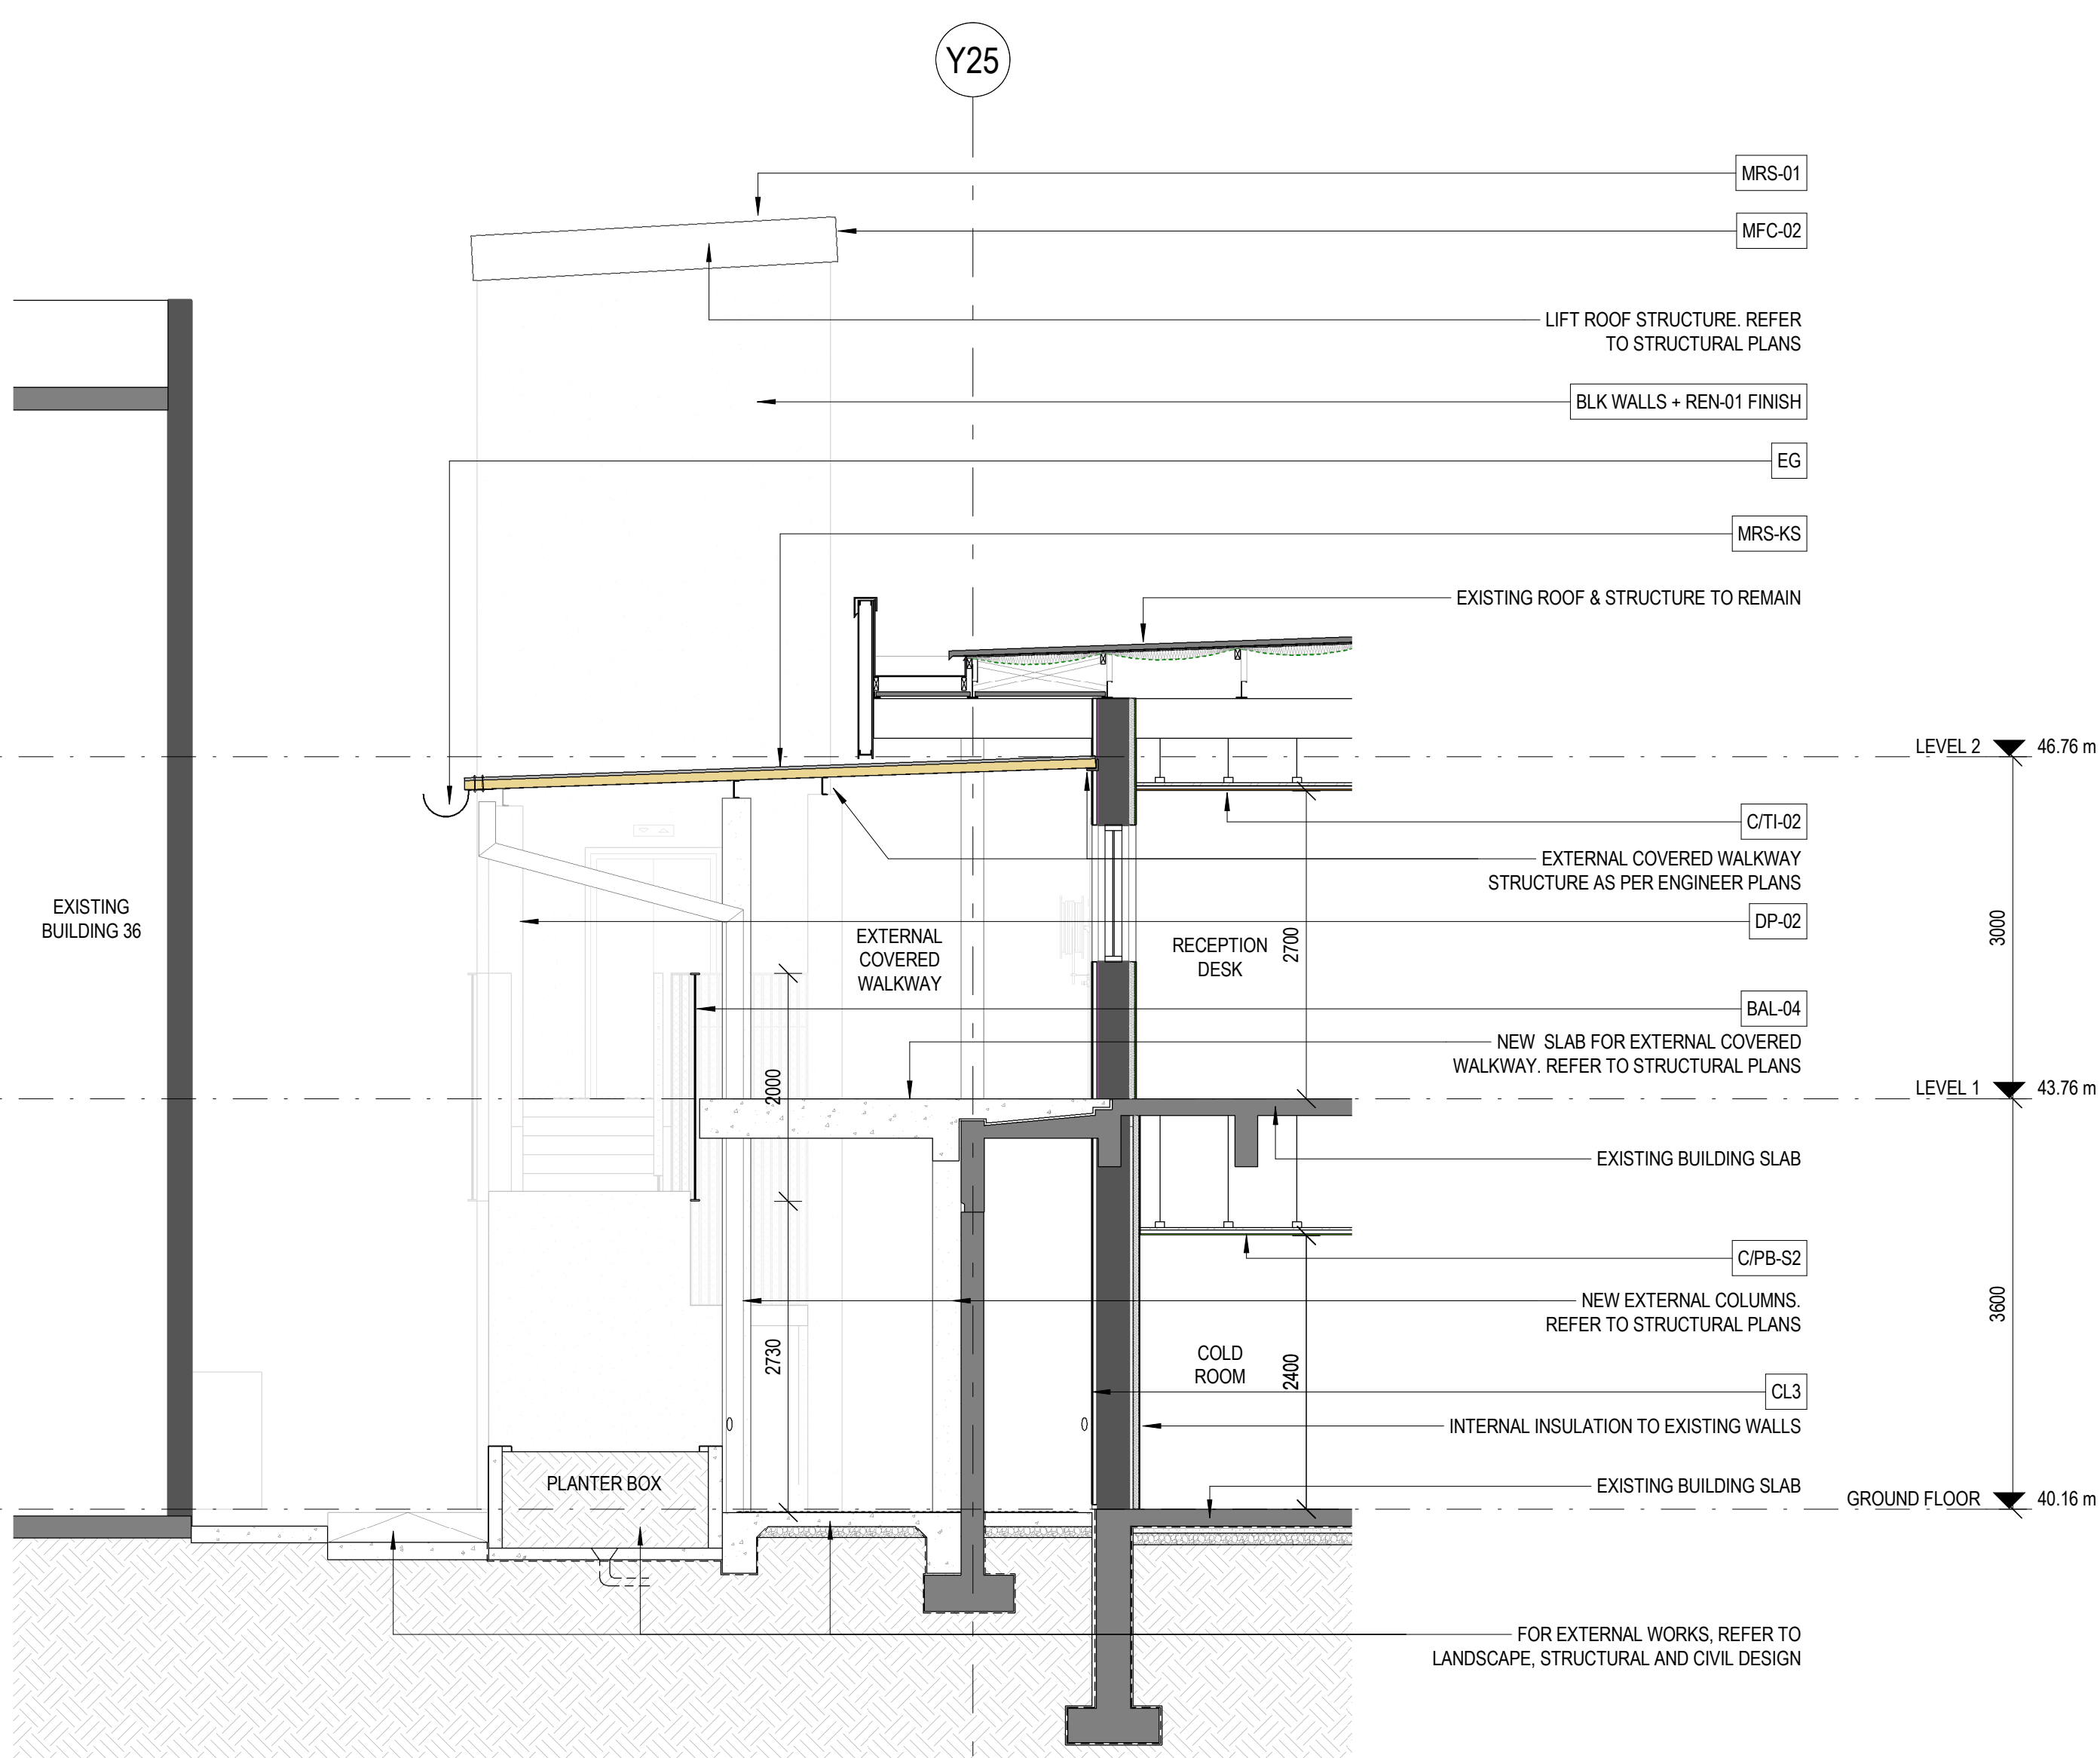

2 WALL SECTION 3
21-01 1 : 50

NOTE

- REFER TO CQU DESIGN GUIDELINES FOR DESIGN AND CONSTRUCTION REQUIREMENTS.
- REFER TO OUTLINE SPECIFICATION & SCHEDULE FOR FINISHES
- CONTRACTOR TO CONFIRM EXISTING STRUCTURE & SERVICES ON SITE PRIOR BUILDING WORK.

ISSUED FOR TENDER