



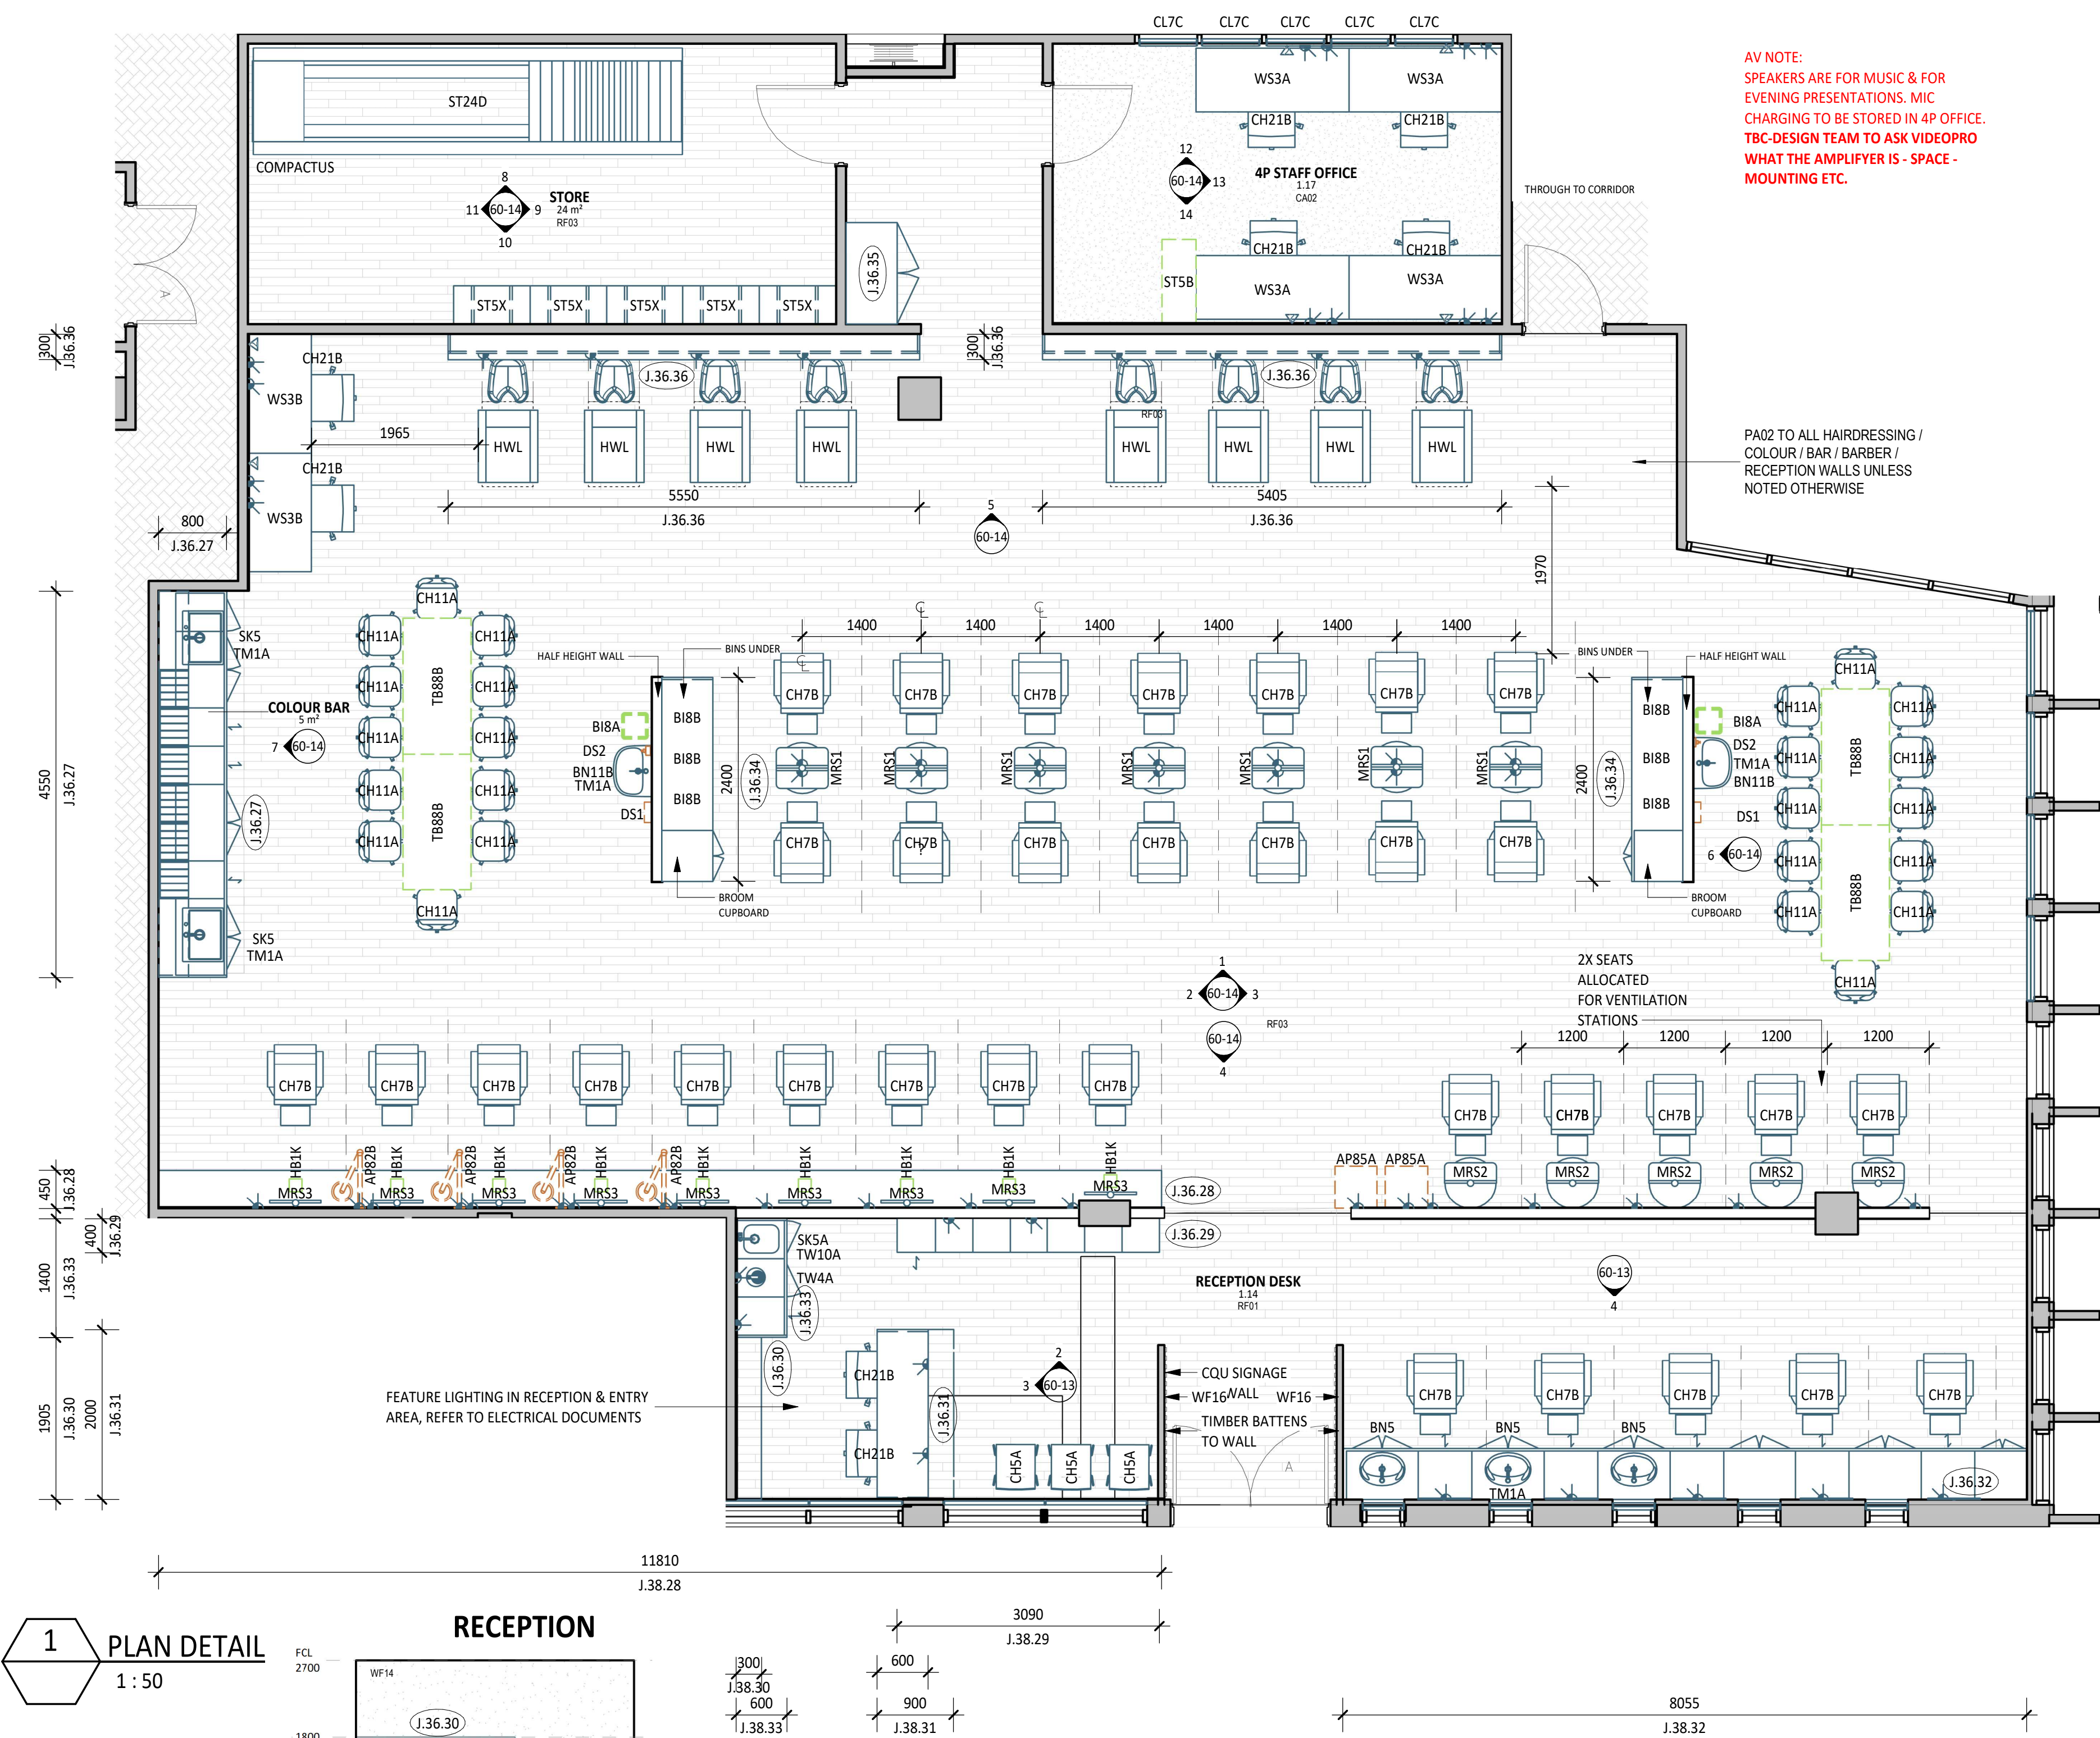


1 PLAN DETAIL
1 : 50

3 ELEVATION DETAIL
1 : 50

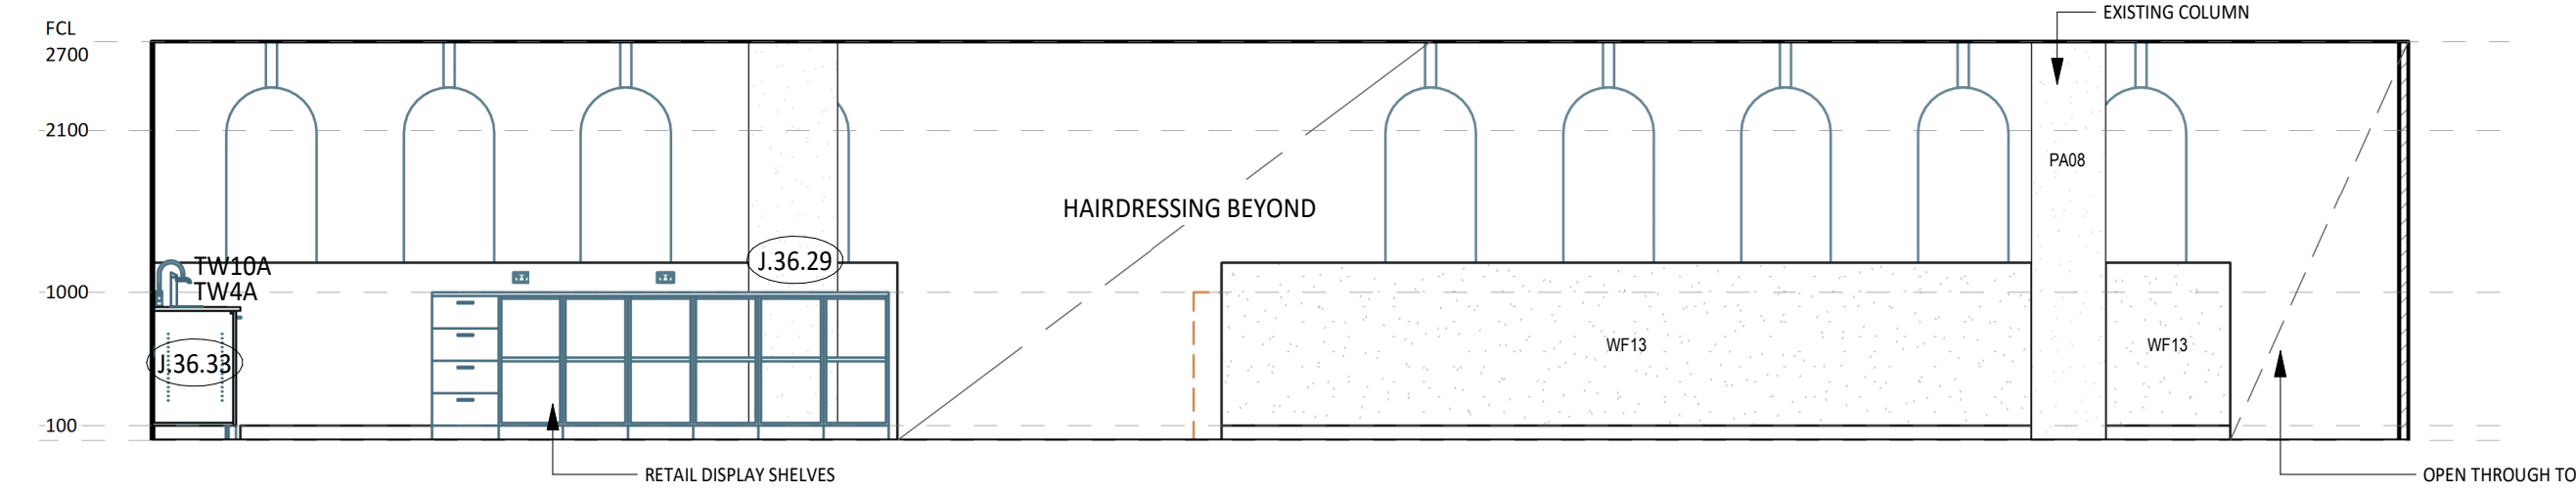

2 ELEVATION DETAIL
1 : 50

BARBER

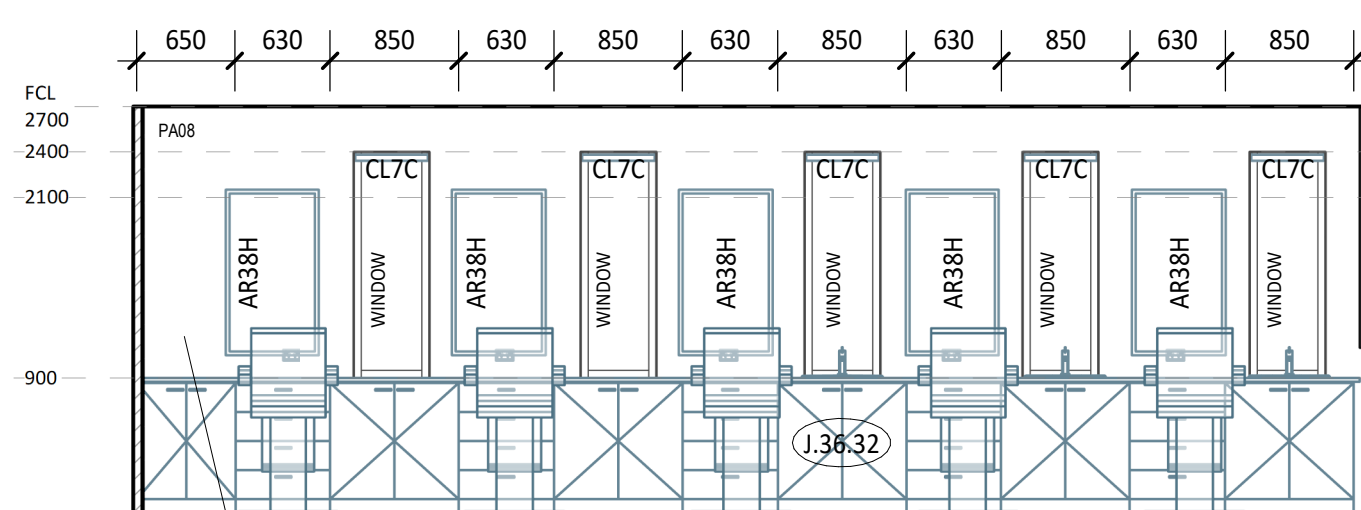

4 ELEVATION DETAIL
1 : 50

40-LEGEND FFE - HAIRDRESSING 1.13				
Code	Description	Group	Count	
BN5	3H - Recessed Oval Basin	1	3	
BN11B	Basin - Type B Basin With Wall Mounted Lever Tapware	1	2	
CH7B	Chair - Specialised Hairdressing	1	34	
CH11A	Chair - Student Stackable	1	24	
CH21B	Chair - Task	1	2	
CL7C	Double Roller Blinds - Blockout	1	9	
HWL	Hair Wash Lounge	1	16	
MRS1	Mirror and Shelf	1	7	
MRS2	Mirror and Shelf	1	6	
MRS3	Mirror and Shelf - ceiling mounted	1	9	
TM1A	Plumbing Fixtures: Tapware - Basin Mixer	1	5	
WS3B	Workstation - 1400W x 750D Straight	1	2	
AP82B	Wall Mounted Hair Dryer	2	4	
AP85A	Mobile Ventilation Station - Hairdressing	2	2	
B18A	Bin - General Waste 20L	3	2	
B18B	Bin - General Waste 50L	3	6	
HB1K	Headblock Clamp	3	9	
TB88B	Angled Table Rectangular On Castors, 1600W x800D x 750H	3	4	
AR38H	Mirror - Framed	1	5	
DS1	Dispenser - Paper Hand Towel	2	2	
DS2	Dispenser - Soap	2	2	

40-LEGEND FFE - RECEPTION DESK 1.14				
Code	Description	Group	Count	
CH5A	Chair - Poly Shell With Timber Base	1	3	
CH21B	Chair - Task	1	2	
CL8A	Single See Through Blind	1	4	
SK5A	Sink - Monaco Single bowl Undermount	1	1	
TW4A	Tapware - Hot and Cold Water Boiling Unit w/ Font, ZIP	1	1	
TW10A	Tapware - Gooseneck Mixer	1	1	

40-LEGEND FFE - STORE 1.16				
Code	Description	Group	Count	
ST24D	Compactus - Mechanical	1	1	

40-LEGEND FFE - 4P STAFF OFFICE B36-L1-13				
hr	Description	Group	Count	
CH21B	Chair - Task	1	4	
CL7C	Double Roller Blinds - Blockout	1	5	
WS3A	Workstation: Office 1800mm (W) x 750mm(D) - Sit/Stand - 50mm Aluminium Frame with Acoustic Panel Insert to Workstation	1	4	
ST5B	Cabinet - Tambour Single Door	3	1	

60-LEGEND JOINERY - BUILDING 36	
Joinery Code	Comments
J.36.27	Benchtop, gables, underbench cupboards, underbench drawers, kickboard, open slot shelvings
J.36.28	Benchtop, bracket support, gables
J.36.29	Benchtop, gables, underbench cupboards, underbench drawers, kickboard
J.36.30	overhead shelving
J.36.31	reception joinery, benchtop, gables, front gables
J.36.32	benchtop, underbench cupboards, underbench drawers, kickboard
J.36.33	benchtop, underbench shelving, underbench cupboards, kickboard, zip tap on top, shelving for tea and coffee
J.36.34	full height cupboard, benchtop, gables
J.36.35	full height cupboards, kickboard bulkhead
J.36.36	overhead shelving

- ### RLS NOTES
- ALL ARCHITECTURAL DRAWINGS TO BE READ IN CONJUNCTION WITH OTHER DISCIPLINES.
 - REFER TO FF&E, SANITARYWARE SCHEDULES FOR ALL FURNITURE, FIXTURES, AND EQUIPMENT.
 - REFER TO HYDRAULIC ENGINEER'S DRAWINGS FOR HYDRAULIC SERVICES. FINISH OF VALVE/BOX COVERS TO MATCH ADJACENT WALL / JOINERY FINISH.
 - REFER TO ELECTRICAL DOCUMENTATION FOR OUTLET DETAILS (ie. POWER, DATA, COMMS etc.)
 - REFER TO AUDIO VISUAL DOCUMENTATION (VideoPro) FOR AV REQUIREMENTS AND DETAILS. ALLOW FOR THE REQUIRED POWER + DATA FOR AV EQUIPMENT.
 - AV SUPPLIER TO CONFIRM EXACT POSITIONS OF EQUIPMENT ON SITE
 - ALL FF&E ITEMS ARE TO BE READ IN CONJUNCTION WITH FF&E SCHEDULES AND CQU DESIGN MANUAL.
 - ALL FF&E AND TRANSFER ITEMS TO BE REVIEWED + CONFIRMED WITH CLIENT PRIOR TO COMMENCING ON SITE.
 - PROVIDE ALLOWANCE AND ADD SUPPORT TO WALLS, WHERE FITTINGS ARE WALL MOUNTED, THIS INCLUDES BUT NOT LIMITED TO HANDBASINS, HANDRAILS, SCREENS, PROJECTORS, etc.
 - FF&E COUNT IS FOR INFORMATION ONLY. THE TOTAL NUMBER OF FF&E ITEMS ARE TO BE CONFIRMED WITH CLIENT AND ARCHITECTS BEFORE PURCHASE OF ITEMS.
 - CONFIRM ALL DIMENSIONS ON SITE FOR JOINERY ITEMS.
 - ALL SANITARY FIXINGS + FIXTURES IN PWD TOILETS TO BE INSTALLED IN ACCORDANCE WITH AS1428.1
 - ALLOW FOR FIRE EXTINGUISHERS + FIRE BLANKETS AS PER AS2444.2001
 - POWER AND DATA POINTS SHOWN ON THE ROOM LAYOUT SHEETS WERE SHOWN AND DISCUSSED DURING USER GROUP BRIEFING. THESE RELATE TO PARTICULAR EQUIPMENT THAT WAS DISCUSSED AS REQUIRING POWER AND DATA. THESE REFLECT STAKEHOLDER EXPECTATIONS FOR SPECIFIC POWER AND DATA POINTS AND HAVE REMAINED IN THE DOCUMENTATION AS A USEFUL REFERENCE FOR THE CONTRACTOR. THESE ARE NOT A COMPLETE QUANTITY AND SPECIFICATION OF POWER AND DATA. THE CONTRACTOR IS TO REFER TO ELECTRICAL ENGINEER'S DOCUMENTATION FOR ALLOWANCE. REFER TO ELECTRICAL DOCUMENTATION FOR AMPS AND 3 PHASE POWER REQUIREMENTS. REFER TO AUDIO VISUAL (VIDEOPRO) DOCUMENTATION FOR ADDITIONAL POWER AND DATA REQUIREMENTS.
 - ALLOW FOR STRUCTURAL PLY BACKING BEHIND PLASTERBOARD FOR FULL EXTENT OF WALLS WITH MOUNTED AUDIO VISUAL EQUIPMENT. REFER TO AUDIO VISUAL (VIDEOPRO) DOCUMENTATION FOR LOCATIONS OF WALL MOUNTED EQUIPMENT.
 - HEARING AUGMENTATION TO AUSTRALIAN STANDARDS - REFER VIDEOPRO AND ELECTRICAL SPECIFICATION.
 - POWER OUTLETS' TYPE / ISOLATORS TO BE CONFIRMED KITCHEN EQUIPMENT REQUIREMENT TO BE CONFIRMED (ALL ELEC OR MIX OF ELEC AND GAS)

ELECTRICAL LEGEND	
⚡ SINGLE POWER OUTLET	🔌 LIGHT SWITCH
⚡ DOUBLE POWER OUTLET	📺 TV
△ SINGLE DATA	
△ DOUBLE DATA	
REFER TO ELECTRICAL ENGINEER'S DRAWINGS FOR DETAILS	

FF&E LEGEND	
— GROUP 1 ITEMS (PROVIDED & FITTED UNDER CONTRACT)	
- - - GROUP 2 ITEMS (PROVIDED BY CLIENT & FITTED UNDER CONTRACT)	
GROUP 2T ITEMS - EXISTING EQUIPMENT (PROVIDED BY CLIENT & FITTED UNDER CONTRACT)	
- - - GROUP 3 ITEMS (PROVIDED & INSTALLED BY CLIENT)	
PLANS TO BE PRINTED IN COLOUR	
SCH_Code	FF&E TAG
JO.PROC	JOINERY TAG

thomson adsett

PEDDLE THORP
architecture | interiors | health | planning

Telephone +61 7 3840 9999
bne@thomsonadsett.com
Level 9, 470 St Pauls Terrace
Fortitude Valley
Qld 4006 Australia
thomsonadsett.com

© Copyright
These drawings and designs and the copyright thereof are the property of Thomson Adsett Pty Ltd and must not be used, retained or copied without written permission of Thomson Adsett Pty Ltd. AEN 76 105 314 654 Trading as ThomsonAdsett. Dimensions take precedence over scaling. Do not measure off drawings as print sizes may vary

CQU ROCKHAMPTON TAFE CONSOLIDATION - STAGE 2

554/700 Yaamba Rd, Norman Gardens QLD 4701



A	12/02/26	ISSUED FOR TENDER	JT
2	30/01/26	60% DRAFT ISSUE	JT
1	23/01/26	FOR COORDINATION ISSUE	JT
rev	date	details	init.

drawn	date
TA/PT	19/12/25
checked	date
JT/RJ	19/12/25
verified	date
JT/RJ	19/12/25

scale

RLS - BLD36-L1 - HAIRDRESSING GENERAL PLAN

scale 1 : 50 @ A1 project no. 260018
revision A
sheet no. CQU-ROK-036-01-ARC-60-13

ISSUE FOR TENDER