



NOTE: WALL LIGHTING, REFER TO ELECTRICAL DOCUMENTS

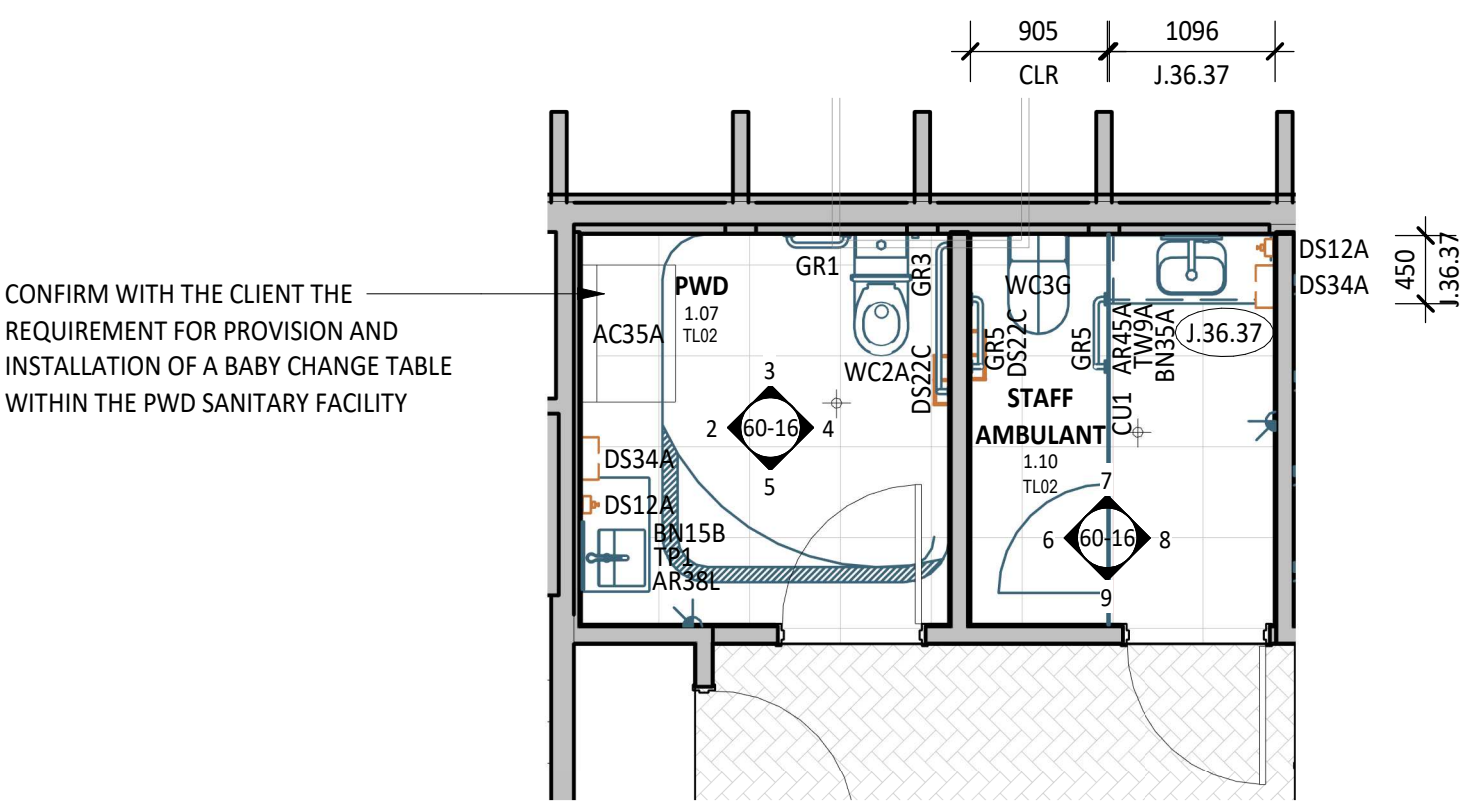


1 PLAN DETAIL
1 : 50


PWD

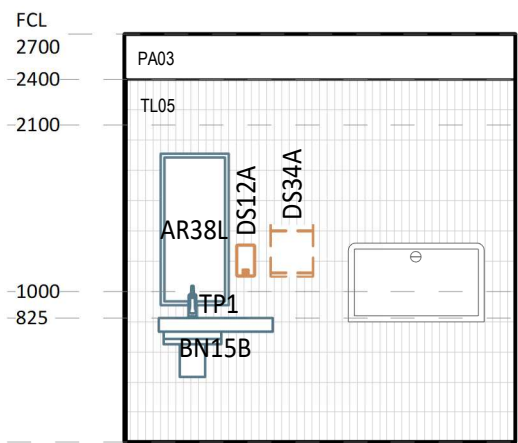


2 ELEVATION DETAIL
1 : 50

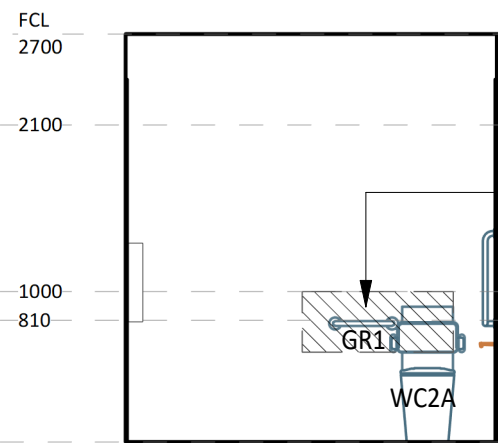

3 ELEVATION DETAIL
1 : 50

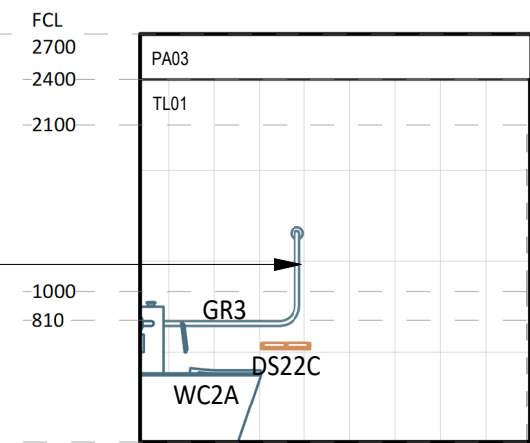


4 ELEVATION DETAIL
1 : 50

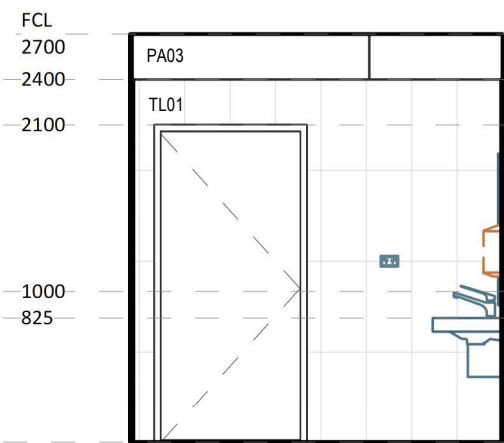


5 ELEVATION DETAIL
1 : 50


STAFF AMBULANT

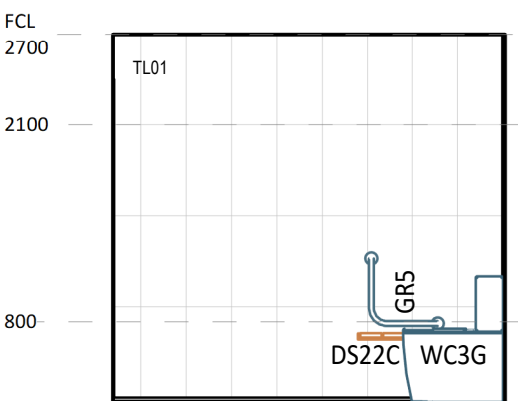


6 ELEVATION DETAIL
1 : 50

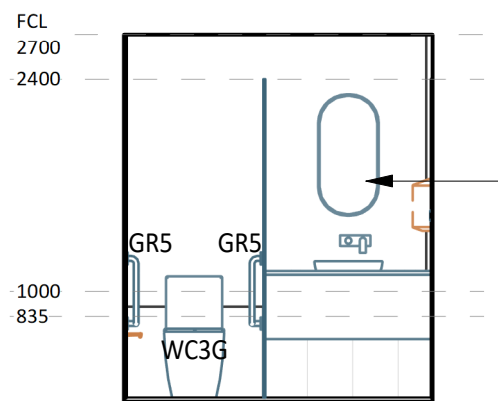

7 ELEVATION DETAIL
1 : 50

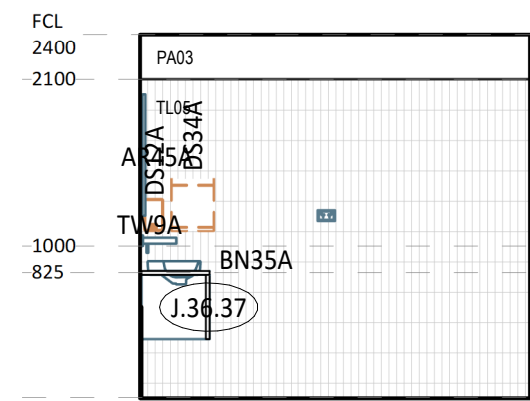

8 ELEVATION DETAIL
1 : 50

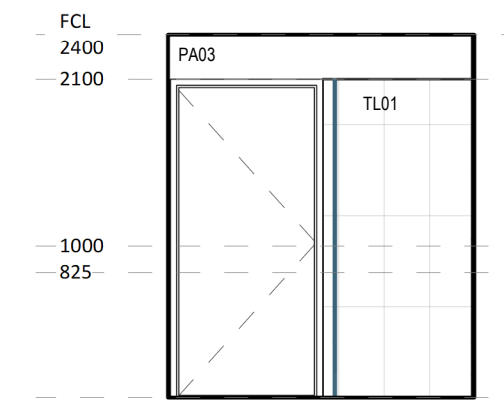

9 ELEVATION DETAIL
1 : 50

40-LEGEND FFE - PWD 1.07			
Code	Description	Group	Count
	PWD Backrest	1	1
BN15B	Accessible Basin	1	1
GR1	Horizontal Grabrail	1	1
TP1	Mixer - Sink Accessible	1	1
WC2A	Toilet - Accessible PWD With Grab Rails	1	1
DS22C	Dispenser - Toilet Tissue 2 Roll	2	1
AR38L	Mirror - Framed	1	1
DS12A	Dispenser - Soap	2	1
DS34A	Dispenser - Paper Hand Towel	2	1

40-LEGEND FFE - AMBULANT 1.10			
Code	Description	Group	Count
AR45A	Mirror - Oval	1	1
BN35A	Caroma Luna Inset Basin	1	1
CU1	Cubicles - Toilet Partition	1	1
GR5	40D - Grab Rail 90 Degree	1	2
TW9A	Tapware - Wall Mounted Basin Mixer	1	1
WC3G	Toilets - Concealed Unit	1	1
DS22C	Dispenser - Toilet Tissue 2 Roll	2	1
DS34A	Dispenser - Paper Hand Towel	2	1

60-LEGEND JOINERY - BUILDING 36	
Joinery Code	Comments
J.36.25	Benchtop, gables, underbench cupboards, kickboard
J.36.37	Benchtop, front panel, with integrated basin

RLS NOTES

1. ALL ARCHITECTURAL DRAWINGS TO BE READ IN CONJUNCTION WITH OTHER DISCIPLINES.
2. REFER TO FF&E, SANITARYWARE SCHEDULES FOR ALL FURNITURE, FIXTURES, AND EQUIPMENT.
3. REFER TO HYDRAULIC ENGINEER'S DRAWINGS FOR HYDRAULIC SERVICES. FINISH OF VALVE/BOX COVERS TO MATCH ADJACENT WALL / JOINERY FINISH.
4. REFER TO ELECTRICAL DOCUMENTATION FOR OUTLET DETAILS (ie. POWER, DATA, COMMS etc.)
5. REFER TO AUDIO VISUAL DOCUMENTATION (VideoPro) FOR AV REQUIREMENTS AND DETAILS. ALLOW FOR THE REQUIRED POWER + DATA FOR AV EQUIPMENT.
6. AV SUPPLIER TO CONFIRM EXACT POSITIONS OF EQUIPMENT ON SITE
7. ALL FF&E ITEMS ARE TO BE READ IN CONJUNCTION WITH FF&E SCHEDULES AND CQU DESIGN MANUAL.
8. ALL FF&E AND TRANSFER ITEMS TO BE REVIEWED + CONFIRMED WITH CLIENT PRIOR TO COMMENCING ON SITE.
9. PROVIDE ALLOWANCE AND ADD SUPPORT TO WALLS, WHERE FITTINGS ARE WALL MOUNTED. THIS INCLUDES BUT NOT LIMITED TO HANDBASINS, HANDRAILS, SCREENS, PROJECTORS, etc.
10. FF&E COUNT IS FOR INFORMATION ONLY. THE TOTAL NUMBER OF FF&E ITEMS ARE TO BE CONFIRMED WITH CLIENT AND ARCHITECTS BEFORE PURCHASE OF ITEMS.
11. CONFIRM ALL DIMENSIONS ON SITE FOR JOINERY ITEMS.
12. ALL SANITARY FIXINGS + FIXTURES IN PWD TOILETS TO BE INSTALLED IN ACCORDANCE WITH AS1428.1
13. ALLOW FOR FIRE EXTINGUISHERS + FIRE BLANKETS AS PER AS2444.2001
14. POWER AND DATA POINTS SHOWN ON THE ROOM LAYOUT SHEETS WERE SHOWN AND DISCUSSED DURING USER GROUP BRIEFING. THESE RELATE TO PARTICULAR EQUIPMENT THAT WAS DISCUSSED AS REQUIRING POWER AND DATA. THESE REFLECT STAKEHOLDER EXPECTATIONS FOR SPECIFIC POWER AND DATA POINTS AND HAVE REMAINED IN THE DOCUMENTATION AS A USEFUL REFERENCE FOR THE CONTRACTOR. THESE ARE NOT A COMPLETE QUANTITY AND SPECIFICATION OF POWER AND DATA. THE CONTRACTOR IS TO REFER TO ELECTRICAL ENGINEER'S DOCUMENTATION FOR ALLOWANCE. REFER TO ELECTRICAL DOCUMENTATION FOR AMPS AND 3 PHASE POWER REQUIREMENTS. REFER TO AUDIO VISUAL (VIDEOPRO) DOCUMENTATION FOR ADDITIONAL POWER AND DATA REQUIREMENTS.
15. ALLOW FOR STRUCTURAL PLY BACKING BEHIND PLASTERBOARD FOR FULL EXTENT OF WALLS WITH MOUNTED AUDIO VISUAL EQUIPMENT. REFER TO AUDIO VISUAL (VIDEOPRO) DOCUMENTATION FOR LOCATIONS OF WALL MOUNTED EQUIPMENT.
16. HEARING AUGMENTATION TO AUSTRALIAN STANDARDS – REFER VIDEOPRO AND ELECTRICAL SPECIFICATION.
17. POWER OUTLETS' TYPE / ISOLATORS TO BE CONFIRMED (ALL KITCHEN EQUIPMENT REQUIREMENT TO BE CONFIRMED (ALL ELEC OR MIX OF ELEC AND GAS))

ELECTRICAL LEGEND

- SINGLE POWER OUTLET
- DOUBLE POWER OUTLET
- SINGLE DATA
- DOUBLE DATA
- REFER TO ELECTRICAL ENGINEER'S DRAWINGS FOR DETAILS
- LIGHT SWITCH
- TV

FF&E LEGEND

- GROUP 1 ITEMS (PROVIDED & FITTED UNDER CONTRACT)
- GROUP 2 ITEMS (PROVIDED BY CLIENT & FITTED UNDER CONTRACT)
- GROUP 2T ITEMS - EXISTING EQUIPMENT (PROVIDED BY CLIENT & FITTED UNDER CONTRACT)
- GROUP 3 ITEMS (PROVIDED & INSTALLED BY CLIENT)
- PLANS TO BE PRINTED IN COLOUR
- SCH_Code FF&E TAG
- JO.PROC JOINERY TAG

AMENITIES NOTES

- SETOUT MARKER
- NOTE: ALL SANITARY FITTINGS AND FIXTURES IN PWD WC INSTALLED IN ACCORDANCE WITH AUSTRALIAN STANDARD AS1428.1
- NOTE: REFER TO SCHEDULES FOR ALL SANITARY FIXTURES AND FITTINGS.
- PROVIDE NOGGINGS IN PARTITION WALLS TO SUPPORT SANITARY FIXTURES AND FITTINGS; INCLUDING IN-WALL CISTERNS, AS REQUIRED.

ISSUE FOR TENDER

thomson adsett

PEDDLE THORP
architecture | interiors | health | planning

Telephone +61 7 3840 9999
bne@thomsonadsett.com
Level 9, 470 St Pauls Terrace
Fortitude Valley
Qld 4006 Australia
thomsonadsett.com

© Copyright
These drawings and designs and the copyright thereof are the property of Thomson Adsett Pty Ltd and must not be used, retained or copied without written permission of Thomson Adsett Pty Ltd. AEN 76 105 314 654 Trading as ThomsonAdsett. Dimensions take precedence over scaling. Do not measure off drawings as print sizes may vary

CQU ROCKHAMPTON
TAFE
CONSOLIDATION -
STAGE 2

554/700 Yaamba Rd, Norman
Gardens QLD 4701

for

CQUniversity
AUSTRALIA

A	12/02/26	ISSUED FOR TENDER	JT
2	30/01/26	60% DRAFT ISSUE	JT
1	23/01/26	FOR COORDINATION ISSUE	JT

rev	date	details	init.
drawn	date		
TA/PT	01/22/26		
checked	date		
JT/RJ	01/22/26		
verified	date		
JT/RJ	01/22/26		

scale	

RLS - BLD36-L1 - PWD,
AMBULANT

scale 1 : 50 @ A1 project no. 260018

revision A

sheet no. CQU-ROK-036-01-ARC-60-16