



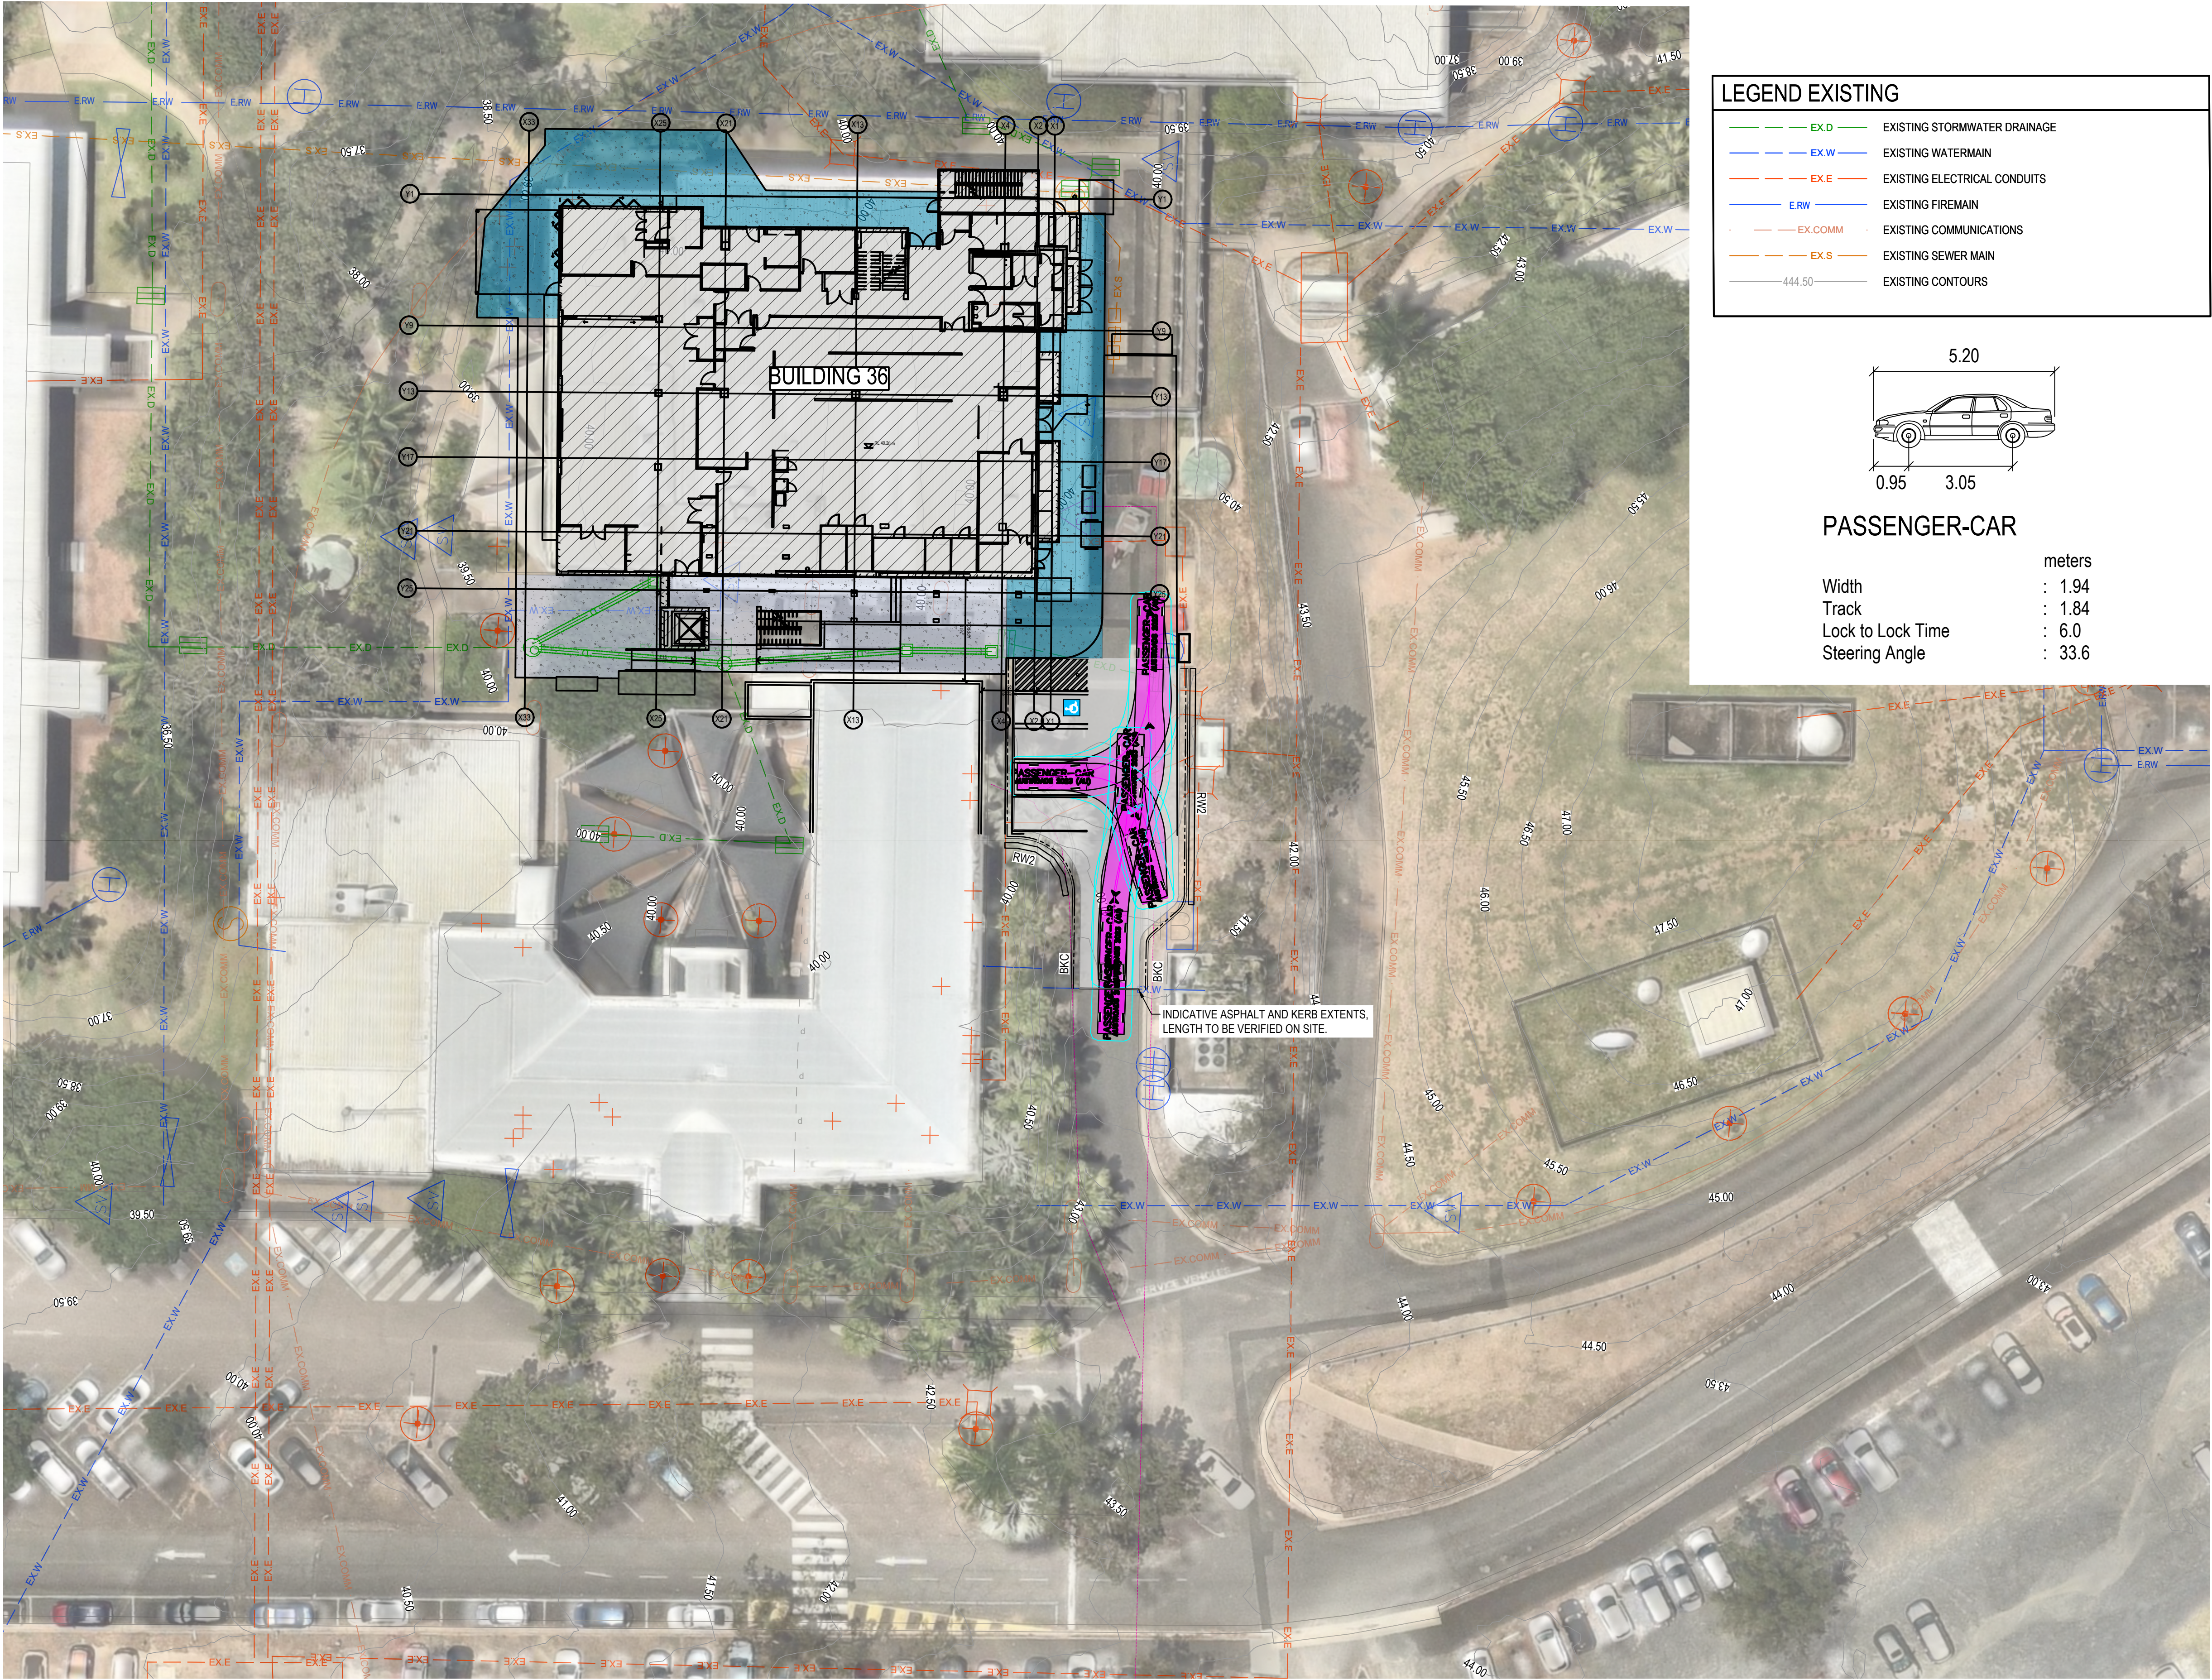

LEGEND EXISTING

- EX.D EXISTING STORMWATER DRAINAGE
- EX.W EXISTING WATERMAIN
- EX.E EXISTING ELECTRICAL CONDUITS
- ER.W EXISTING FIREMAIN
- EX.COMM EXISTING COMMUNICATIONS
- EX.S EXISTING SEWER MAIN
- 444.50 EXISTING CONTOURS

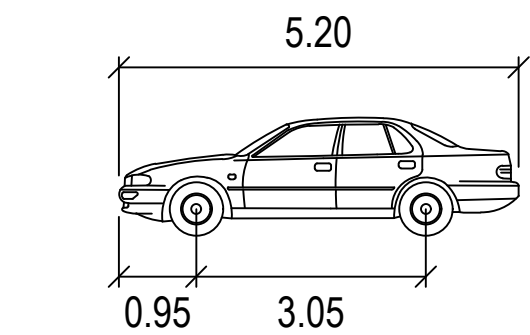


PASSENGER-CAR

Width	: 1.94	meters
Track	: 1.84	
Lock to Lock Time	: 6.0	
Steering Angle	: 33.6	

LEGEND

- PROPOSED BUILDING AREA
- PROPOSED PAVEMENT TYPE 1 LIGHT DUTY ASPHALT - REFER DWG C240
- PROPOSED PAVEMENT TYPE 2 HEAVY DUTY ASPHALT - REFER DWG C240
- PROPOSED PAVEMENT TYPE 3 HEAVY DUTY CONCRETE - REFER DWG C240
- PROPOSED PAVEMENT TYPE 4 LIGHT DUTY CONCRETE - REFER DWG C240
- PROPOSED CHEVRON LINEMARKING TO AS1742.2
- PROPOSED LANDSCAPE AREA REFER LANDSCAPE PLANS FOR DETAILS
- STAGE BOUNDARY
- CONTOURS MAJOR
- PROPOSED TOP OF BATTER
- PROPOSED BOTTOM OF BATTER
- PROPOSED EDGE OF BITUMEN
- BKC PROPOSED BARRIER KERB AND CHANNEL
- MKC PROPOSED BARRIER KERB AND CHANNEL
- INR PROPOSED INVERT KERB
- RW2 PROPOSED BLOCK RETAINING WALL
- PROPOSED GALVANISED TUBULAR FENCE
- PROPOSED SIGN
- B PROPOSED BOLLARD
- PROPOSED TACTILE GROUND SURFACE INDICATORS (TGS)
- PROPOSED WHEEL STOP
- PROPOSED KERB RAMP
- X X X X ITEMS / SERVICES TO BE REMOVED
- + PL00.000 PROPOSED PAVEMENT LEVEL
- + SL00.000 PROPOSED SURFACE LEVEL
- + BE00.000 PROPOSED BULK EARTHWORKS LEVEL
- + TW00.000 PROPOSED TOP OF RETAINING WALL LEVEL
- + BW00.000 PROPOSED BOTTOM OF RETAINING WALL LEVEL
- + EX00.000 EXISTING SURFACE LEVEL
- 1:XX PROPOSED SURFACE FALL
- RWD PROPOSED TRENCH GRATE
- SD PROPOSED ROOFWATER DRAINAGE PIPE
- PROPOSED SUBSOIL DRAINAGE
- PROPOSED STORMWATER DRAINAGE PIPE AND MANHOLE
- PROPOSED HEADWALL AND ROCK OUTLET PROTECTION
- PROPOSED TABLEDRAIN
- W PROPOSED WATER PIPE
- E PROPOSED ELECTRICAL CONDUIT/CABLES
- N1 REFER NOTE 1 FOR DETAILS

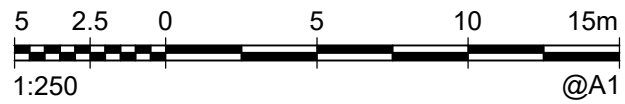

P1	001/2026	RO	PRELIMINARY			
REV	DATE	BY	DESCRIPTION	CHK	APP	
DRAWING STATUS:			PRELIMINARY			



<http://www.wsp.com>

CLIENT:



ARCHITECT:



PROJECT:

CQU ROCKHAMPTON TAFE

TITLE:

BUILDING 36 SITE LAYOUT PLAN

SCALE @ A1:

1:250

CHECKED:

JC

APPROVED:

JC

PROJECT NUMBER:

PS229518

DRAWN:

RO

DATE:

1/23/2026

DRAWING No:

C200

REV:

P1

© WSP Australia Pty Ltd