
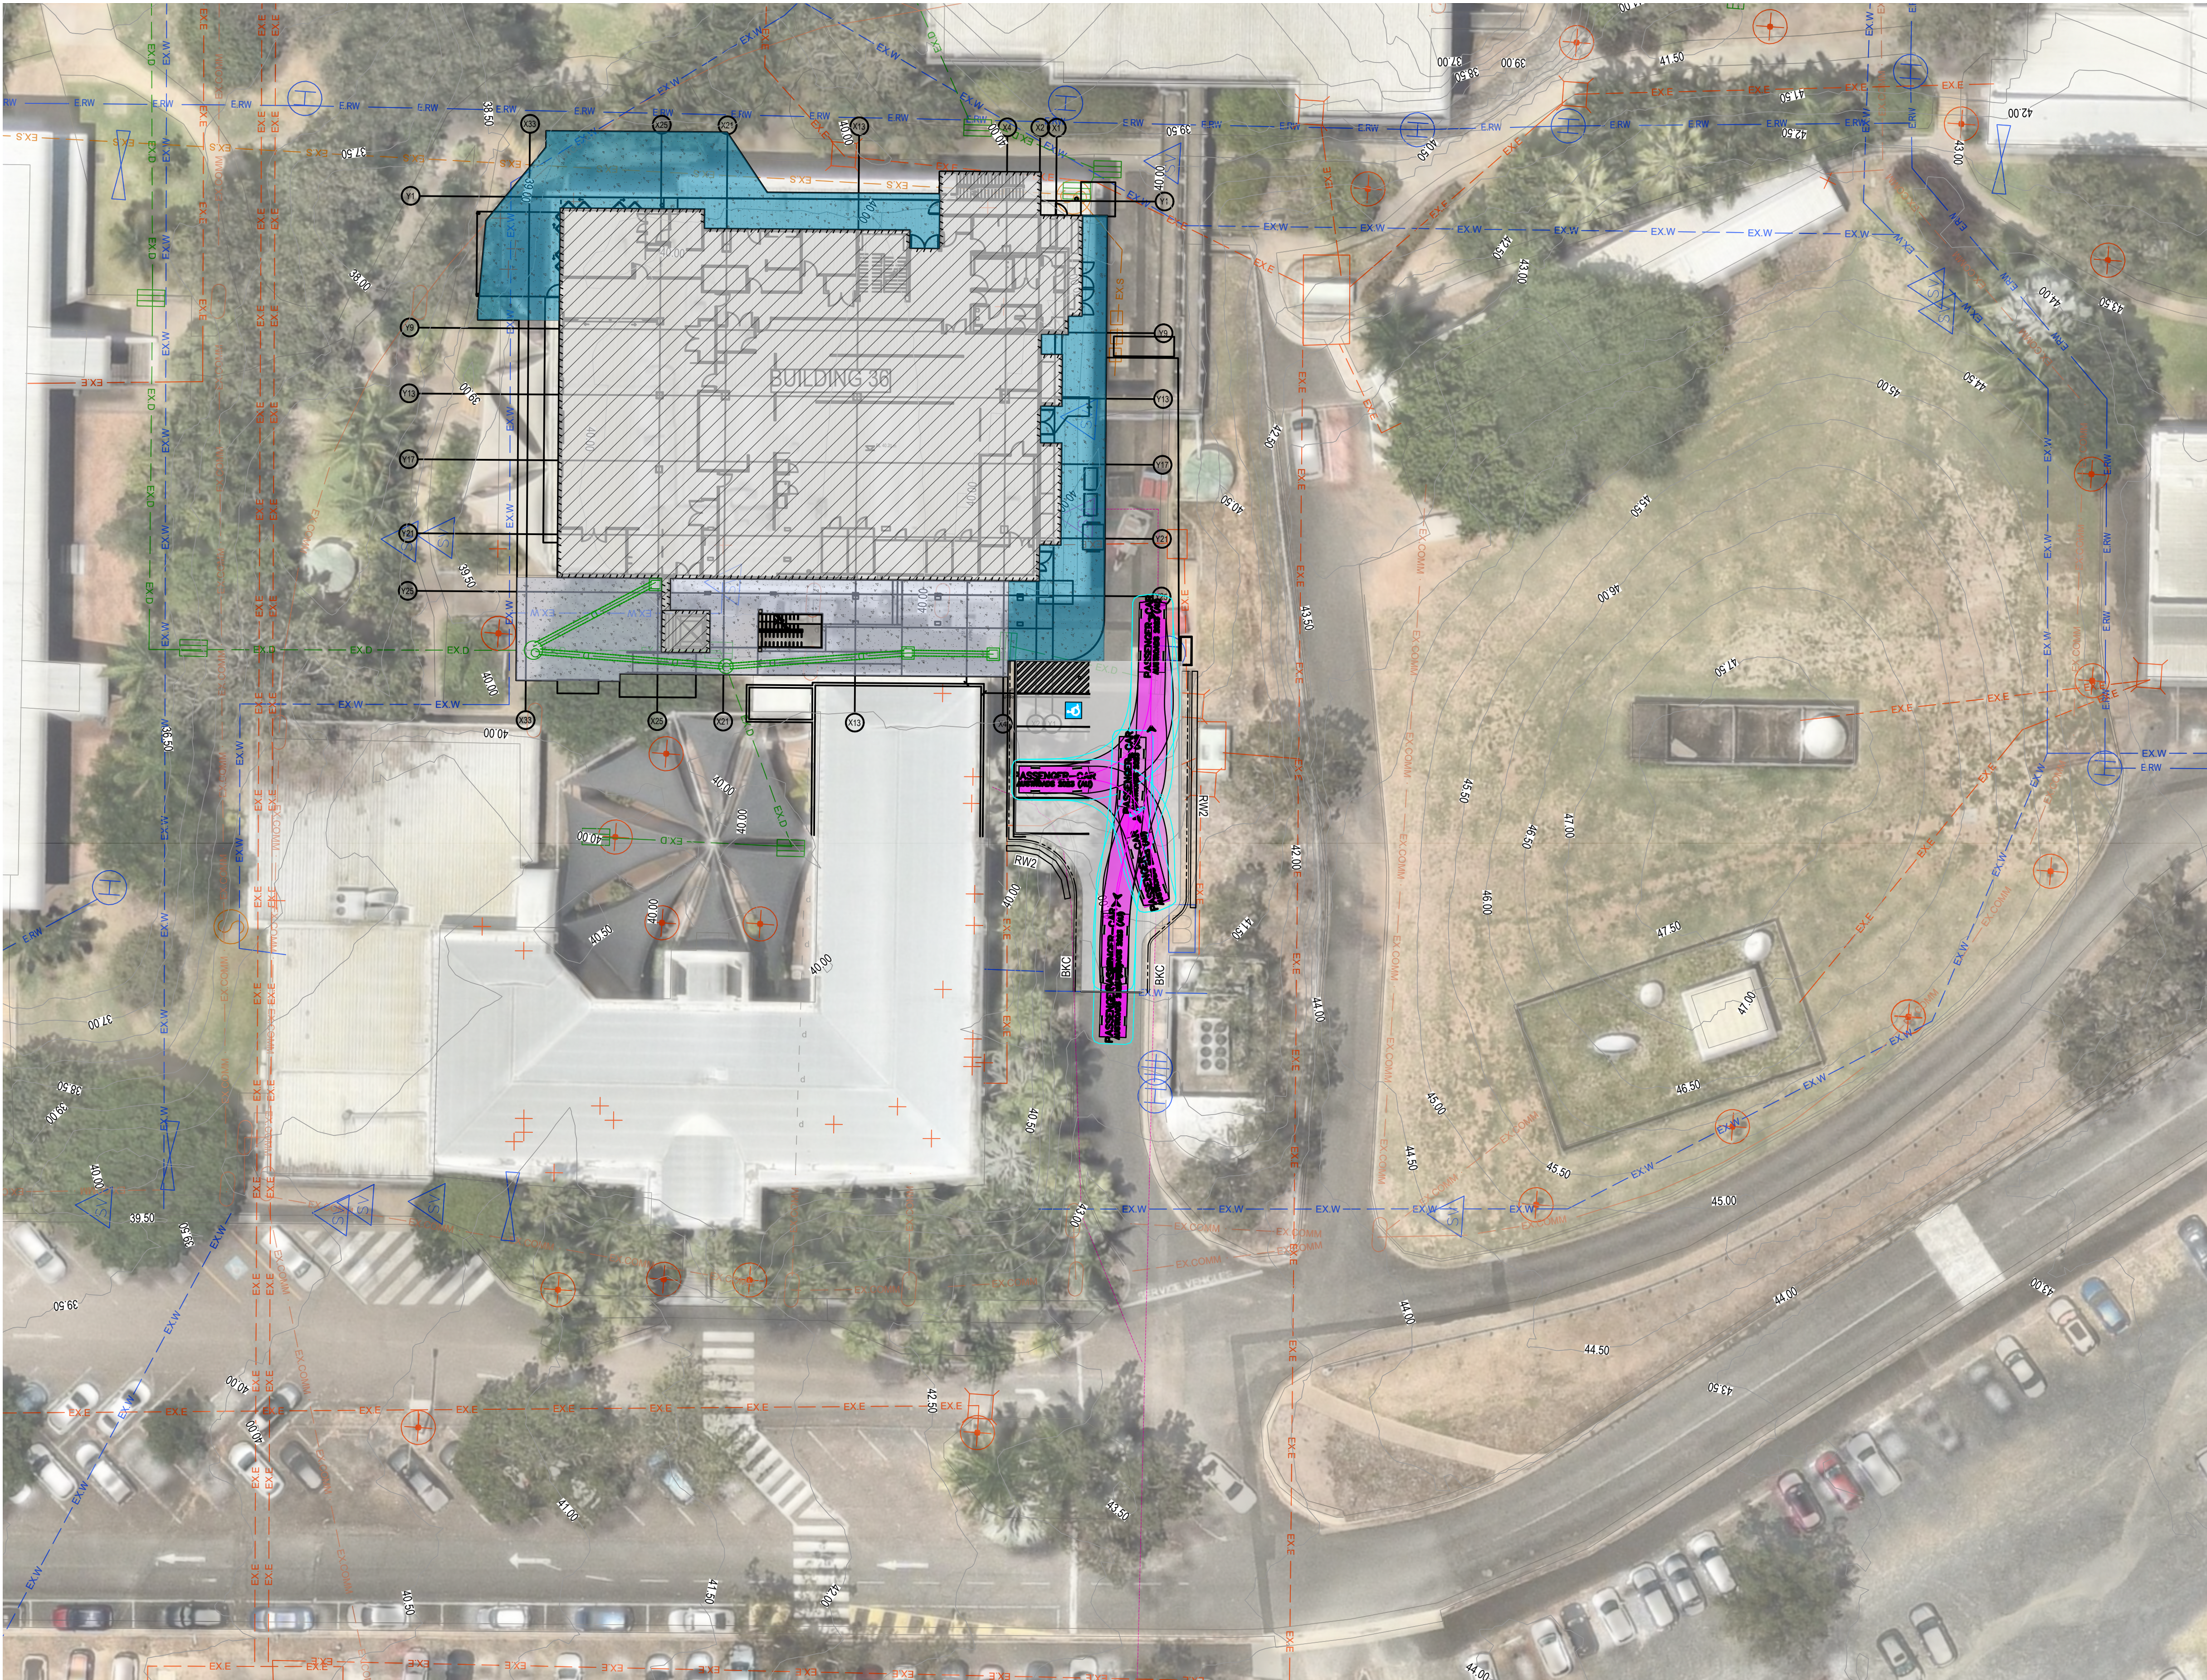


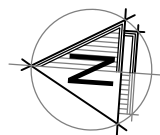


LEGEND EXISTING

- EX.D EXISTING STORMWATER DRAINAGE
- EX.W EXISTING WATERMAIN
- EX.E EXISTING ELECTRICAL CONDUITS
- ER.W EXISTING FIREMAIN
- EX.COMM EXISTING COMMUNICATIONS
- EX.S EXISTING SEWER MAIN
- 444.50 EXISTING CONTOURS

LEGEND

- PROPOSED PAVEMENT TYPE 1
LIGHT DUTY ASPHALT - REFER DWG C240
- PROPOSED PAVEMENT TYPE 2
HEAVY DUTY ASPHALT - REFER DWG C240
- PROPOSED PAVEMENT TYPE 3
HEAVY DUTY CONCRETE - REFER DWG C240
- PROPOSED PAVEMENT TYPE 4
LIGHT DUTY CONCRETE - REFER DWG C240
- LANDSCAPE AREA
REFER LANDSCAPE PLANS FOR DETAILS
- BUILDING AREA
- SC SAW CUT LINE
- SJ SAWCUT JOINT
- EJ EXPANSION JOINT
- IJ ISOLATION JOINT
- CJ CONSTRUCTION JOINT
- ET EDGE THICKENING
- LJ LONGITUDINAL JOINT
- 2-N12 TRIMMER BARS 1500 LONG FIXED TO UNDERSIDE OF MESH
- # ADDITIONAL LAYER OF SL82 MESH (BTM) ON ENTIRE PANEL.
- N1 REFER NOTE 1 FOR DETAILS

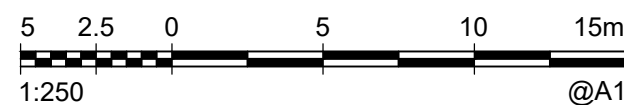

P1	30012026	RO	DRAFT 60% DESIGN DEVELOPMENT	JC	JC
REV	DATE	BY	DESCRIPTION	CHK	APP
DRAWING STATUS:			PRELIMINARY		



<http://www.wsp.com>

CLIENT:



ARCHITECT:



PROJECT:

CQU ROCKHAMPTON TAFE

TITLE:

BUILDING 36 PAVEMENT LAYOUT PLAN

SCALE @ A1:

1:250

CHECKED:

JC

APPROVED:

JC

PROJECT NUMBER:

PS229518

DRAWN:

RO

DATE:

1/30/2026

DRAWING No:

C230

REV:

P1

© WSP Australia Pty Ltd