




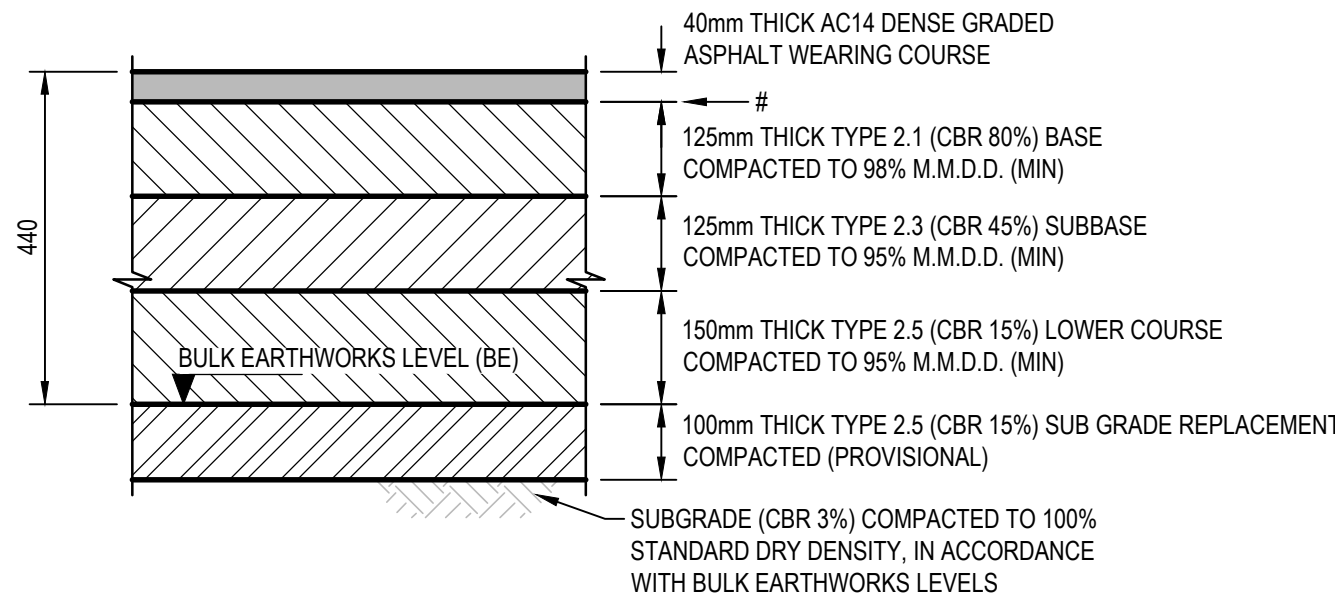


PAVEMENT TYPE 1
LIGHT DUTY ASPHALT FLEXIBLE PAVEMENT
SCALE 1:10

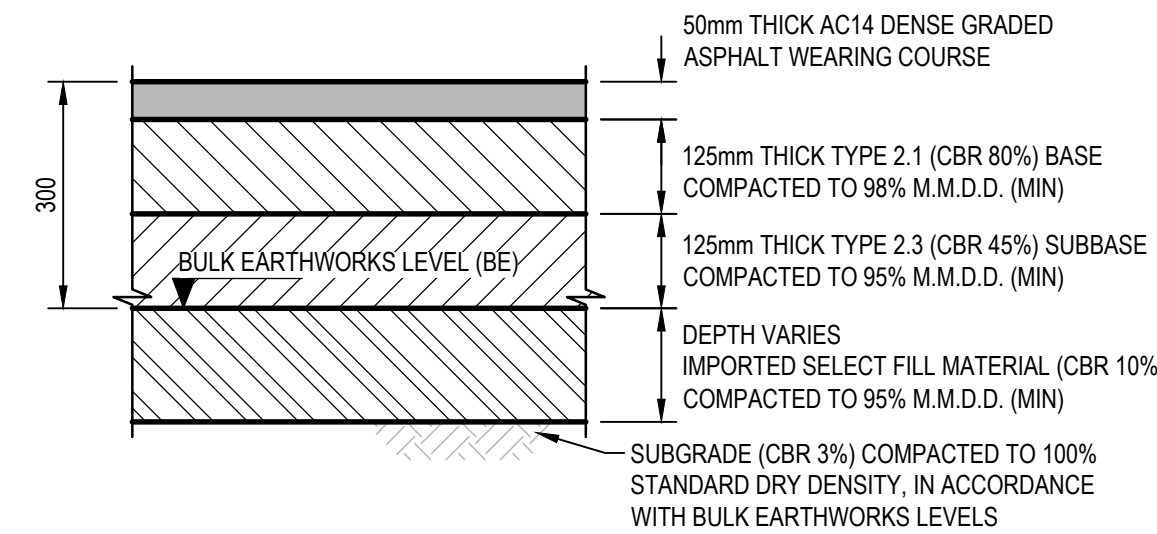


PAVEMENT TYPE 2
HEAVY DUTY ASPHALT FLEXIBLE PAVEMENT
SCALE 1:10

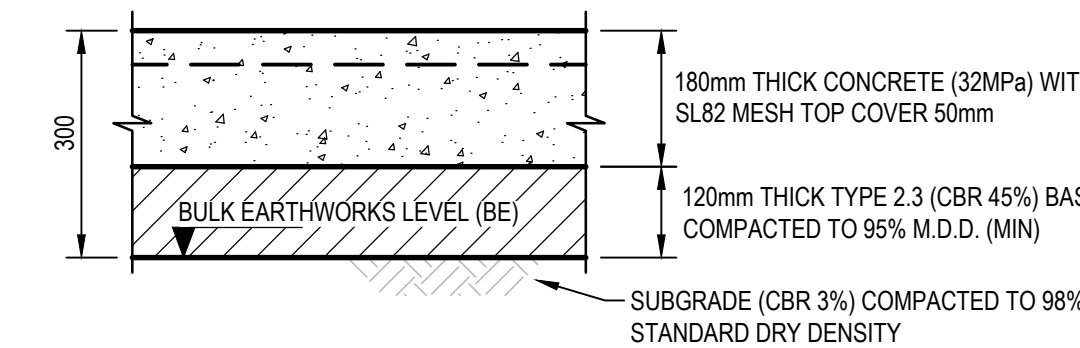


PAVEMENT TYPE 3
HEAVY DUTY CONCRETE PAVEMENT
SCALE 1:10

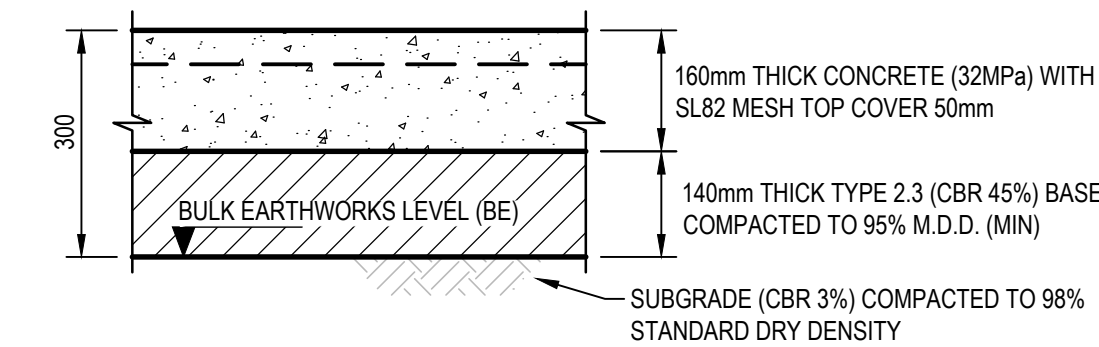


PAVEMENT TYPE 4
LIGHT DUTY CONCRETE PAVEMENT
SCALE 1:10

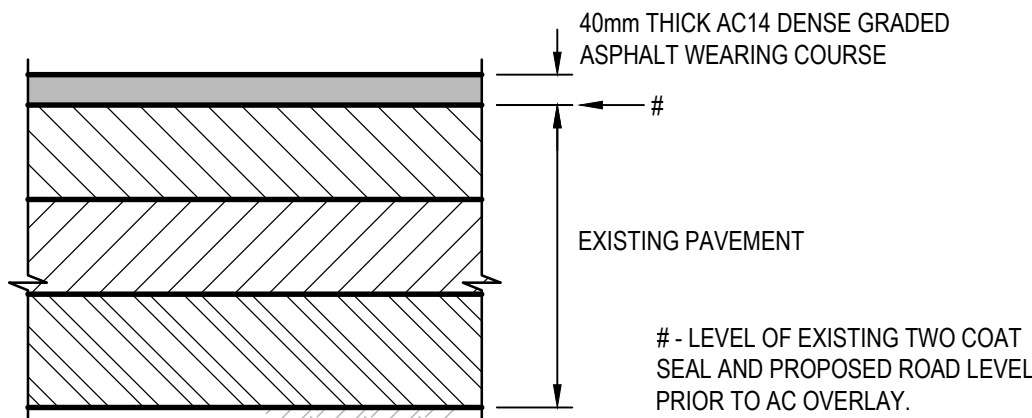


PAVEMENT TYPE 5
AC OVERLAY EXISTING PAVEMENT
SCALE 1:10

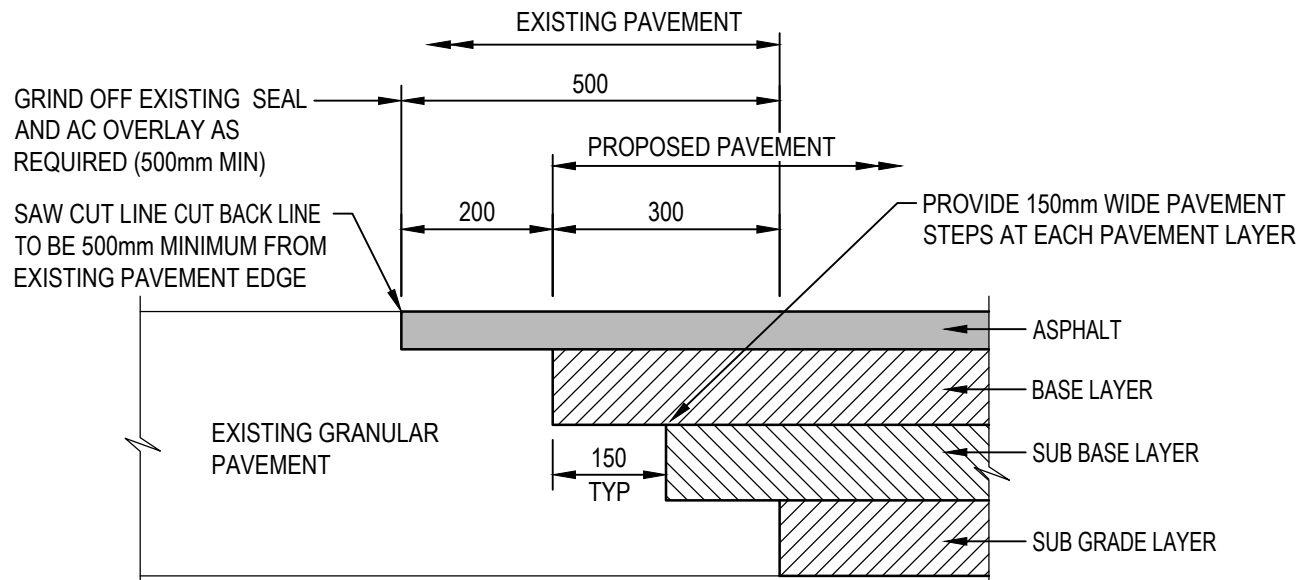


GRANULAR PAVEMENT JOINT DETAIL
SCALE 1:10

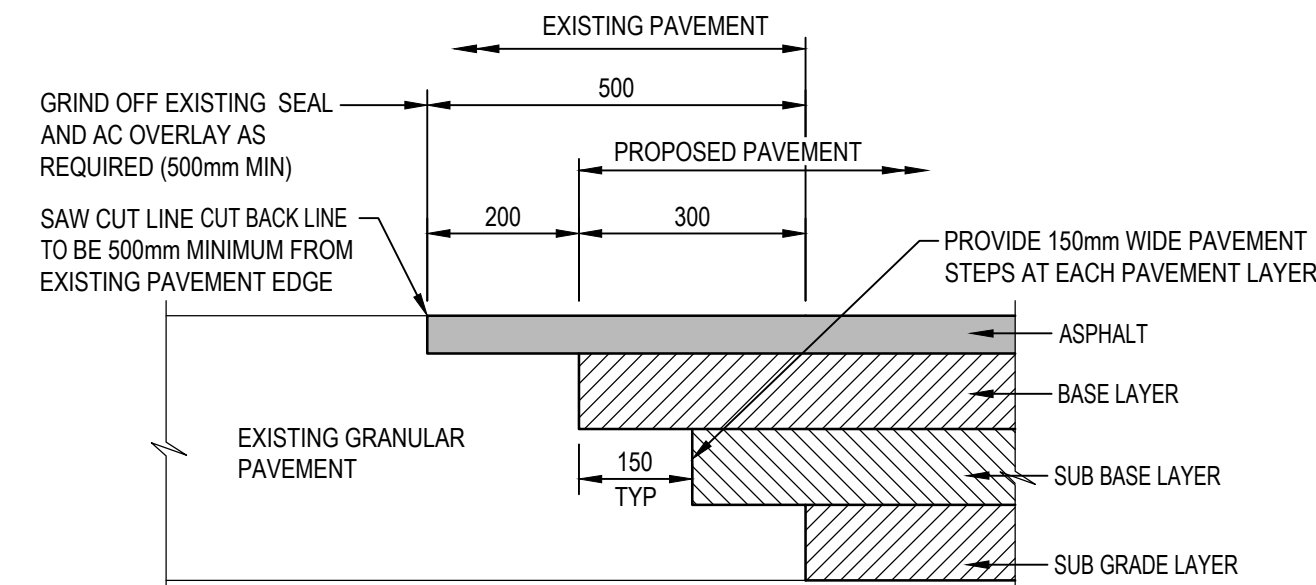

GRANULAR PAVEMENT JOINT DETAIL
SCALE 1:10

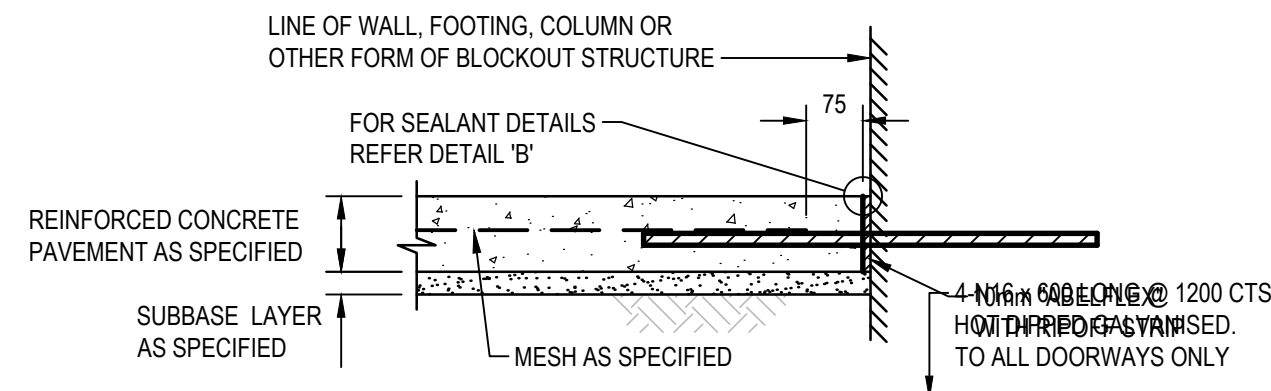


EXPANSION JOINT ABUTTING STRUCTURE (EJS)
SCALE 1:10

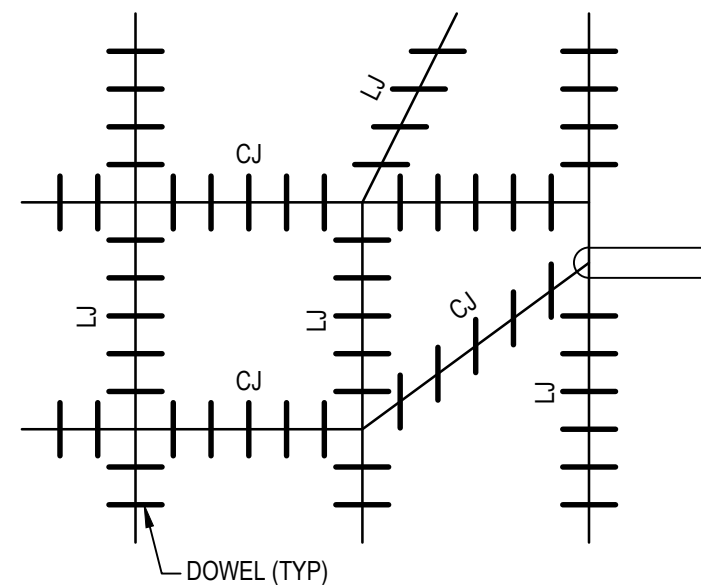


DOWEL ORIENTATIONS
NTS


NOTE: WHERE CONTRACTION JOINTS ARE SKEW TO THE MAIN JOINTING LAYOUT, ENSURE THAT THE DOWELS ARE ALIGNED PARALLEL TO THE MAIN JOINTING LAYOUT.

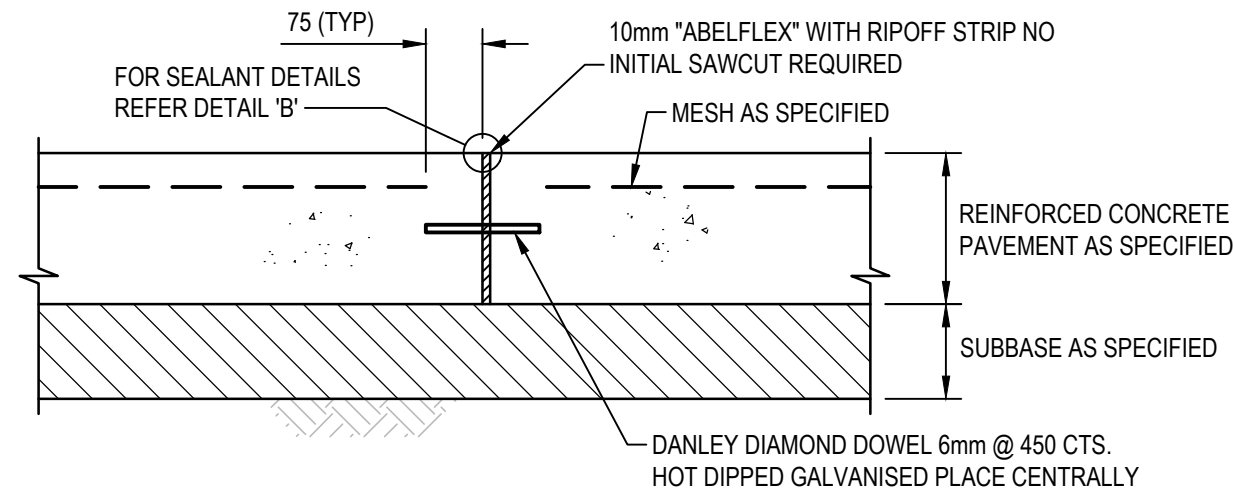


EXPANSION JOINT (EJ)
ALSO TRANSVERSE STOP WORK JOINT
SCALE 1:10

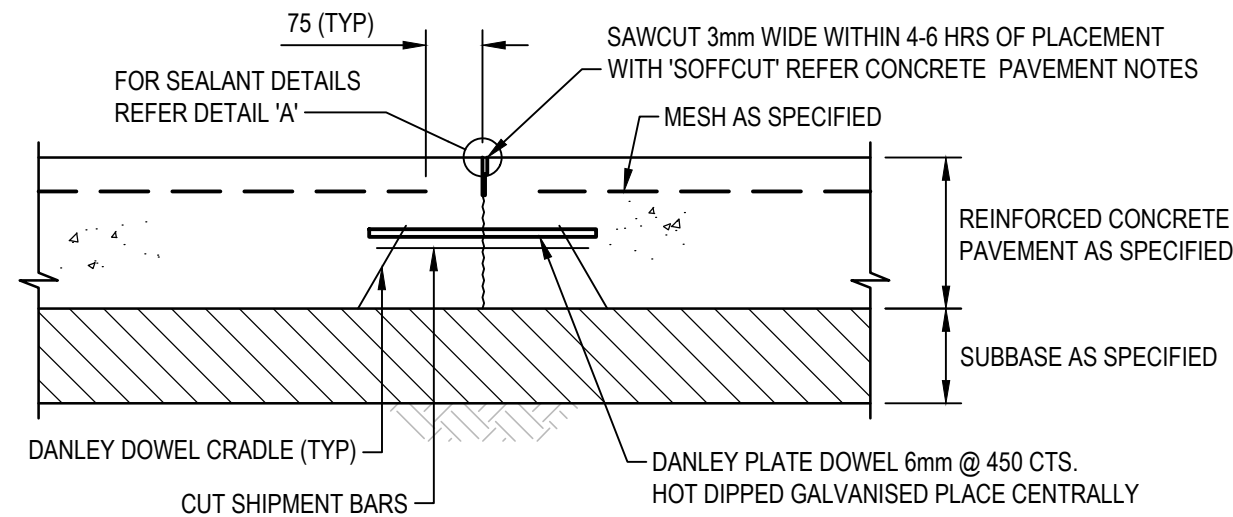


SAWCUT JOINT (SJ)
(POUR OVER)
SCALE 1:10

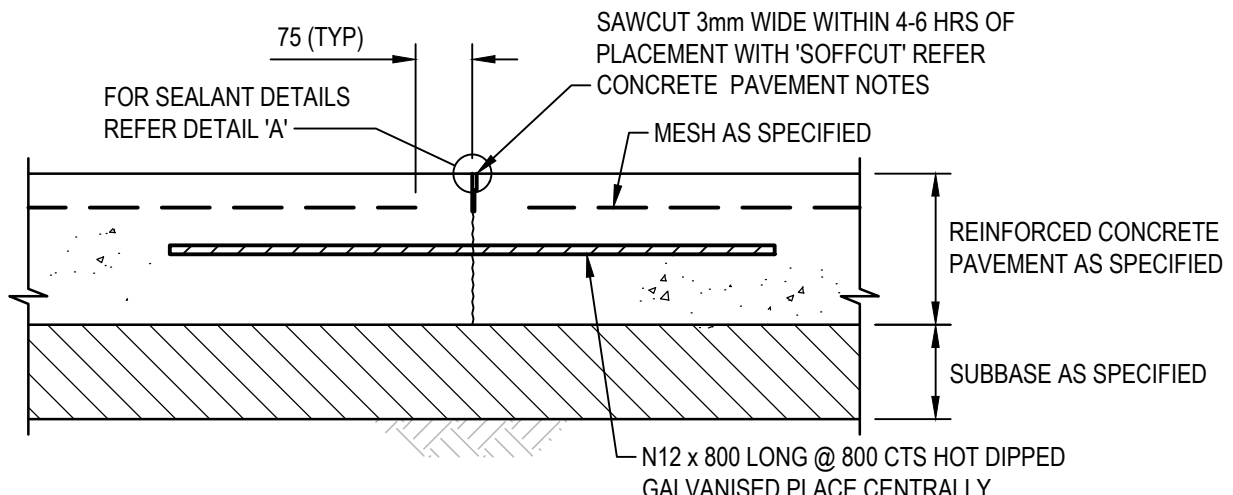


LONGITUDINAL CONTRACTION JOINT (LJ)
(POUR OVER)
SCALE 1:10

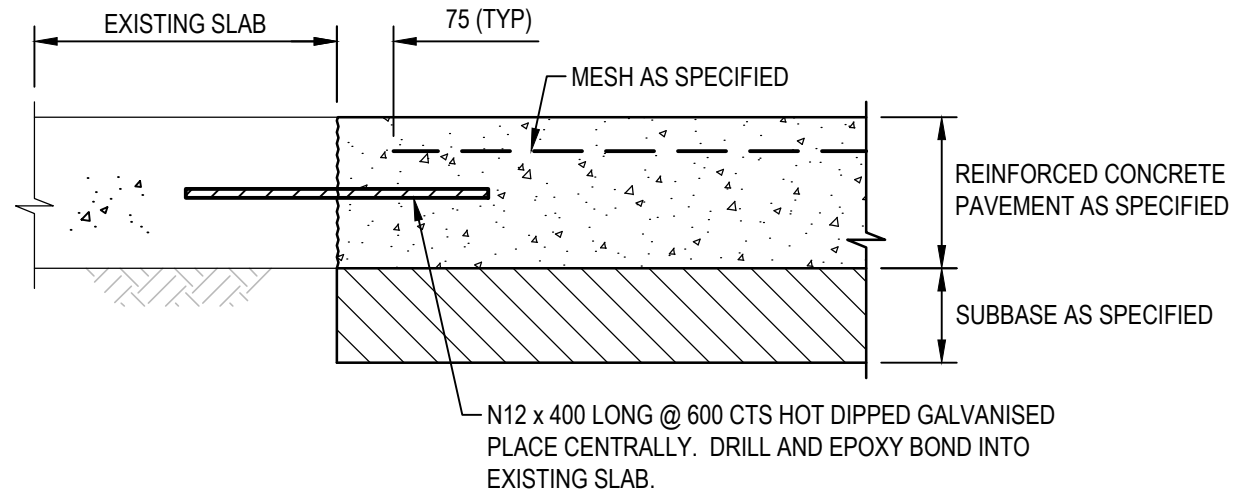


EXPANSION JOINT ABUTTING EXISTING SLAB (EJE)
SCALE 1:10

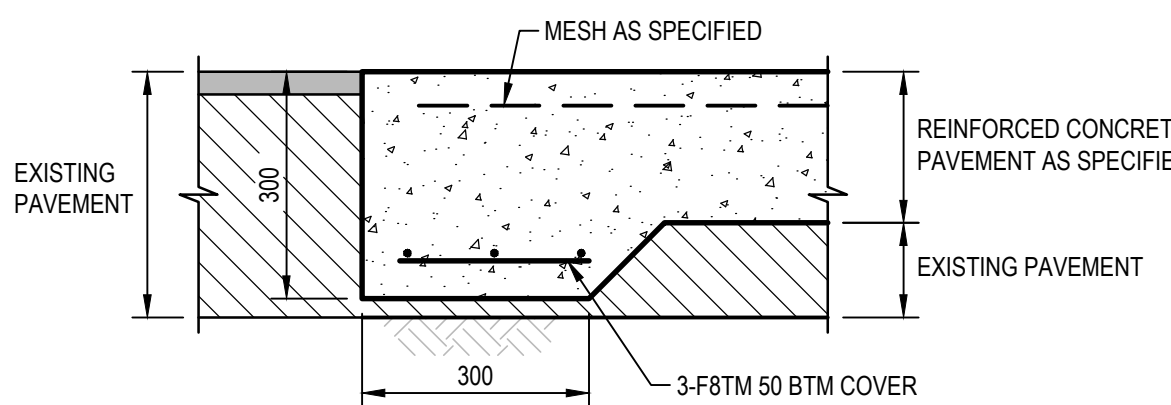


CONCRETE EDGE THICKENING (ET)
SCALE 1:10

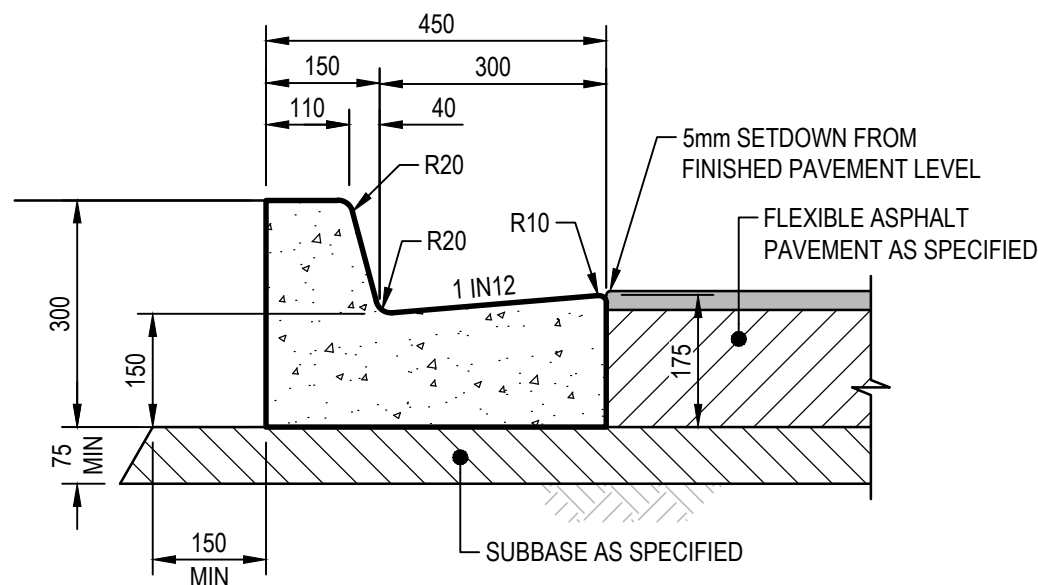

BARRIER KERB AND CHANNEL (BKC)
SCALE 1:10

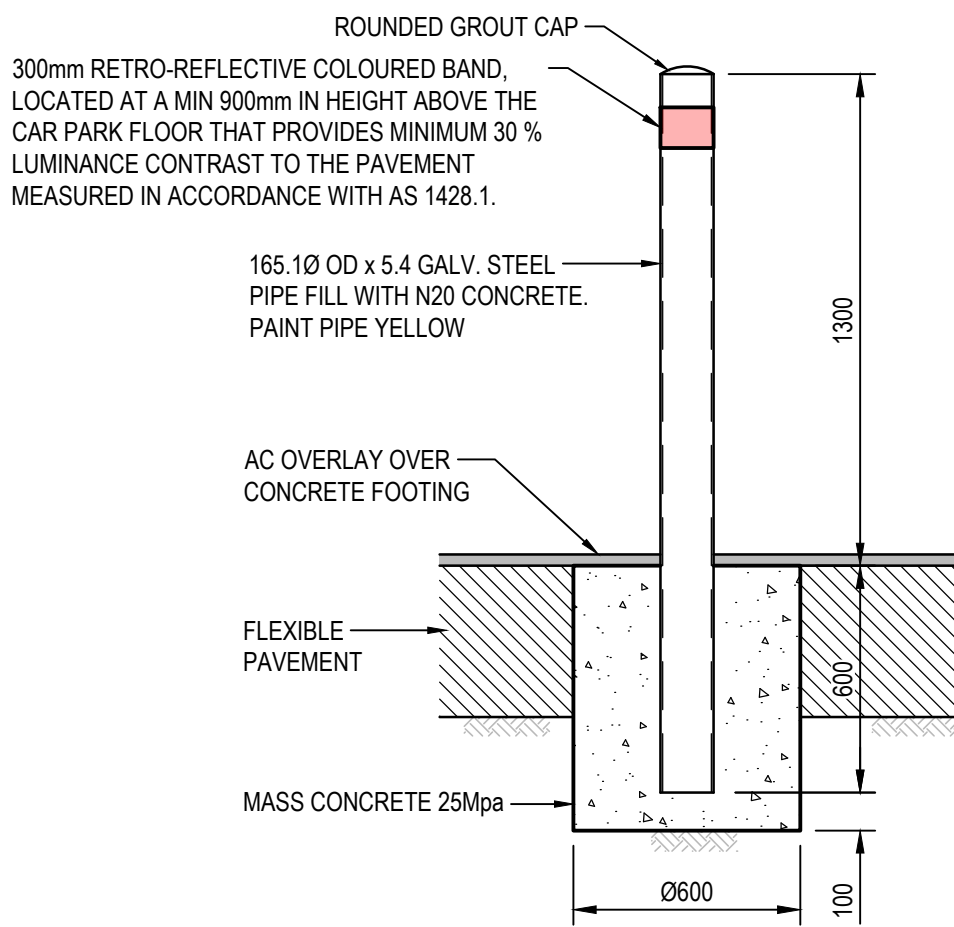

BOLLARD DETAIL
CAR BOLLARD IN FLEXIBLE PAVEMENT
SCALE 1:20

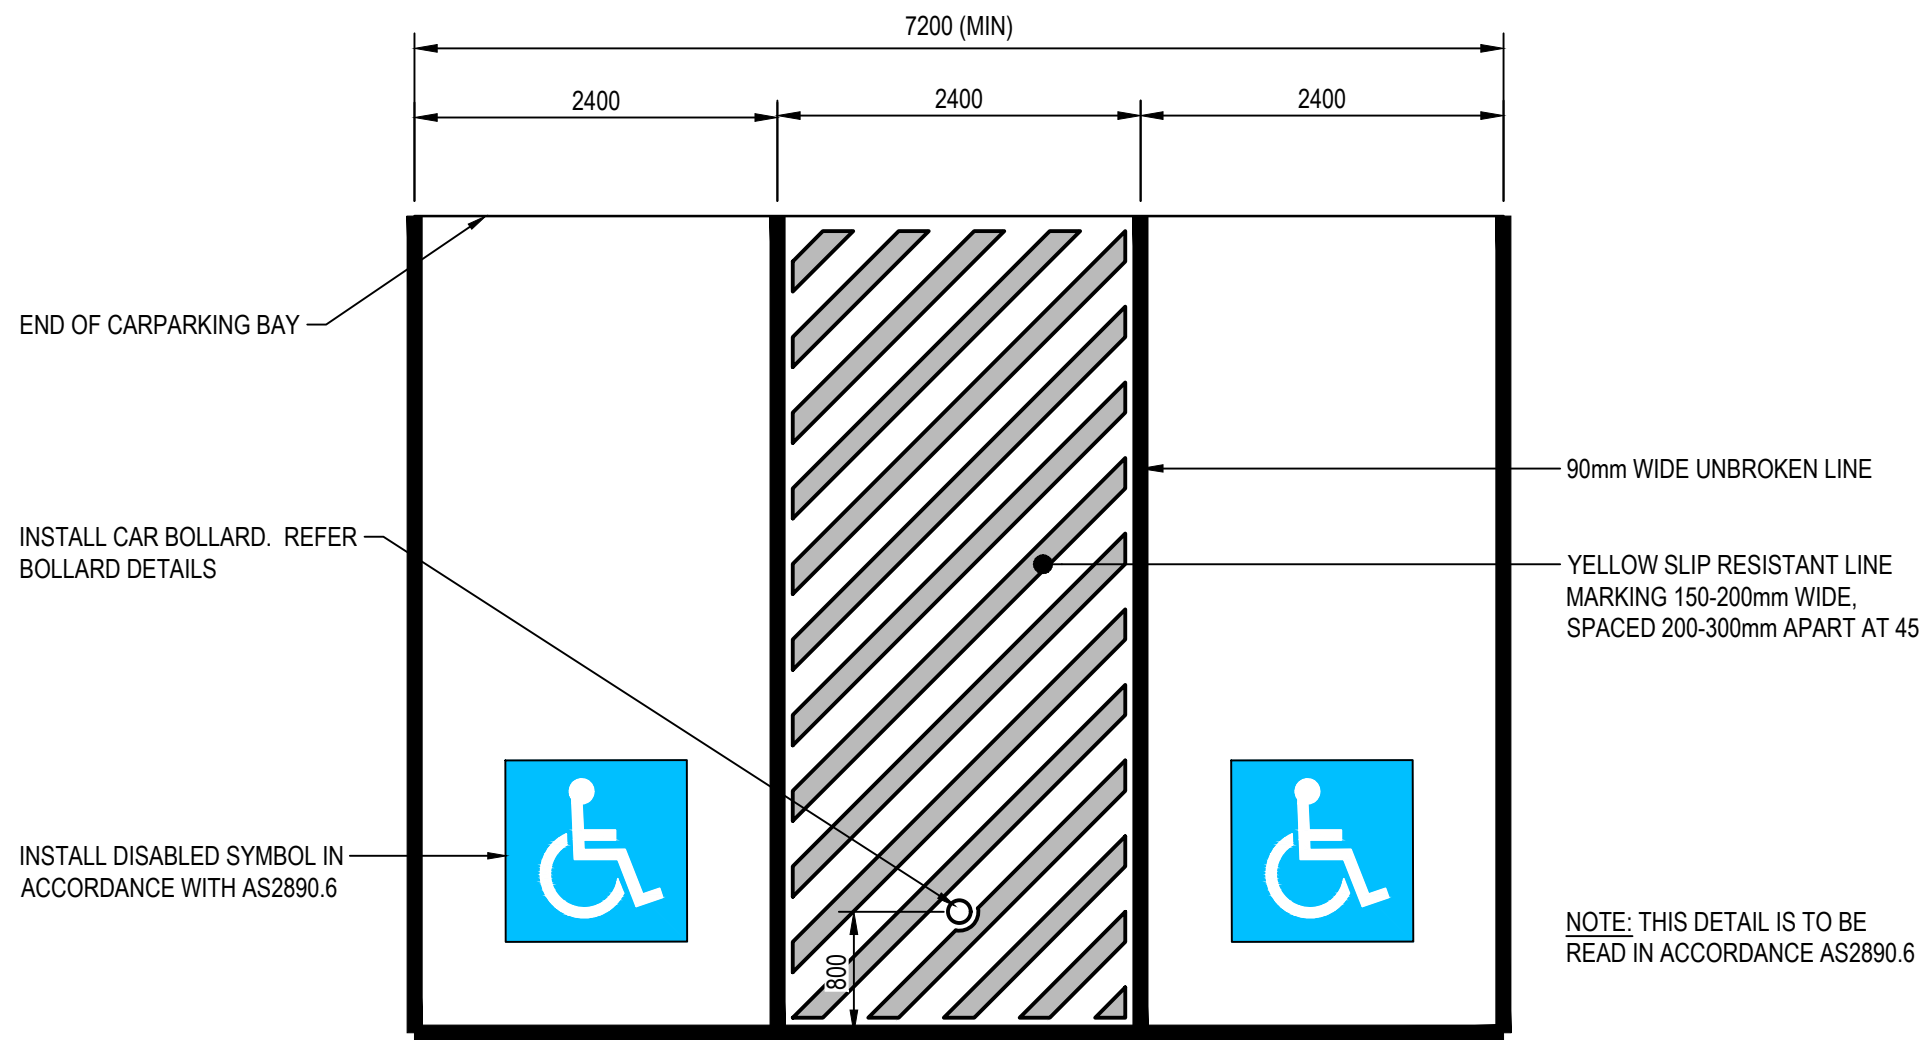

TYPICAL PWD AND SHARED ZONE
SCALE 1:50

P1	30/01/2026	RO	DRAFT 60% DESIGN DEVELOPMENT	JC	JC
REV	DATE	BY	DESCRIPTION	CHK	APP
DRAWING STATUS:			PRELIMINARY		



<http://www.wsp.com>

CLIENT:



ARCHITECT:



PROJECT:

CQU ROCKHAMPTON TAFE

TITLE:

BUILDING 36 CIVIL DETAILS

SCALE @ A1:

AS ABOVE

CHECKED:

JC

APPROVED:

JC

PROJECT NUMBER:

PS229518

DRAWN:

RO

DATE:

1/30/2026

DRAWING No:

C240

REV:

P1

© WSP Australia Pty Ltd