

DO NOT SCALE

STEELWORK ROOF:

NOTES:

CONTRACTOR TO ALLOW FOR ADDITIONAL PURLIN SUPPORTS UNDER ALL GUTTERS.

REFER TO ARCHITECT FOR WATERPROOFING & SET-OUT DETAILS.

STEELWORK GENERAL:

NOTES:

READ IN CONJUNCTION WITH STEELWORK NOTES ON GENERAL
NOTES DRAWING A00-0100-00-04.


STRUCTURAL PLANS SHOW PRIMARY STEELWORK & DOES NOT INCLUDE SECONDARY OR ARCHITECTURAL STEELWORK OUTSIDE THE STRUCTURAL SCOPE OF WORKS.

ALL TENDERERS TO VISIT SITE & CONSIDER SITE ACCESS AND CONSTRAINTS IN THEIR SUBMISSIONS. ANY ADDITIONAL SPLICE LOCATIONS TO BE SUBMITTED TO THE STRUCTURAL ENGINEER, PRIOR TO FABRICATION, FOR REVIEW.

ALL EXPOSED STEELWORK TO BE HOT-DIP GALVANISED. ALL FIRE PROTECTION OF STEELWORK BY OTHERS.

SERVICES ENGINEERS REQUIRED TO SUBMIT PROPOSED LOCATIONS OF ANY BEAM PENETRATIONS FOR STRUCTURAL ENGINEER'S REVIEW. NO PENETRATIONS ARE PERMITTED THROUGH BEAMS UNTIL AGREED IN WRITING BY THE STRUCTURAL ENGINEER.

CONTRACTOR TO ALLOW FOR PENETRATING EXISTING ROOF &
FLASHING/WATERPROOFING AROUND PENETRATION

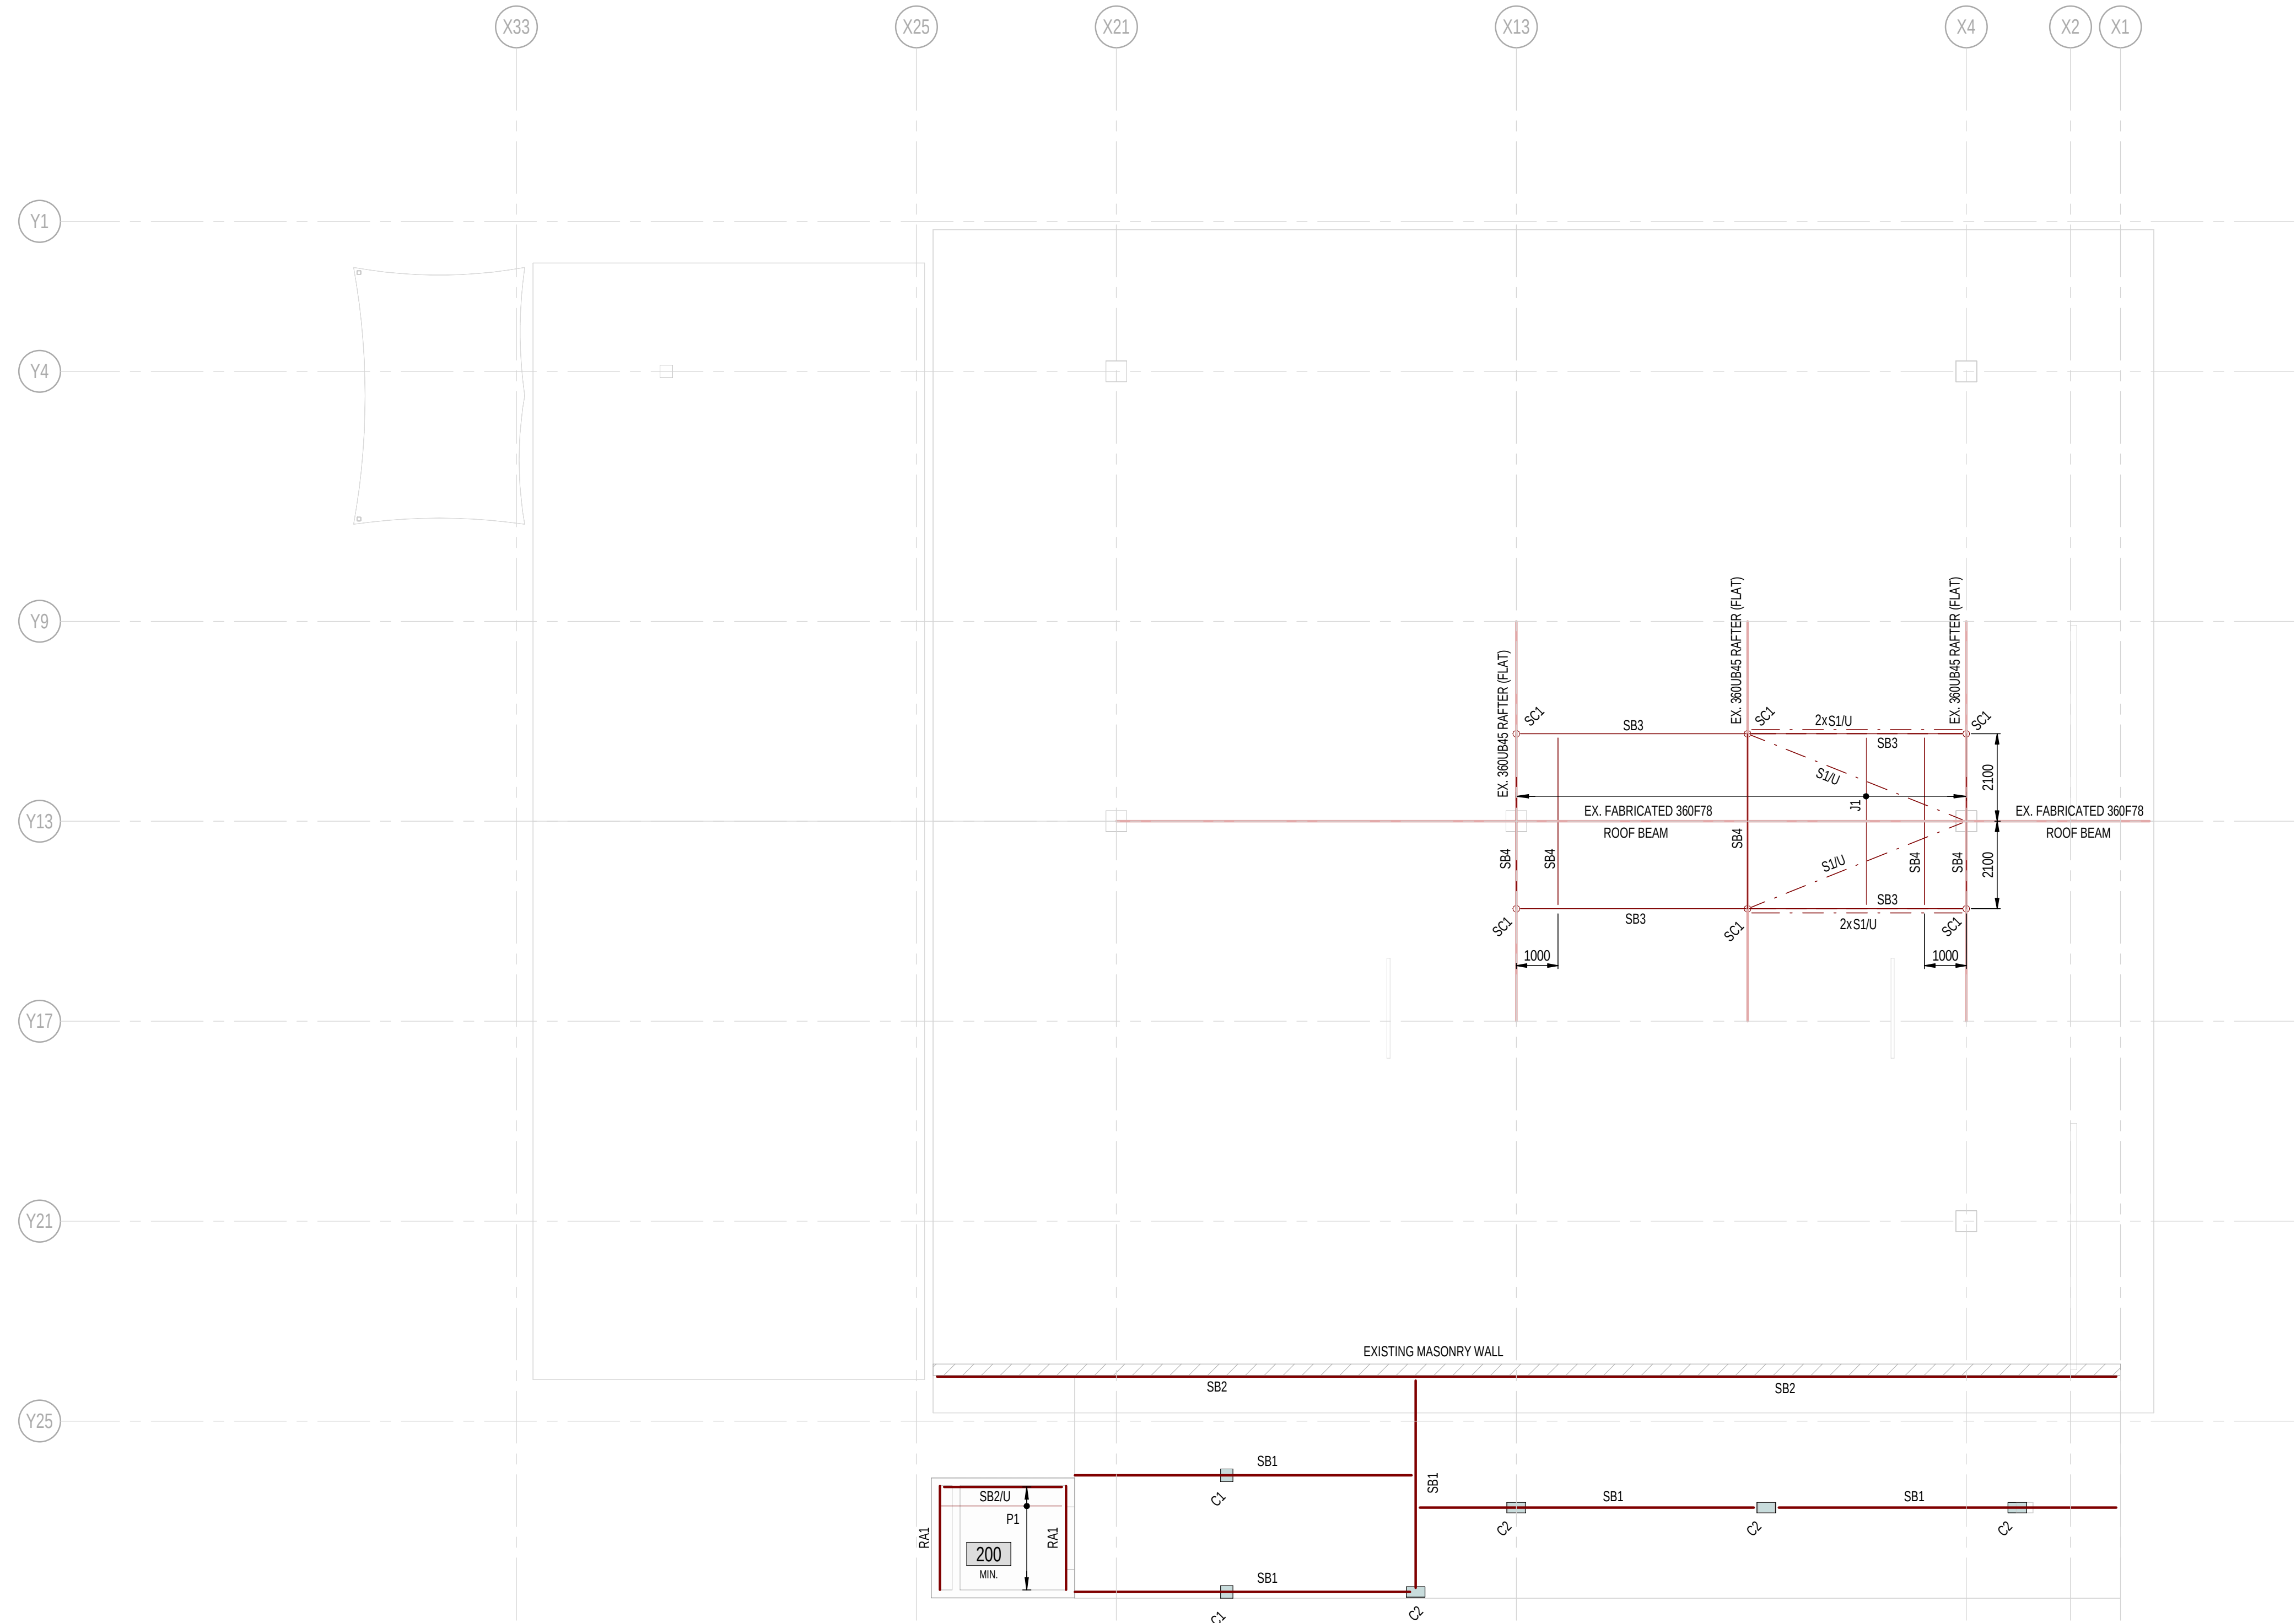

ROOF LEVEL STEEL COLUMN SCHEDULE		
MARK	SIZE	REMARKS
SC1	165.1x5.4 CHS	STEEL COLUMN

ROOF LEVEL STEEL FRAMING SCHEDULE		
MARK	SIZE	REMARKS
J1	12SPFC	<varies>
P1	C150I2	ROOF PURLINS AT 50 MAX CRS.
RA1	125x75x8 UA	RAKING ANGLE
S1	89x5.0 CHS	BRACING STRUT (BELOW EXISTING ROOF SHEETING TO BRACE PLANT PLATFORM
SB1	200x100x6.0 RHS	STEEL BEAM
SB2	100x8 EA	FIXED TO EXISTING MASONRY EXTERNAL WALL AT 600 MAX CRS.
SB3	250PFC	PLANT PLATFORM BEAM
SB4	200UCS2	PLANT PLATFORM BEAM

INFORMATION REFLECTED ON THIS DRAWING REPRESENTS STRUCTURAL DESIGN DEVELOPED FOR D&C TENDER ADVISE ONLY, AND SHOULD NOT BE REGARDED AS COMPLETE. THE D&C CONTRACTOR SHOULD REFER TO ALL ASSOCIATED ARCHITECTURAL AND OTHER DISCIPLINE DRAWINGS, PROJECT BRIEFS AND CLIENT REQUIREMENTS AND MAKE ADEQUATE ALLOWANCES FOR ALL NECESSARY STRUCTURAL WORKS TO MEET THESE REQUIREMENTS, EQUIPMENT SCHEDULES AND COMPLIANCE WITH THE NCC & APPROPRIATE AUSTRALIAN STANDARDS

[illegible]

<http://www.wsp.com>

CLIENT



PEDDLE THORP

ARCHITECT:

PROJECT:

CQU ROCKHAMPTON TAFE
CONSOLIDATION - STAGE 2

TITLE:

BUILDING 36
ROOF FRAMING ARRANGEMENT PLAN

SCALE @ A1:

1:100

PROJECT NUMBER:

S229518

APPROVED:

DG

DATE: _____

1.2026

36-ST-DR-Z00-710-00-00

A

© WSP Australia Pty Ltd