



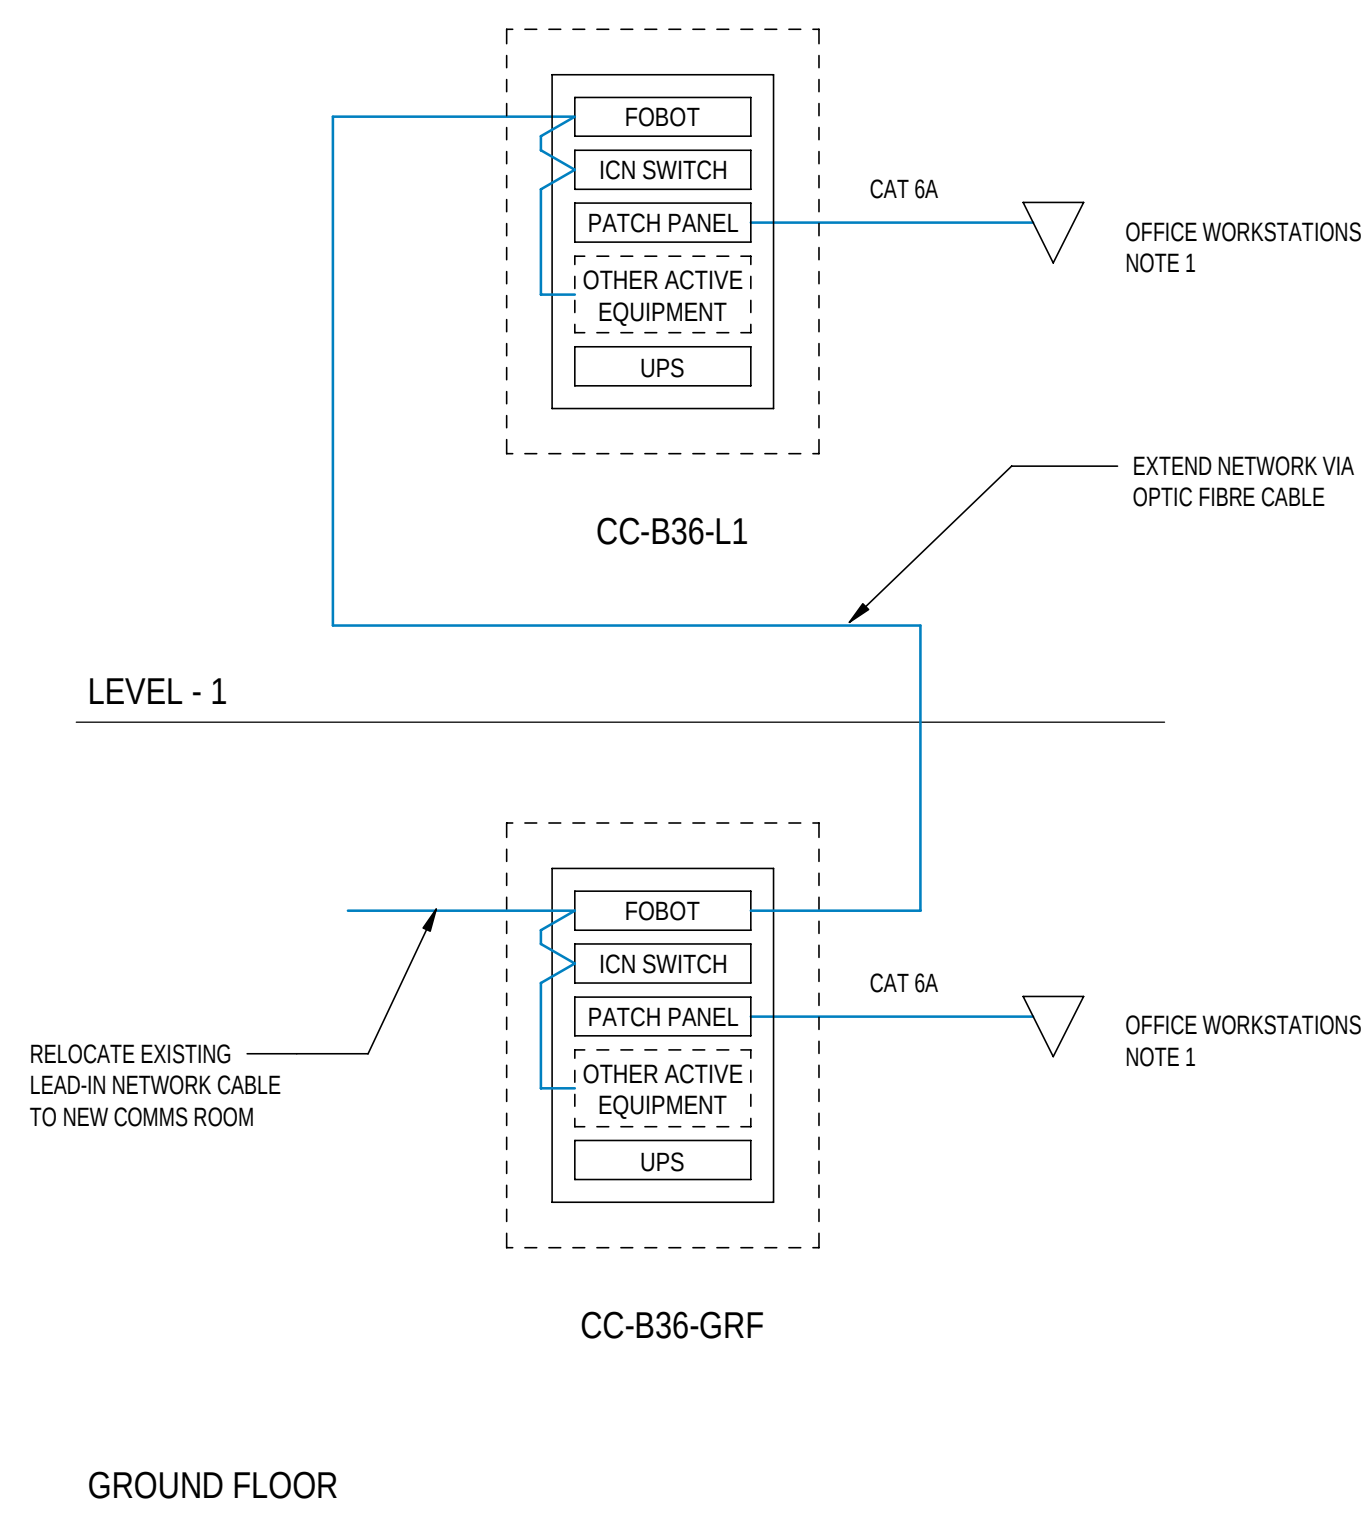


COMMS SCHEMATIC DIAGRAM

COMMUNICATION NOTES

- REFER TO THE DRAWING FOR EXACT NUMBER OF TELECOMMUNICATIONS OUTLETS.
- PROVIDE 2XVIA RACK MOUNTED UPS IN EVERY COMMS RACK.
- REFER TO LAYOUT DRAWINGS FOR QUANTITIES AND TYPE OF CAMERAS.

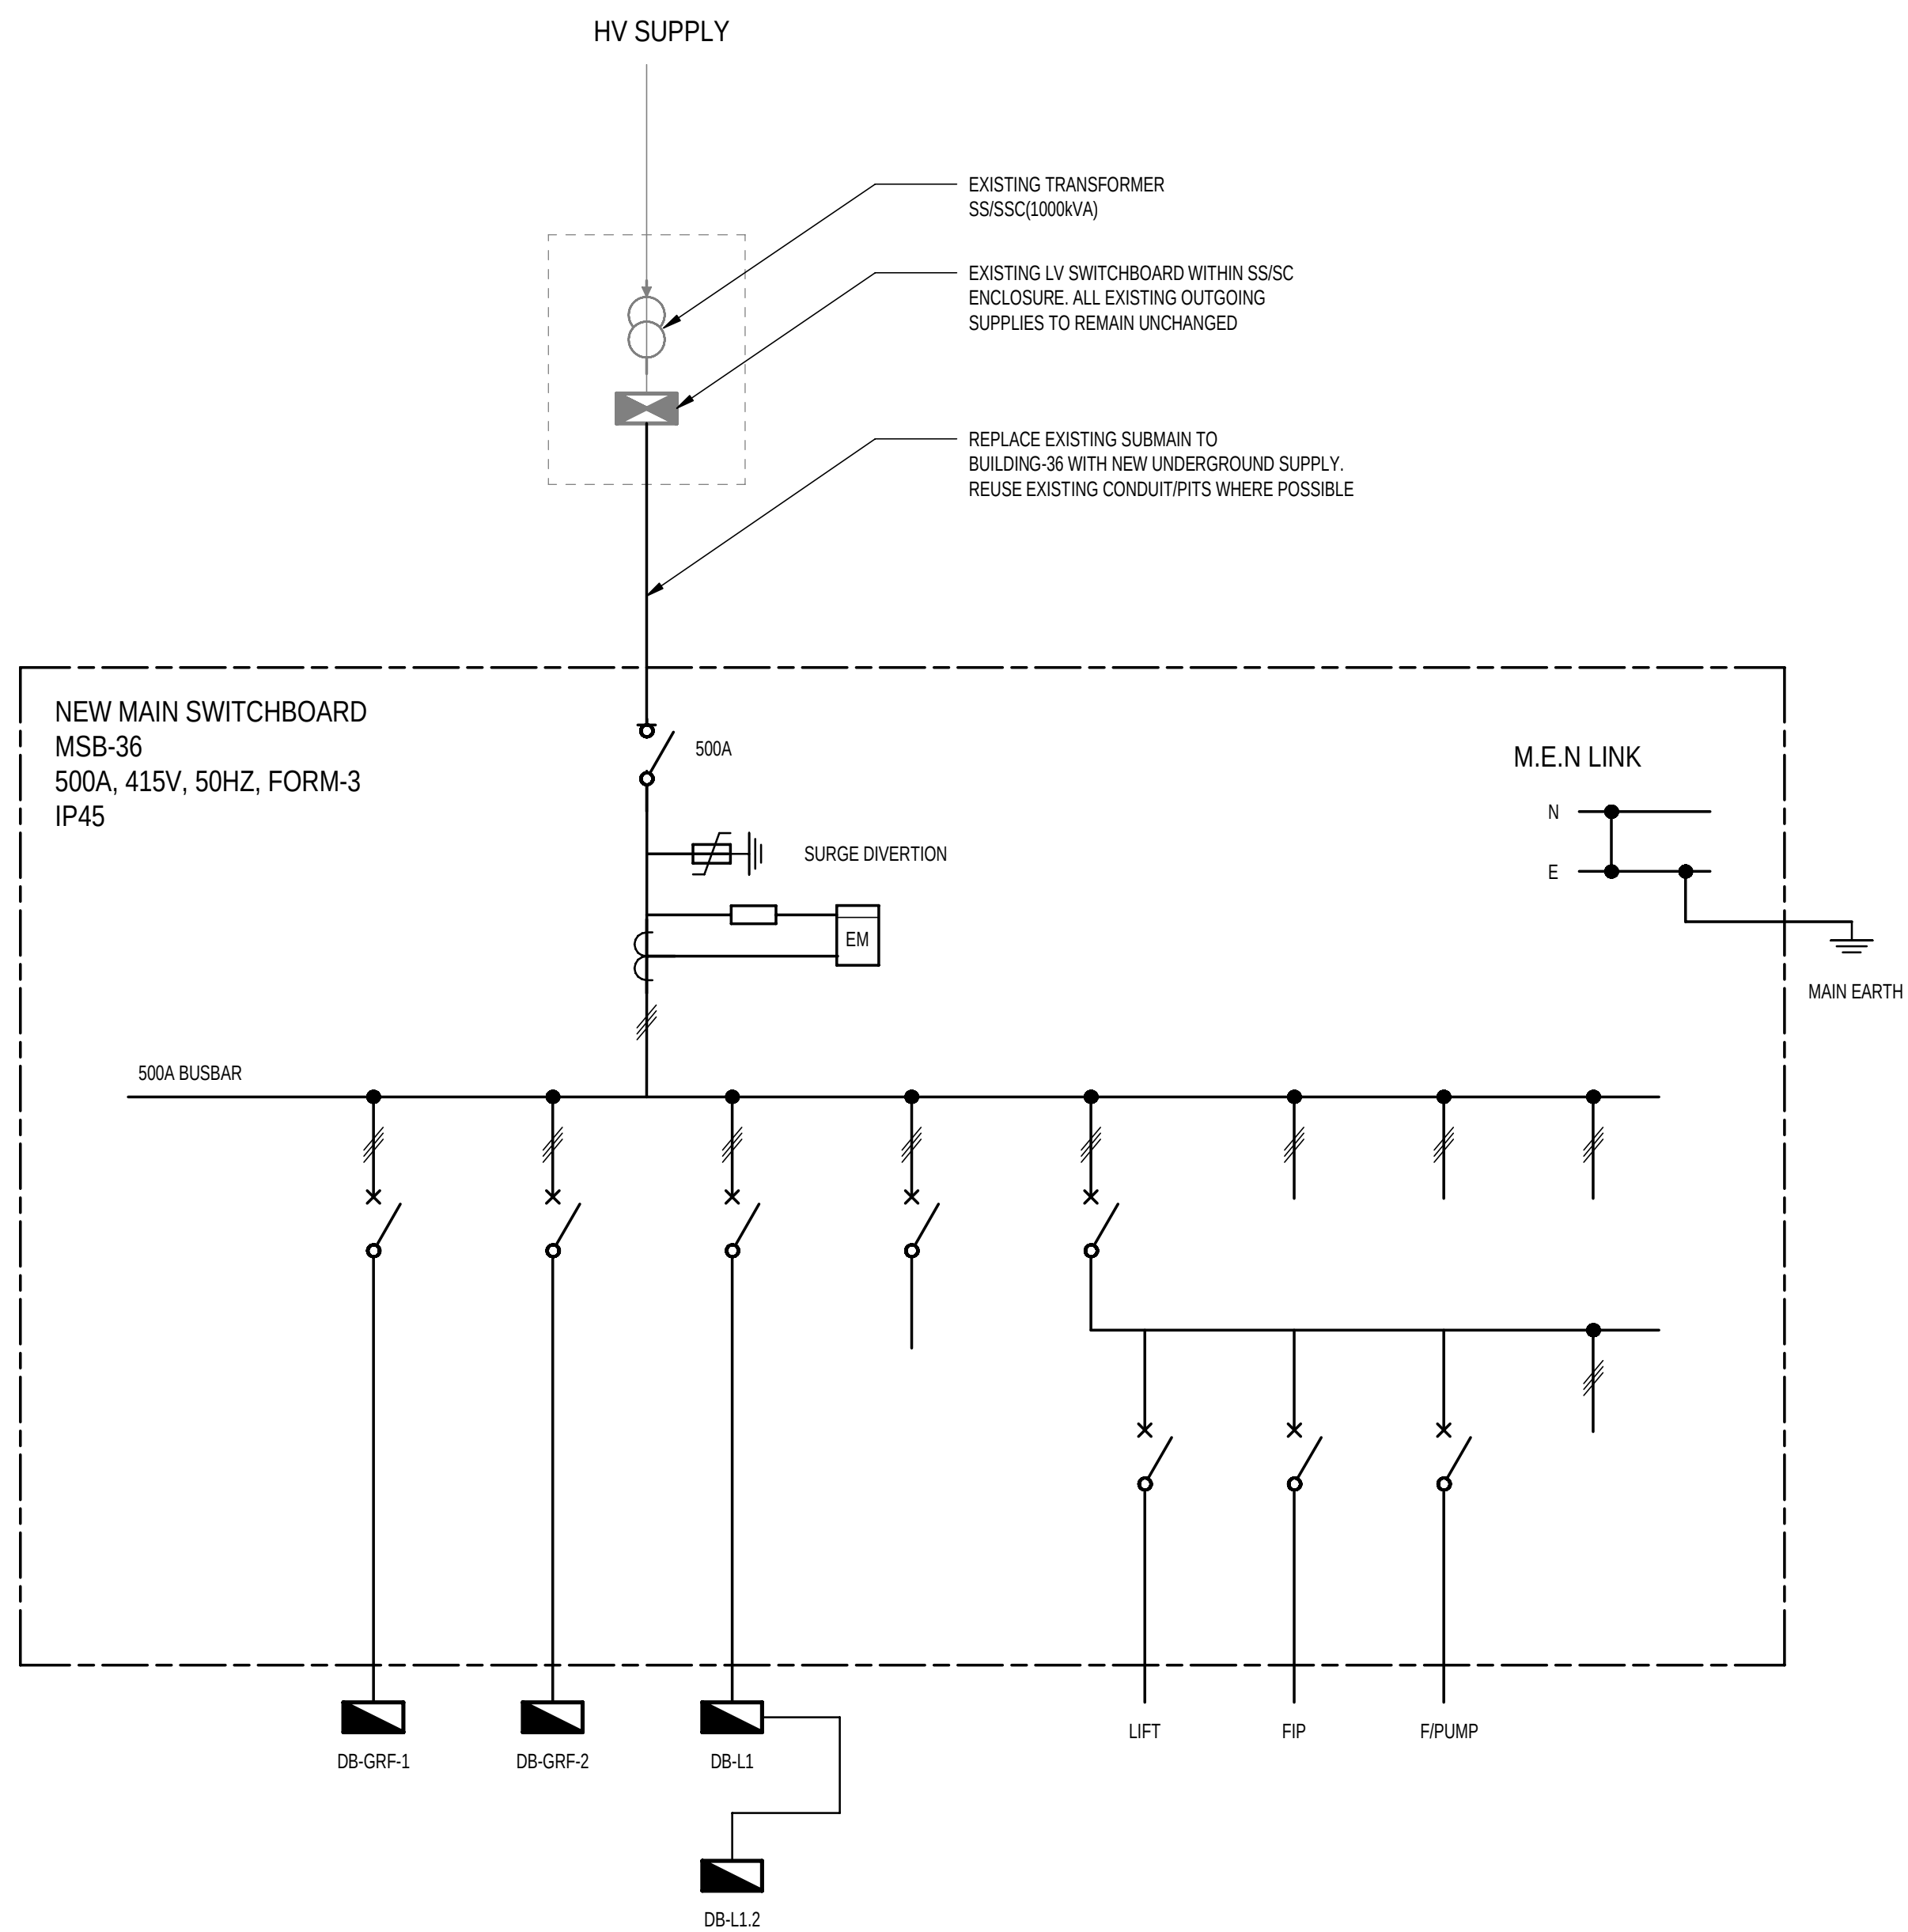

BUILDING B-36 SINGLE LINE DIAGRAM

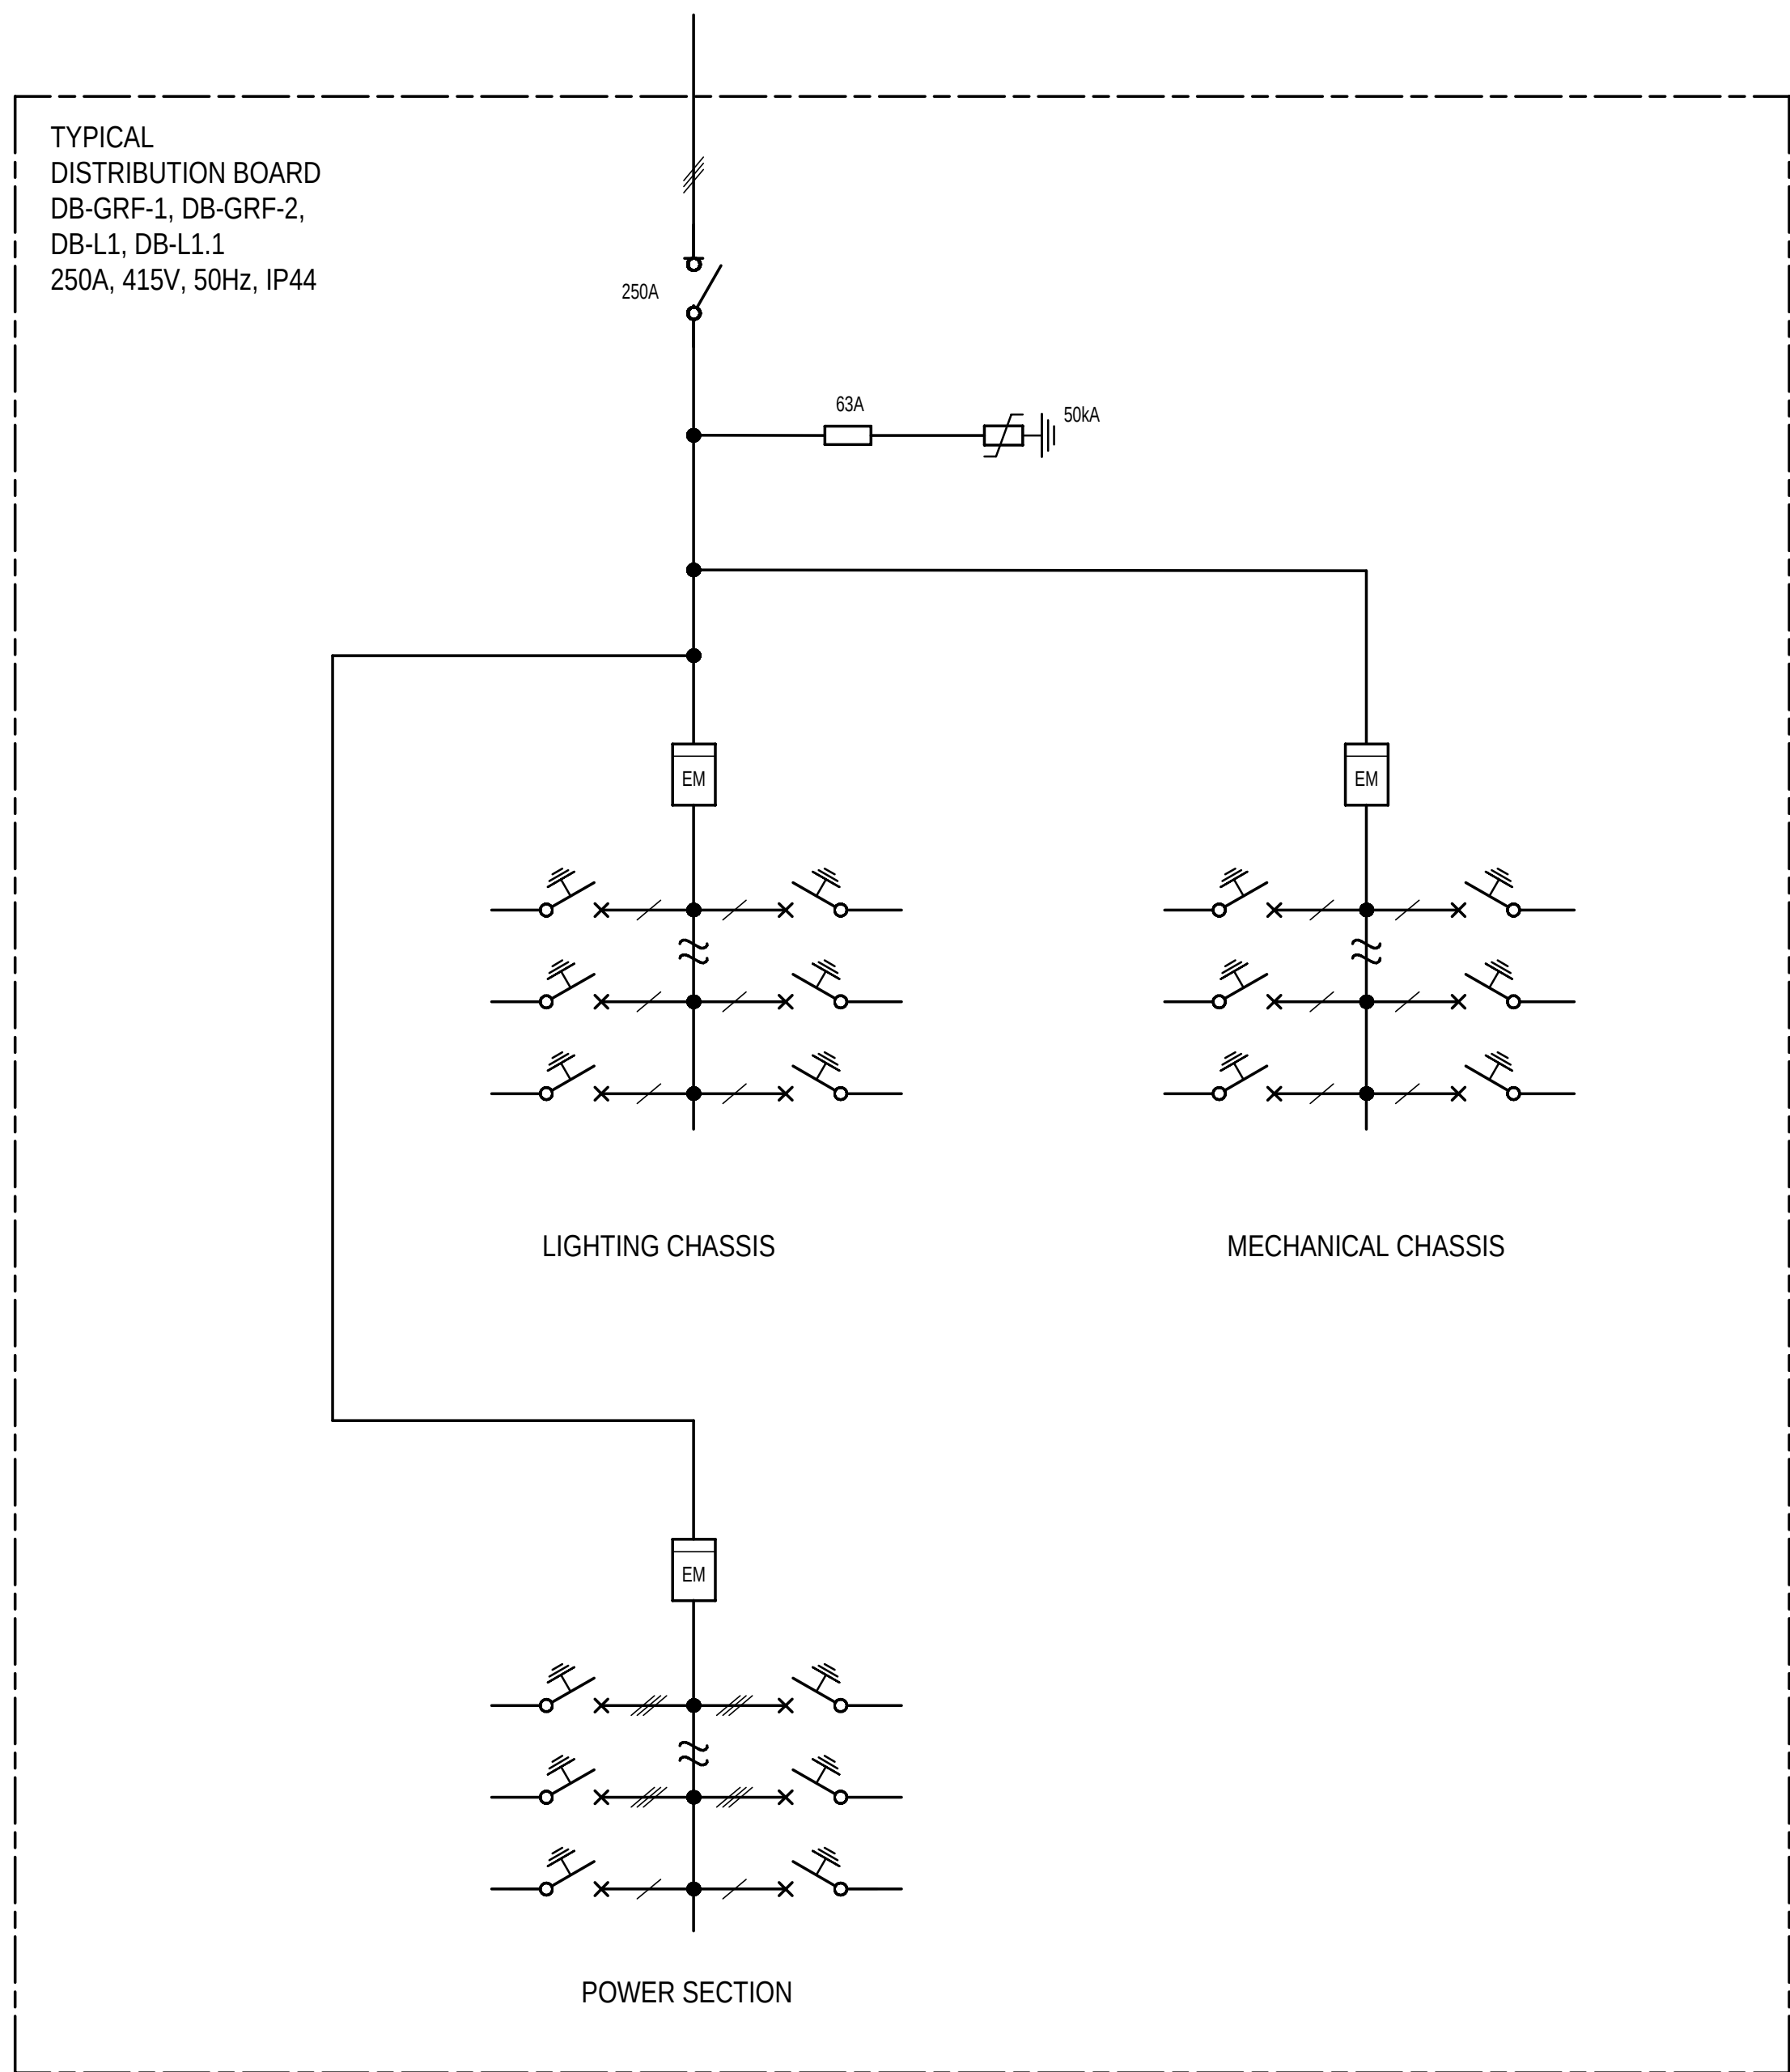

INFORMATION REFLECTED ON THIS DRAWING REPRESENTS ELECTRICAL SERVICES DESIGN DEVELOPED FOR D&C TENDER ADVISE ONLY, AND SHOULD NOT BE REGARDED AS COMPLETE. THE D&C CONTRACTOR SHOULD REFER TO ALL ASSOCIATED ARCHITECTURAL AND OTHER DISCIPLINE DRAWINGS, PROJECT BRIEF-S AND CLIENT REQUIREMENTS AND MAKE ADEQUATE ALLOWANCES FOR ALL NECESSARY ELECTRICAL SERVICES WORKS TO MEET THESE REQUIREMENTS, EQUIPMENT SCHEDULES AND COMPLIANCE WITH THE NCC & APPROPRIATE AUSTRALIAN STANDARDS

B	12.02.2020	MM	ISSUED FOR D&C TENDER	TP	SM
A	10.02.2020	MM	ISSUED FOR REVIEW	TP	SM
REV	DATE	BY	DESCRIPTION	CHK	APP

DESIGN DEVELOPMENT



900 Ann Street, Level 12, Fortitude Valley 4006
Tel: +61-7-3854-6200 Fax: +61-7-3854-6500
<http://www.wsp.com>

CLIENT: CQU

ARCHITECT: THOMSON ADSETT / PEDDLE THORP

PROJECT: CQU ROCKHAMPTON TAFE CONSOLIDATION

TITLE: ELECTRICAL SERVICES
BUILDING 36 - SCHEMATICS

SCALE @ A1	N.T.S	CHECKED	TP	APPROVED	SM
PROJECT NUMBER	PS229518	DRAWN	MM	DATE	JAN 2020

DRAWING NO.	B36-EL-DR-200-A00-00-00	REV.	B
-------------	-------------------------	------	---

© WSP Australia Pty Ltd