



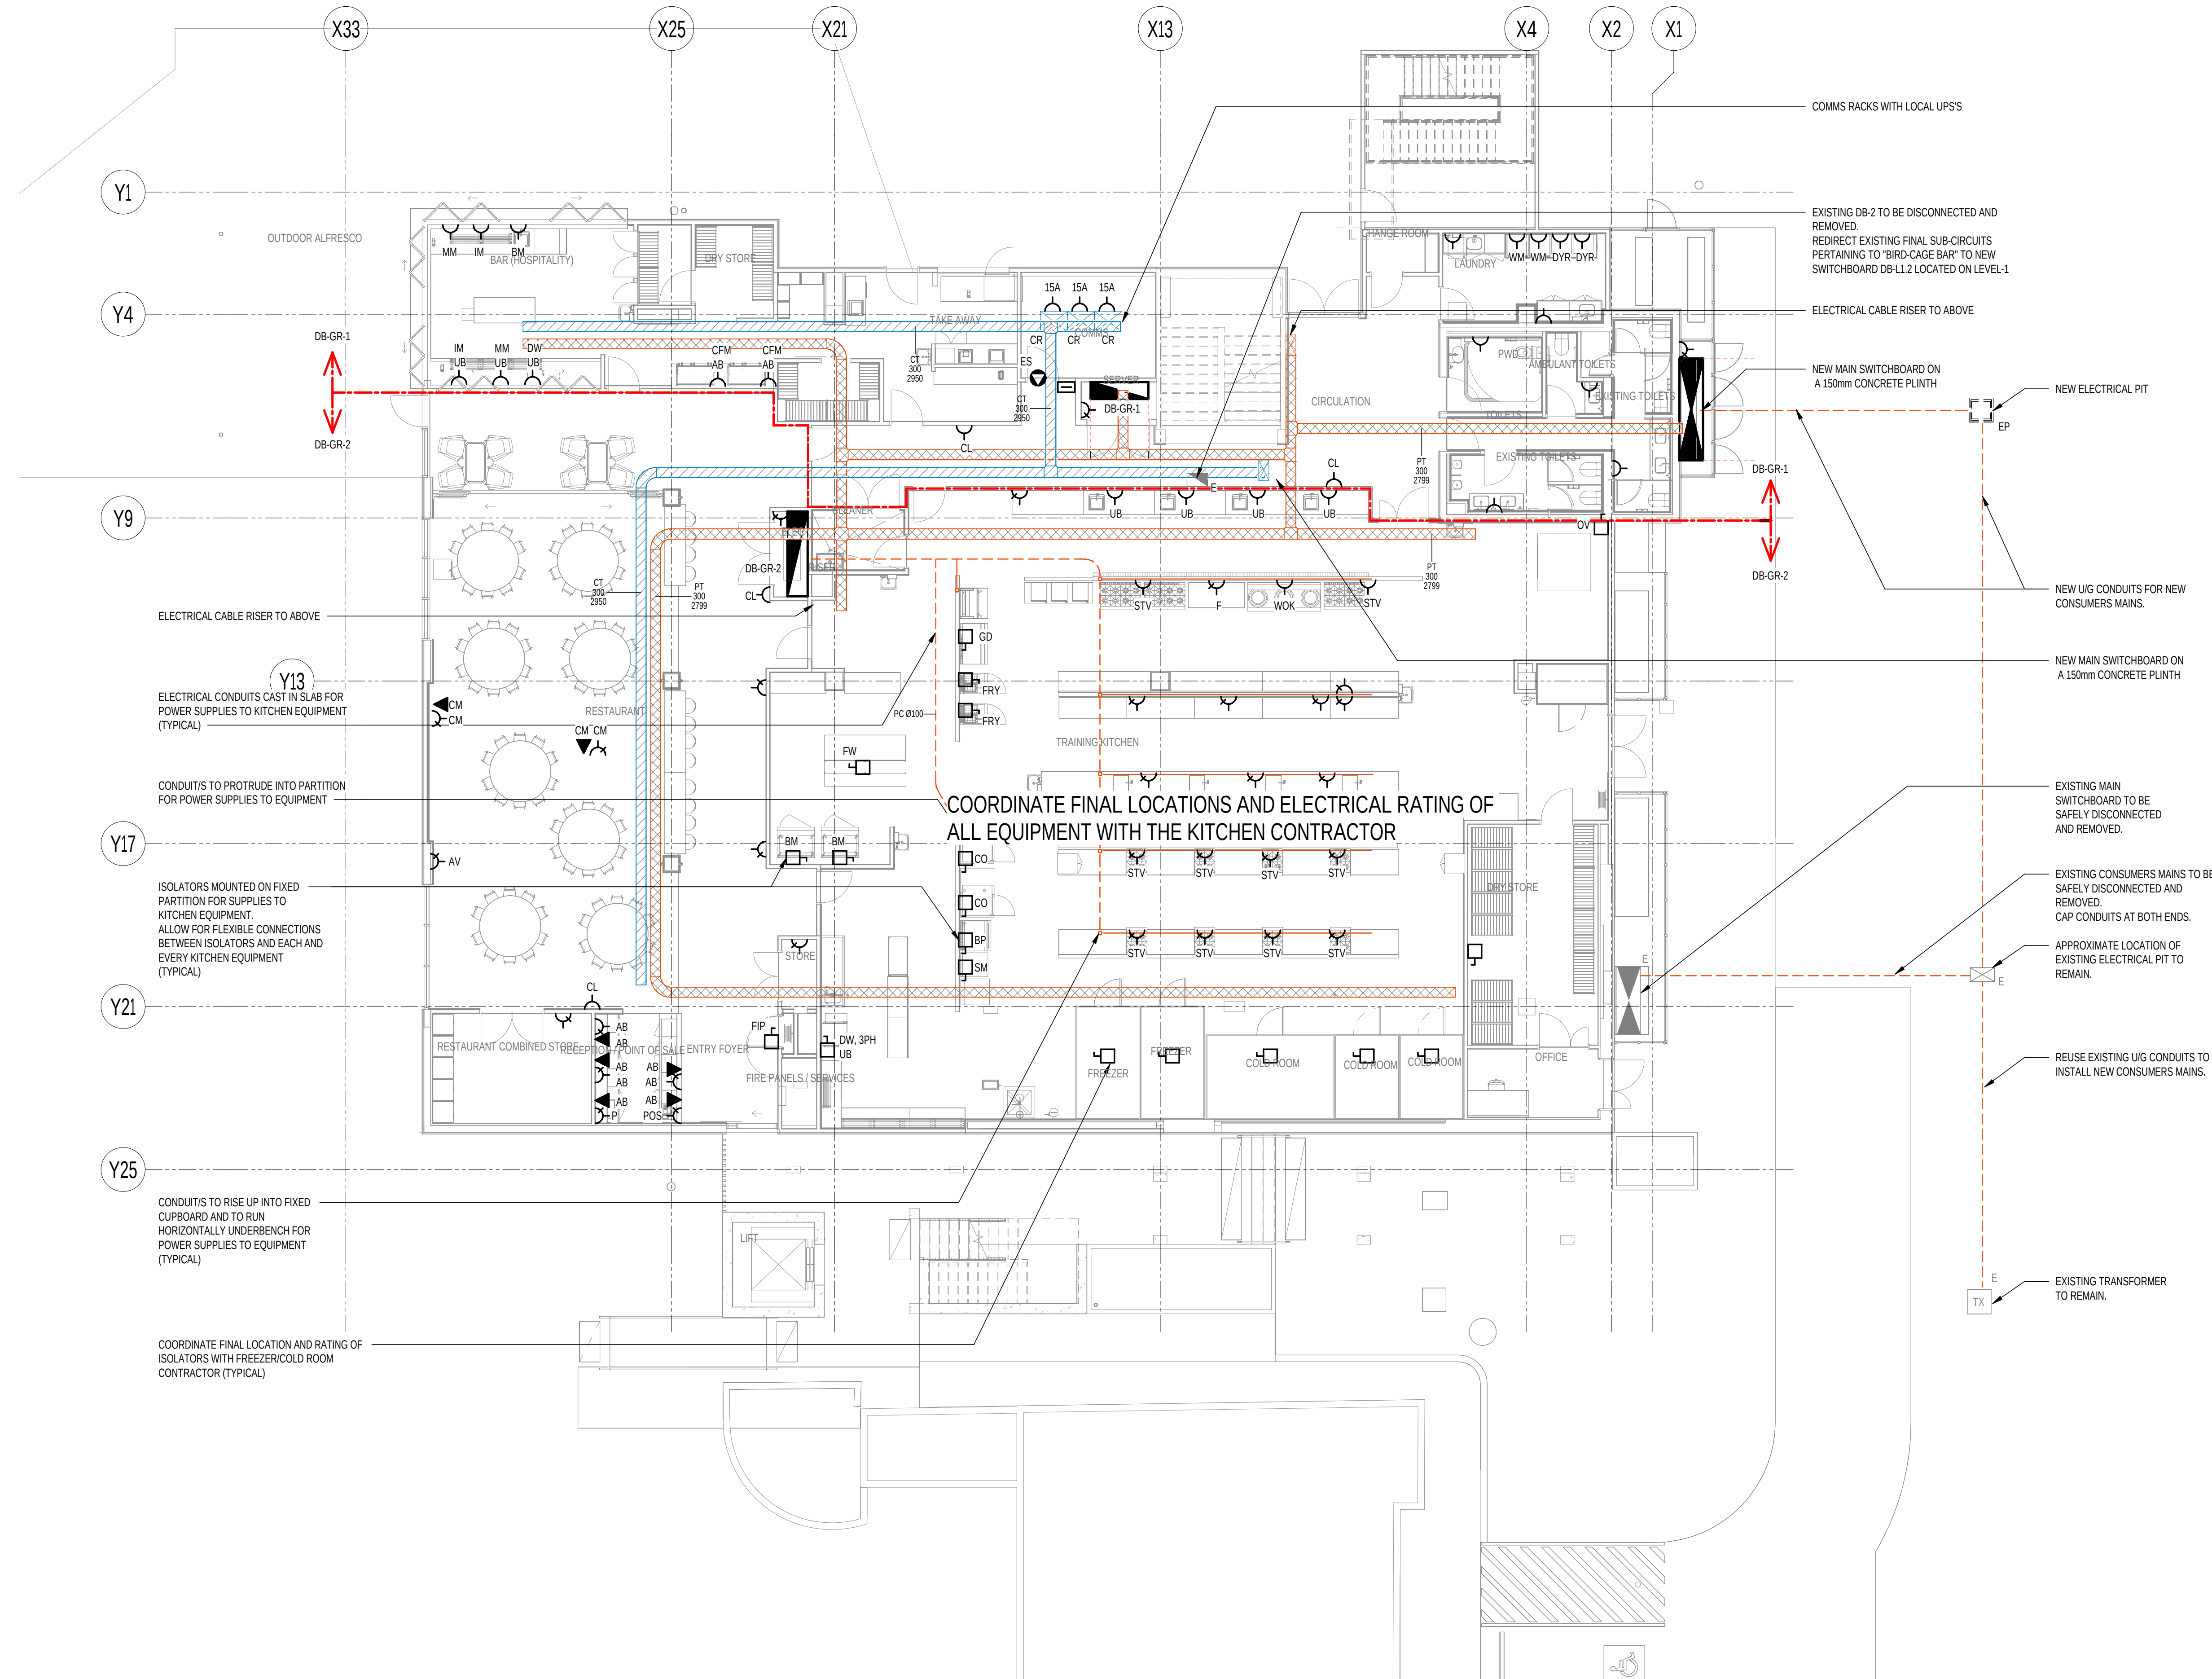

INFORMATION REFLECTED ON THIS DRAWING REPRESENTS ELECTRICAL SERVICES DESIGN DEVELOPED FOR D&C TENDER ADVISE ONLY, AND SHOULD NOT BE REGARDED AS COMPLETE. THE D&C CONTRACTOR SHOULD REFER TO ALL ASSOCIATED ARCHITECTURAL AND OTHER DISCIPLINE DRAWINGS, PROJECT BRIEFS AND CLIENT REQUIREMENTS AND MAKE ADEQUATE ALLOWANCES FOR ALL NECESSARY ELECTRICAL SERVICES WORKS TO MEET THESE REQUIREMENTS, EQUIPMENT SCHEDULES AND COMPLIANCE WITH THE NCC & APPROPRIATE AUSTRALIAN STANDARDS

B	12.02.2026	MM	ISSUED FOR D&C TENDER	TP	SM
A	16.02.2026	MM	ISSUED FOR D&C TENDER	TP	SM
REV	DATE	BY	DESCRIPTION	CHK	APP

DESIGN DEVELOPMENT

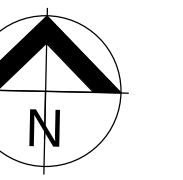

900 Ann Street, Level 12, Fortitude Valley 4006
Tel: +61-7-3854-6200 Fax: +61-7-3854-6500
<http://www.wsp.com>

CLIENT: CQU

ARCHITECT: THOMSON ADSETT / PEDDLE THORP

PROJECT: CQU ROCKHAMPTON TAFE CONSOLIDATION

TITLE: ELECTRICAL SERVICES
BUILDING 36 - GROUND LEVEL - POWER AND COMMS LAYOUT

SCALE @ A1	1:100	CHECKED	TP	APPROVED	SM
PROJECT NUMBER	PS229518	DRAWN	MM	DATE	JAN 2026

DRAWING NO:	B36-EL-DR-520-L00-00-00	REV:	B
-------------	-------------------------	------	---

© WSP Australia Pty Ltd