


INFORMATION REFLECTED ON THIS DRAWING REPRESENTS MECHANICAL SERVICES DESIGN DEVELOPED FOR D&C TENDER ADVICE ONLY, AND SHOULD NOT BE REGARDED AS COMPLETE. THE D&C CONTRACTOR SHOULD REFER TO ALL ASSOCIATED ARCHITECTURAL AND OTHER DISCIPLINE DRAWINGS, PROJECT BRIEFS AND CLIENT REQUIREMENTS AND MAKE ADEQUATE ALLOWANCES FOR ALL NECESSARY MECHANICAL SERVICES WORKS TO MEET THESE REQUIREMENTS, EQUIPMENT SCHEDULES AND COMPLIANCE WITH THE NCC & APPROPRIATE AUSTRALIAN STANDARDS

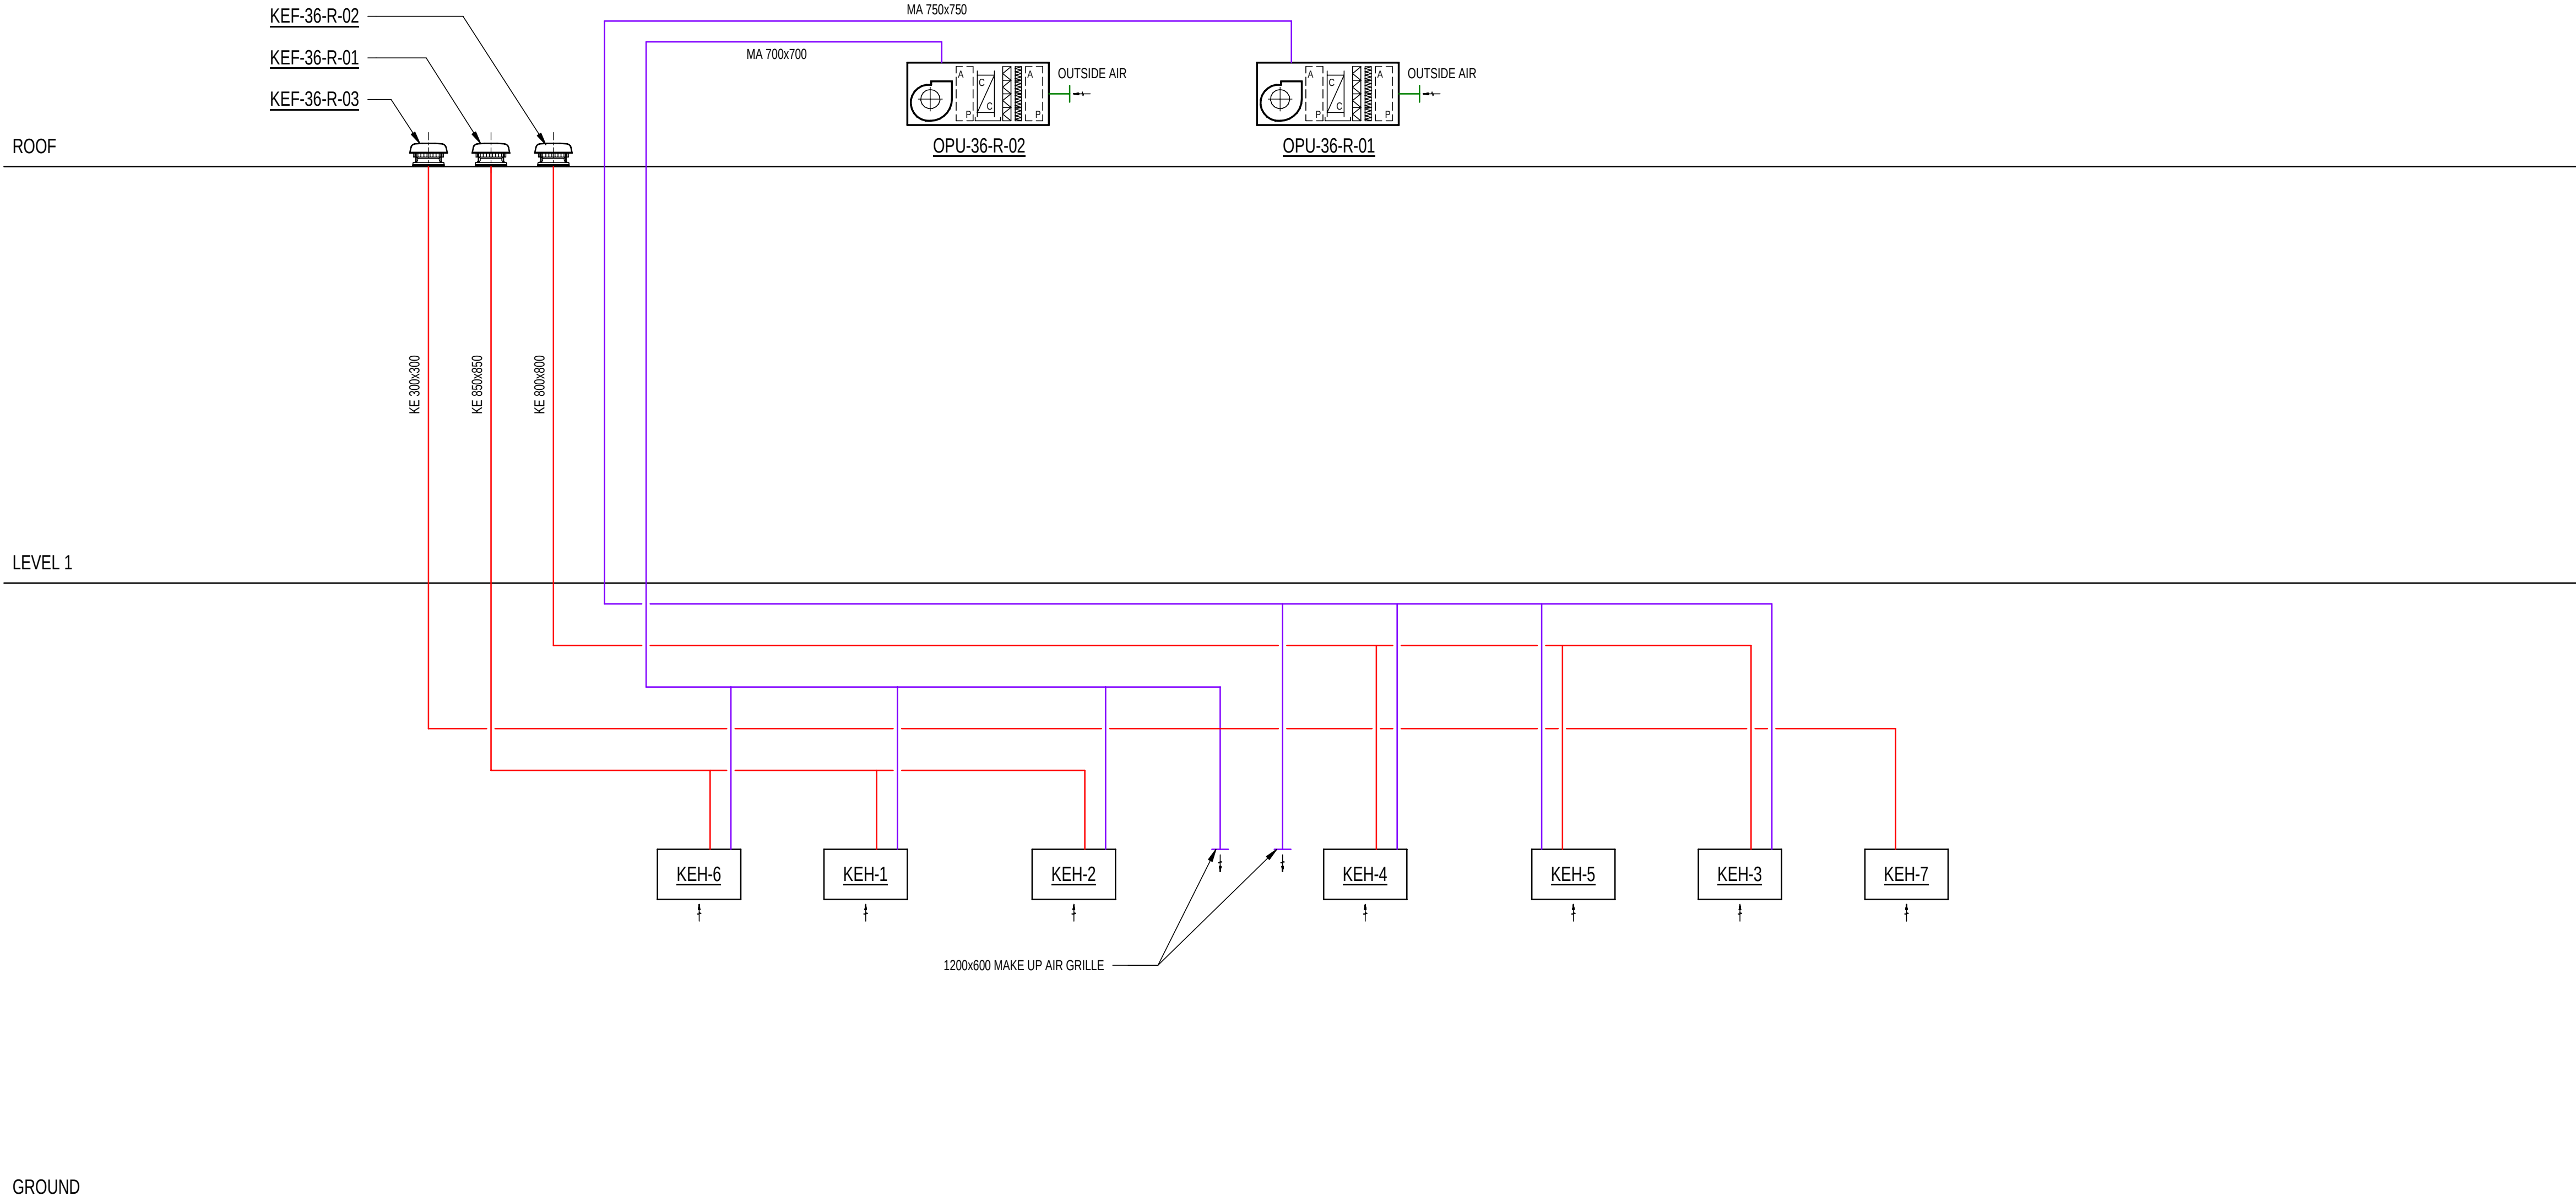

BUILDING 36 KITCHEN MAKE UP AIR SCHEMATIC
N.T.S.

A	12.02.2026	PD	ISSUED FOR D&C TENDER	MB	SM
REV	DATE	BY	DESCRIPTION	CHK	APP

DRAWING STATUS: DESIGN DEVELOPMENT

DESIGN DEVELOPMENT



900 Ann Street, Level 12, Fortitude Valley 4
Tel: +61-7-3854-6200 Fax: +61-7-3854-65
<http://www.wsp.com>

C

THOMSON ADSETT / PEDDLE THOR

CQU ROCKHAMPTON TAFE CONSOLIDATION

MECHANICAL SERVICES
MECHANICAL SERVICES - KITCHEN MAKE UP /
SCHEMATICS

SCALE @ A0: N.T.S.	CHECKED: MB	APPROVED: SM
PROJECT NUMBER: P5229518	DRAWN: RD	DATE: FEB 2026

DRAWING No:	REV:
00-ME-DR-210-A00-00-03	A

© WSP Australia Pty