


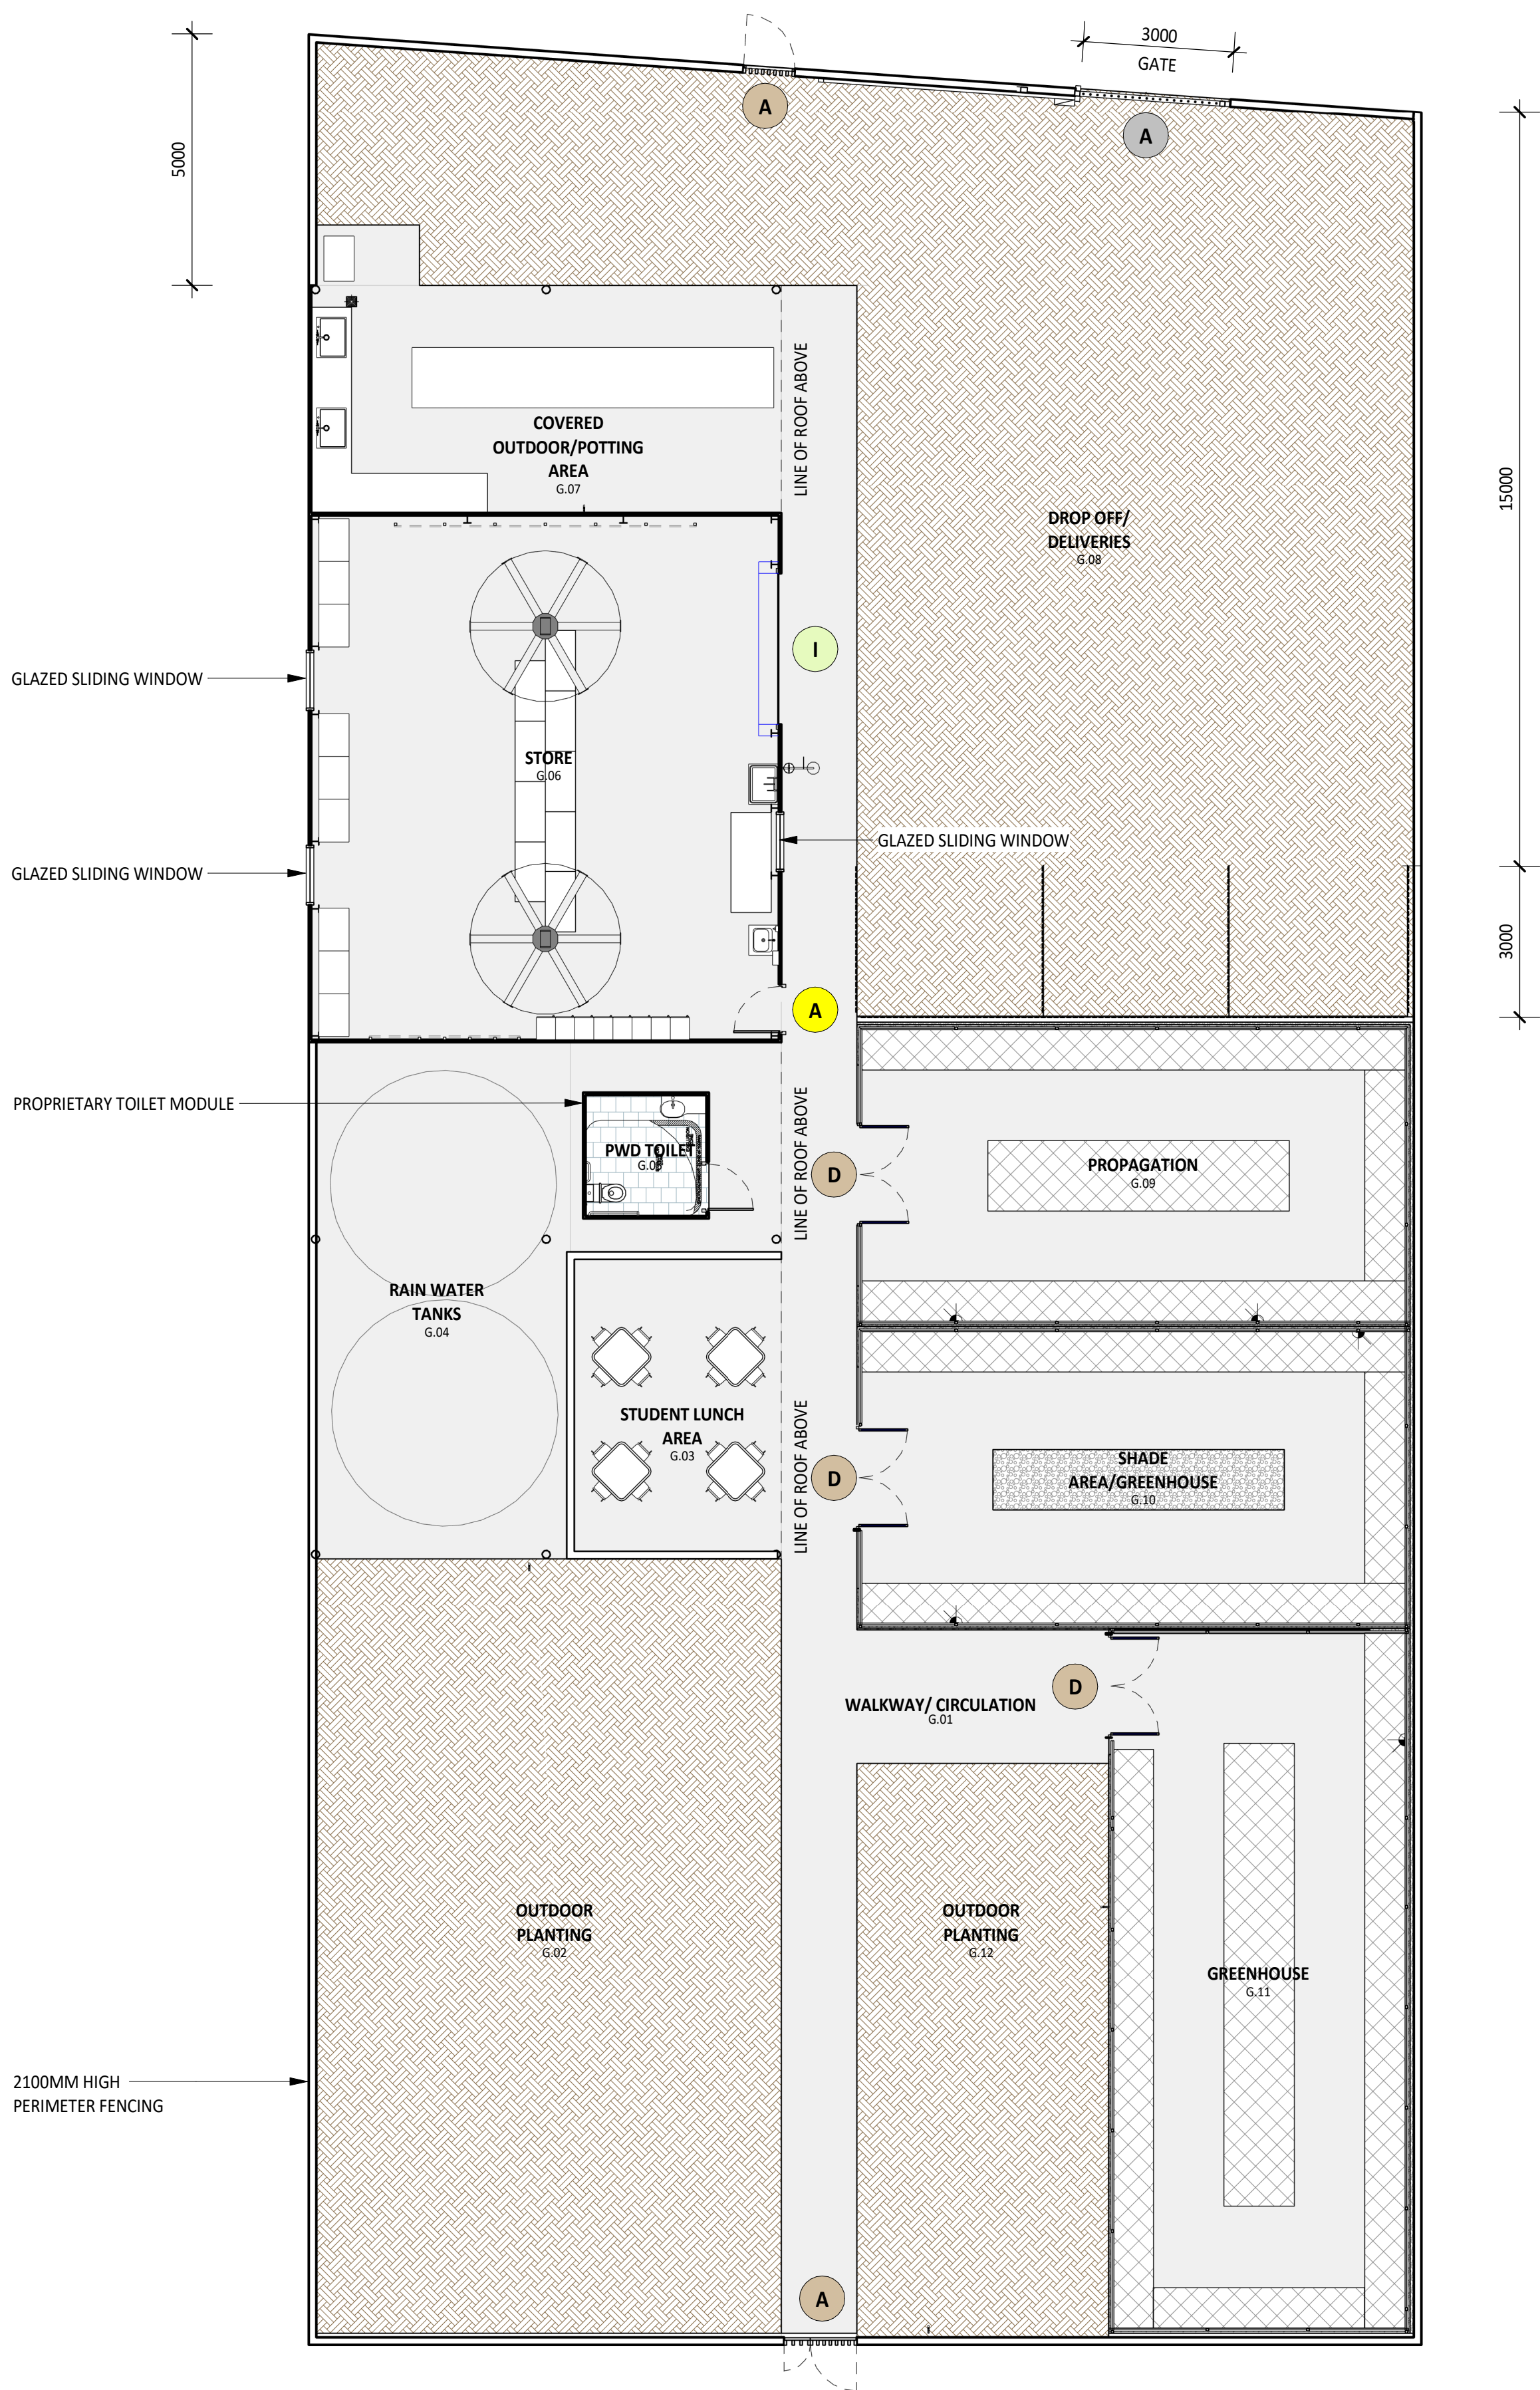

ACCESS TYPE	
A	CARD READER ACCESS
B	TURN SNIB (NO KEY)
C	PRIVACY SET & TURN SNIB
D	MORTICE LOCK & KEY CYLINDER
E	ROLLER DOOR LOCK
F	LEVER WITH COMPRESSION LOCKING MECHANISM
G	FREE LEVER ACCESS
H	PUSH & PULL ACCESS
I	ROLLER LATCH
J	FREE LEVER EGRESS
S	ROLLER SHUTTER INCLUDES SAFETY CHAIN TO BE HUNGWHEN SHUTTER IS HELD OPEN

DOOR TYPE	
XX	SOLID CORE DOOR
XX	GLAZED SLIDER DOOR
XX	VISION PANEL
XX	AUTO-SLIDER DOOR
XX	GLAZED-STACKER DOOR
XX	BIFOLD DOOR
XX	ROLLER DOOR
XX	ACOUSTIC STACKER DOOR
XX	GLAZED SWING DOOR
XX	SWING GATE
XX	SLIDING GATE - AUTOMATIC OPERATION
ALL DOORS TO HAVE MONITORED ELECTRIC STRIKE SWIPE CARD ACCESS, PLUS MASTERKEY LOCK AND CYLINDER. EXCEPTIONS ARE - MEETING ROOM DOORS - INCLUDE MASTERKEY LOCK AND CYLINDER, PLUS SNIB - NO SWIPE. ELECTRICAL CUPBOARDS - INCLUDE MASTERKEY LOCK AND CYLINDER - NO SWIPE OR SNIB	

ICON LEGEND	
XX	ACCESS TYPE (TYPE MARK)
XX	DOOR TYPE (COLOUR SHADE)

GENERAL NOTE	
- REFER TO MECHANICAL DRAWINGS FOR GRILLE AND UNDERCUT - ALL SERVICE DOORS TO HAVE SMOKE SEALS - FOR GLAZED DOORS REFER TO ROOM LAYOUT SHEET FOR EXTENT, WHICH NOTES SAFETY VISUAL GLAZING / PRIVACY SCREENING. - DOOR FUNCTION AND HARDWARE TO BE IN ACCORDANCE TO CQU GUIDELINES. - ANY DOOR ACCESS TO BATHROOM TO HAVE STAINLESS STEEL KICKPLATE - ALLOW FOR DOOR CLOSERS AND DOOR STOPS TO DOORS - EXTERNAL DOORS TO BE MANUALLY OPERATED, OPENING OUTWARDS. ENSURE THIS COMPLIES WITH AS 1428.1 - FIRE RATED DOORS TO HAVE PUSH BAR FOR EXIT. - SINGLE SWING DOORS FOR CIRCULATION ACCESS TO BE 920MM WIDE, UNLESS SPECIFIED - ALL EXTERNAL DOORS, LECTURE THEATRE DOORS, PLANT ROOMS, TOILET DOORS, FIRES DOORS AND EMERGENCY EXIT TO HAVE AUTO-CLOSER DOORS - CQU TO CONFIRM ACCESS REQUIREMENT TO OFFICES AND CLASSROOMS - EXTERNALLY LOCKED DOORS TO HAVE STRIKER PLATE PROTECTION INSTALLED - REFER TO CQU DESIGN GUIDELINES FOR DESIGN AND CONSTRUCTION REQUIREMENTS. - REFER TO ROOM LAYOUT SHEET FOR EXTENT OF WORK. - DRAWINGS TO BE READ IN CONJUNCTION WITH SERVICES, CIVIL AND STRUCTURAL DRAWINGS. - ALL EXTERNAL DOORS TO HAVE REED SWITCH	

ISSUED FOR TENDER

© Copyright
These drawings and designs and the copyright thereof are the property of Thomson Adsett Pty Ltd and must not be used, retained or copied without written permission of Thomson Adsett Pty Ltd. ABN 76 105 314 654 Trading as ThomsonAdsett. Dimensions take precedence over scaling. Do not measure off drawings as print sizes may vary

CQU ROCKHAMPTON TAFE

554/700 Yaamba Rd, Norman Gardens QLD 4701



A	12/02/26	ISSUED FOR TENDER	BS
4	30/01/26	DRAFT 60% ISSUE	BS
3	23/01/25	COORDINATION ISSUE FOR CONSULTANTS	KM
2	19/12/25	ISSUED FOR COORDINATION	KM
1	16/12/25	FROZEN ISSUE	KM
rev	date	details	init.

drawn	date
PT	19/12/25
checked	date
BS	19/12/25
verified	date
BS	19/12/25

scale

HORTICULTURE FLOOR PLAN

scale	project no.
1 : 100 @ A1	260018
revision	
A	
sheet no.	
CQU-ROK-076-GN-ARC-21-00	