




CQU ROCKHAMPTON TAFE

554/700 Yaamba Rd, Norman Gardens QLD 4701

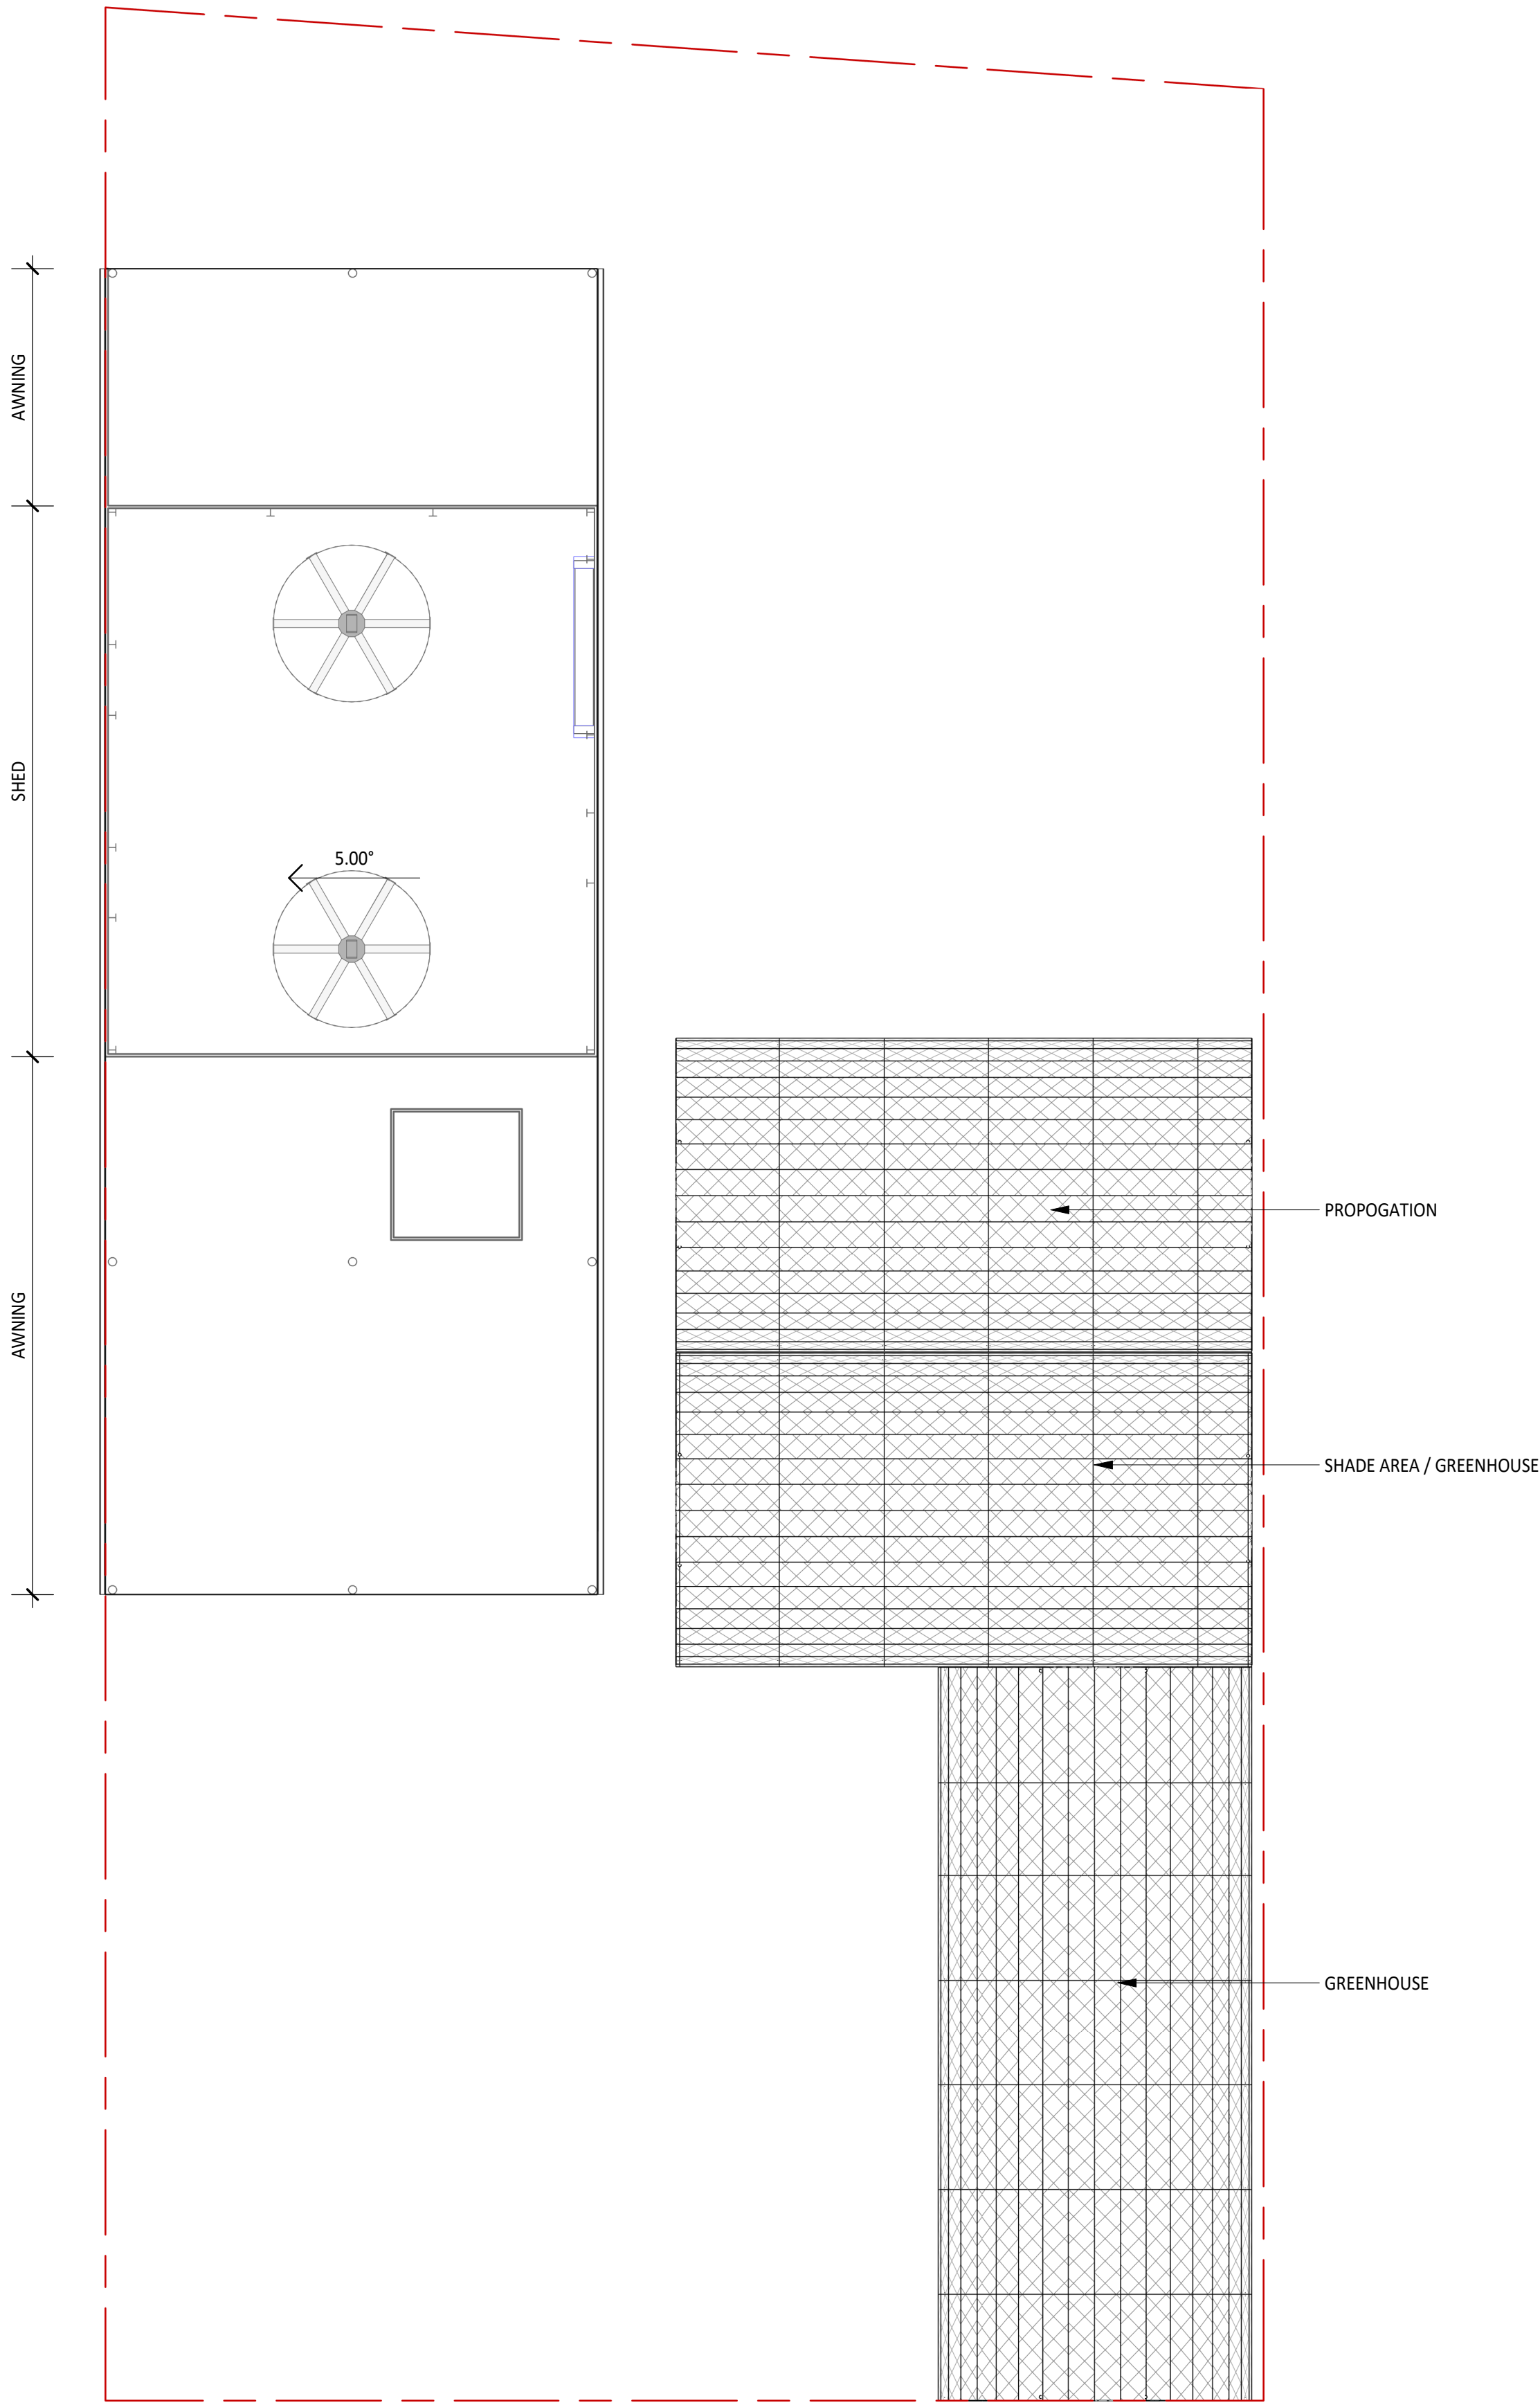

A	12/02/26	ISSUED FOR TENDER	BS
3	30/01/26	DRAFT 60% ISSUE	BS
2	19/12/25	ISSUED FOR COORDINATION	KM
1	16/12/25	FROZEN ISSUE	KM

rev	date	details	init.
-----	------	---------	-------

drawn	date
PT	19/12/25
checked	date
BS	19/12/25
verified	date
BS	19/12/25

scale

HORTICULTURE ROOF PLAN

scale project no.
1 : 100 @ A1 260018
revision
A
sheet no.
CQU-ROK-076-RF-ARC-21-20

ISSUED FOR TENDER