



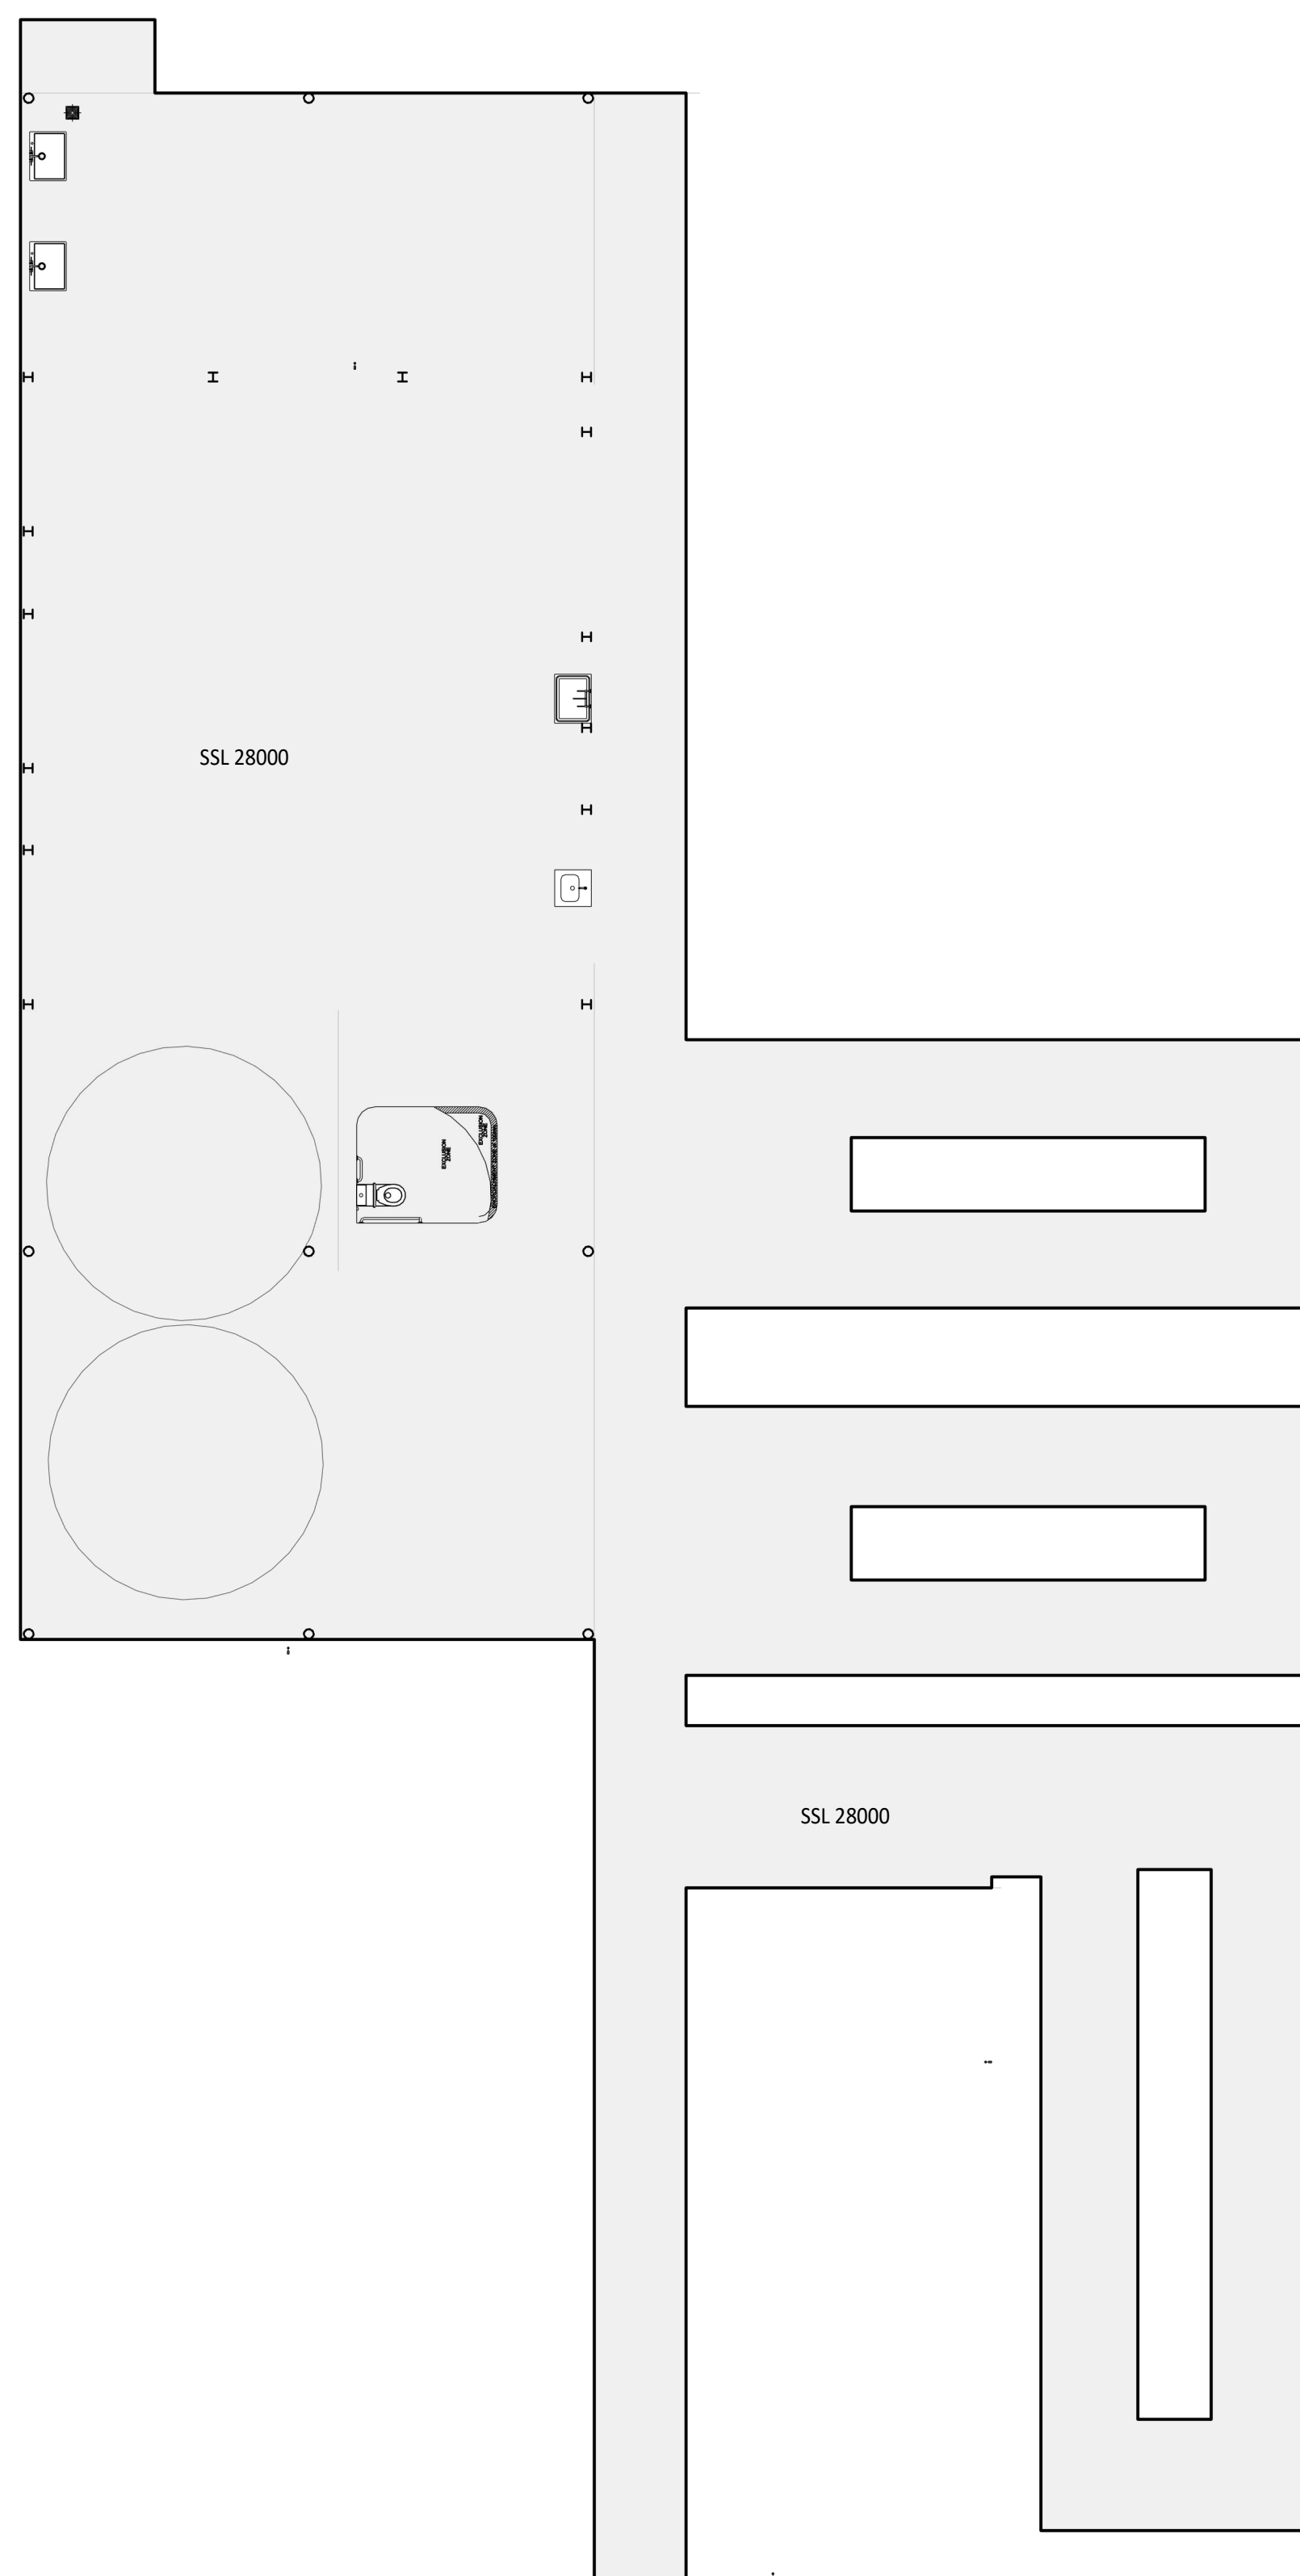


WATERPROOFING LEGEND

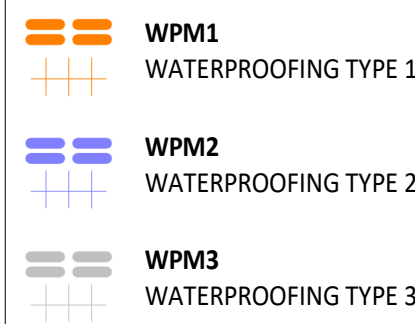

UNLESS NOTED OTHERWISE FLOORS WITH WATERPROOFING TO
HAVE MEMBRANE COVERED TO MINIMUM 150 AFFL

WALL SETOUTS

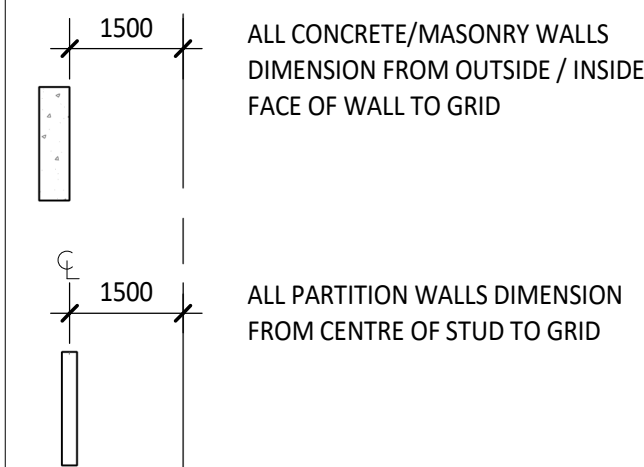

ISSUED FOR TENDER



PEDDLE THORP
architecture | interiors | health | planning

Telephone +61 7 3840 9999
bne@thomsonadsett.com
Level 9, 470 St Pauls Terrace
Fortitude Valley
Qld 4006 Australia
thomsonadsett.com

© Copyright

These drawings and designs and the copyright thereof are the property of Thomson Adsett Pty Ltd and must not be used, retained or copied without written permission of Thomson Adsett Pty Ltd. ABN 76 105 314 654 Trading as ThomsonAdsett. Dimensions take precedence over scaling. Do not measure off drawings as print sizes may vary

**CQU ROCKHAMPTON
TAFE**

554/700 Yaamba Rd, Norman
Gardens QLD 4701


for



A	12/02/26	ISSUED FOR TENDER	BS
1	19/12/25	ISSUED FOR COORDINATION	KM
rev	date	details	init.

drawn	date
PT	19/12/25
checked	date
BS	19/12/25
verified	date
BS	19/12/25

scale

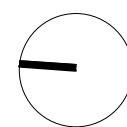

STRUCTURAL SETOUT PLAN GROUND LEVEL

scale project no.
1 : 100 @ A1 260018

revisor

A

sheet no.

CQU-ROK-076-GN-ARC-23-01

original sheet size - A1 (594mm x 841mm)

Autodesk Docs://CQU ROK TAFE/260018_A_CQ-UNIVERSITY BLD-HC R25.nt