



AREA OF WORKS HAS A SITE SOIL CLASSIFICATION OF "H1"
IN ACCORDANCE WITH AS2870. FOR FURTHER INFORMATION
REFER TO GEOTECHNICAL REPORT (BY OTHERS)

- NOTES
1. EXPANSION JOINT WRAPPED IN A SUITABLE MATERIAL TO ALLOW FULL MOVEMENT AND TO PREVENT THE INGRESS OF FOREIGN MATTER. MINIMUM TRAVEL: "H1" 50mm
 2. ARTICULATION JOINT WRAPPED IN A SUITABLE MATERIAL TO ALLOW FULL MOVEMENT AND TO PREVENT THE INGRESS OF FOREIGN MATTER. INSTALLED TO MANUFACTURERS SPECIFICATIONS.
 3. IF VERTICAL DROP GREATER THAN 100mm THEN EXPANSION JOINT TO BE INSTALLED.
 4. PIPEWORK GRADED AT MINIMUM 1:60 FOR A MINIMUM DISTANCE OF 300mm DOWNSTREAM OF EXITING STRUCTURAL SLAB.
 5. ALL TRENCHING TO BE GRADED UNIFORMLY WITH PIPEWORK TO ENSURE TRENCH DRAINAGE.
 6. EXPANSION AND SWIVEL JOINT DOWNSTREAM OF EVERY JUNCTION (TYPICAL) & CHANGE IN DIRECTION (>45°). FOR H1 SITES, A COMBINATION SWIVEL/EXPANSION JOINT MAY BE UTILISED.
 7. COMPACTED CLAY SOILS OR EQUIVALENT IN TRENCH TO FORM IMPERMEABLE "PLUG" TO PREVENT THE INGRESS OF WATER THROUGH TRENCHING AS PER AS2870.
 8. THIS ARTICULATION DESIGN HAS BEEN PREPARED IN CONJUNCTION WITH MANUFACTURER AND INDUSTRY INFORMATION, TO SATISFY THE REQUIREMENTS OF THE PLUMBING AND DRAINAGE REGULATION 2013 SCHEDULE 6.
 9. THIS DETAIL SHALL BE FULLY COMPLIED WITH IN REGARDS TO CONTRACTOR INSTALLATION, UNLESS WRITTEN APPROVAL IS PROVIDED BY WSP CERTIFYING ENGINEER OR THEIR APPROVED REPRESENTATIVE.

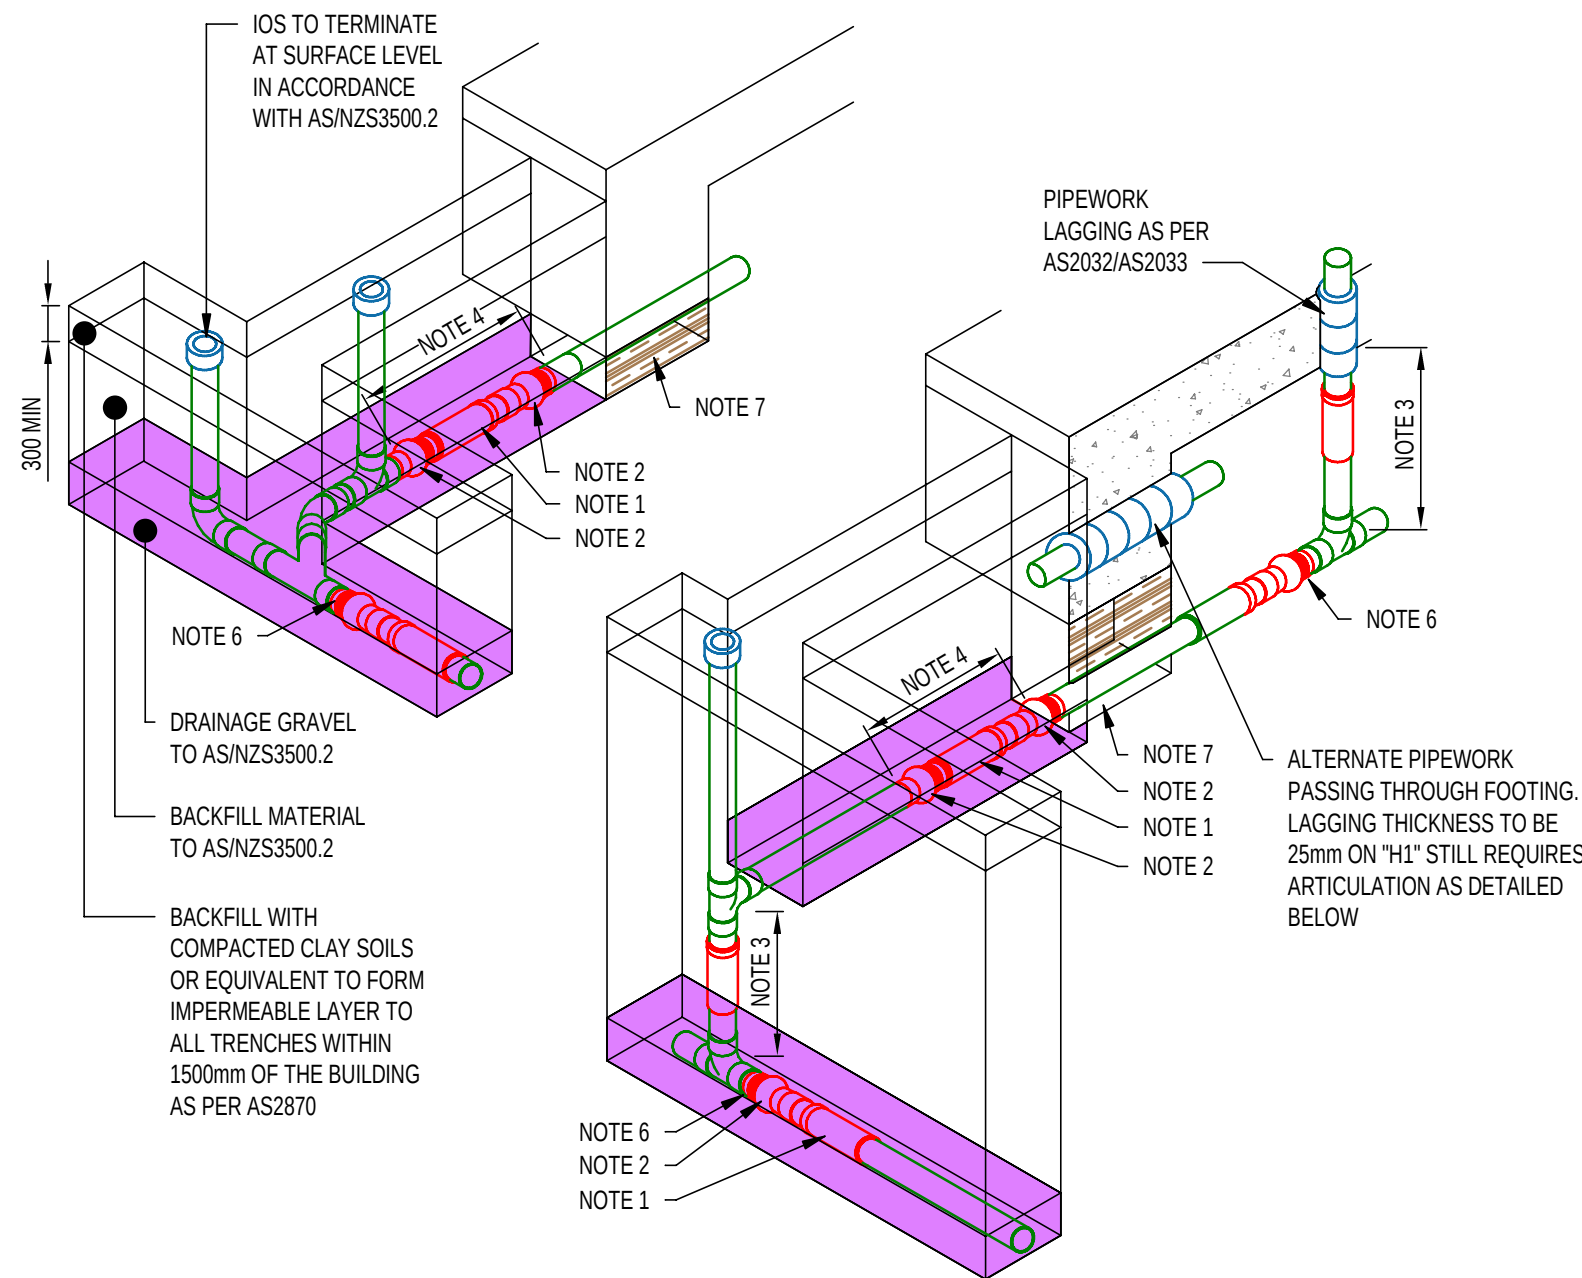


1 IN GROUND DRAINAGE (STORMWATER & SANITARY)
N.T.S.

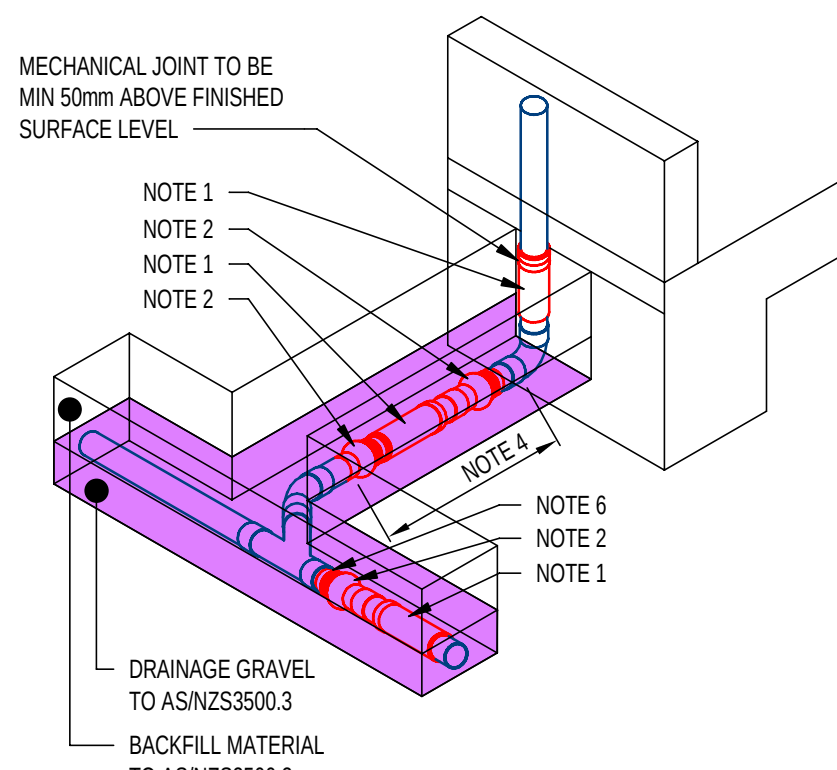


2 STORMWATER DOWNPIPES
N.T.S.


FLEXIBLE DRAINAGE DETAIL N.T.S.

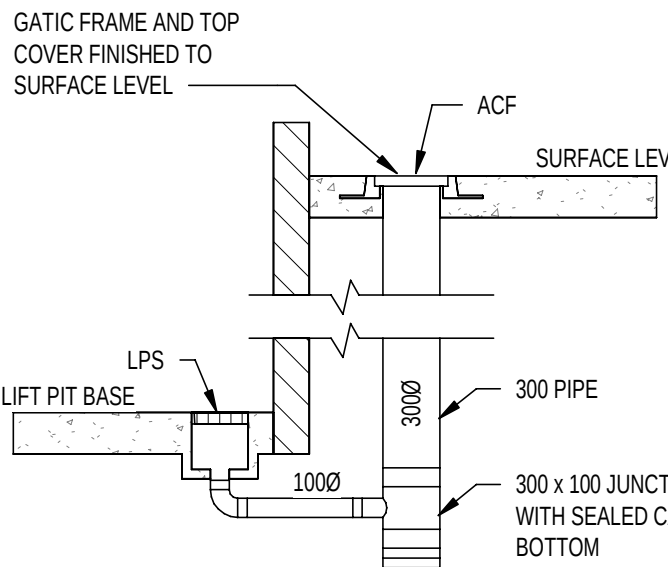


LIFT SUMP DRAINAGE N.T.S.

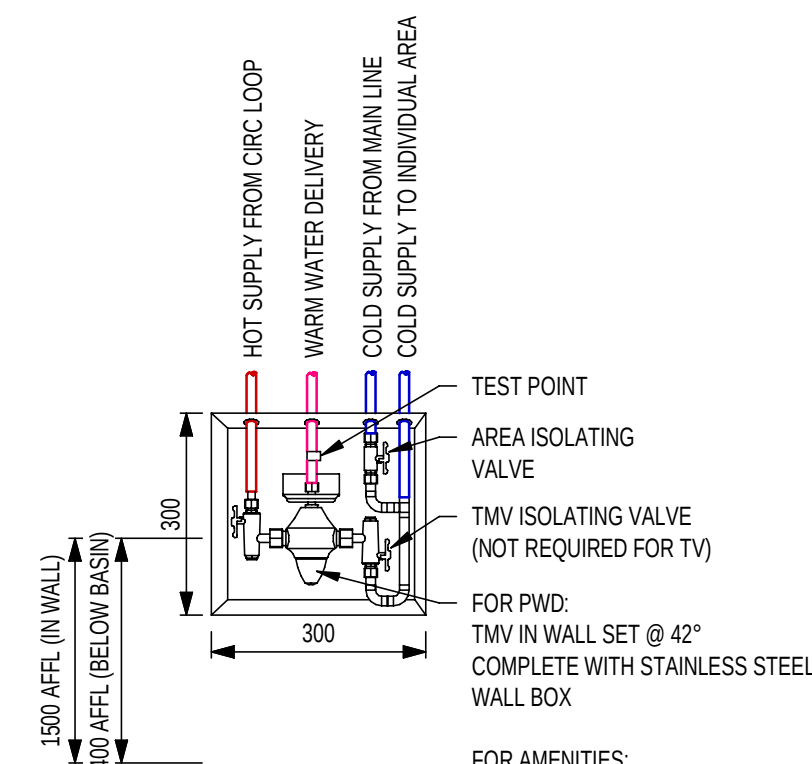


TMV DETAIL N.T.S.

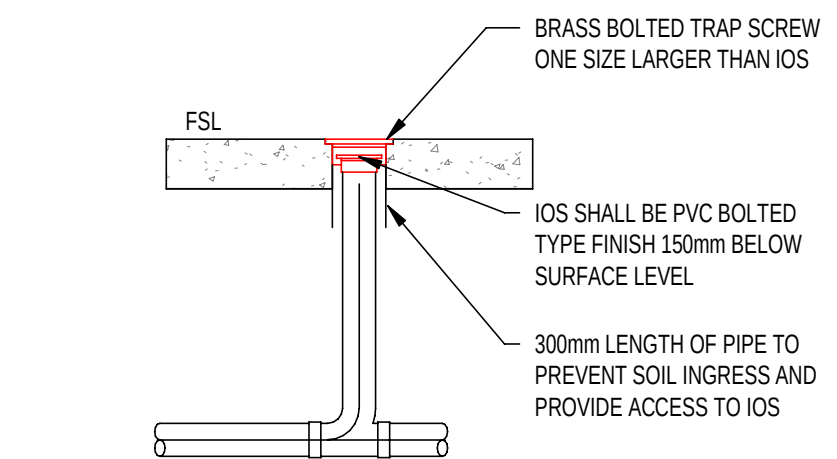


TRAFFICABLE IOS N.T.S.

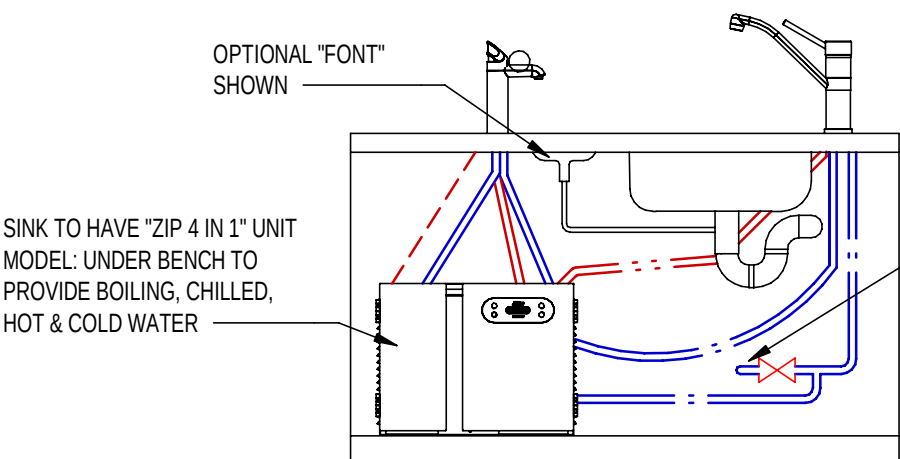


ZIP 4 IN 1 UNDER BENCH MODEL BOILING, CHILLED, HOT & COLD N.T.S.

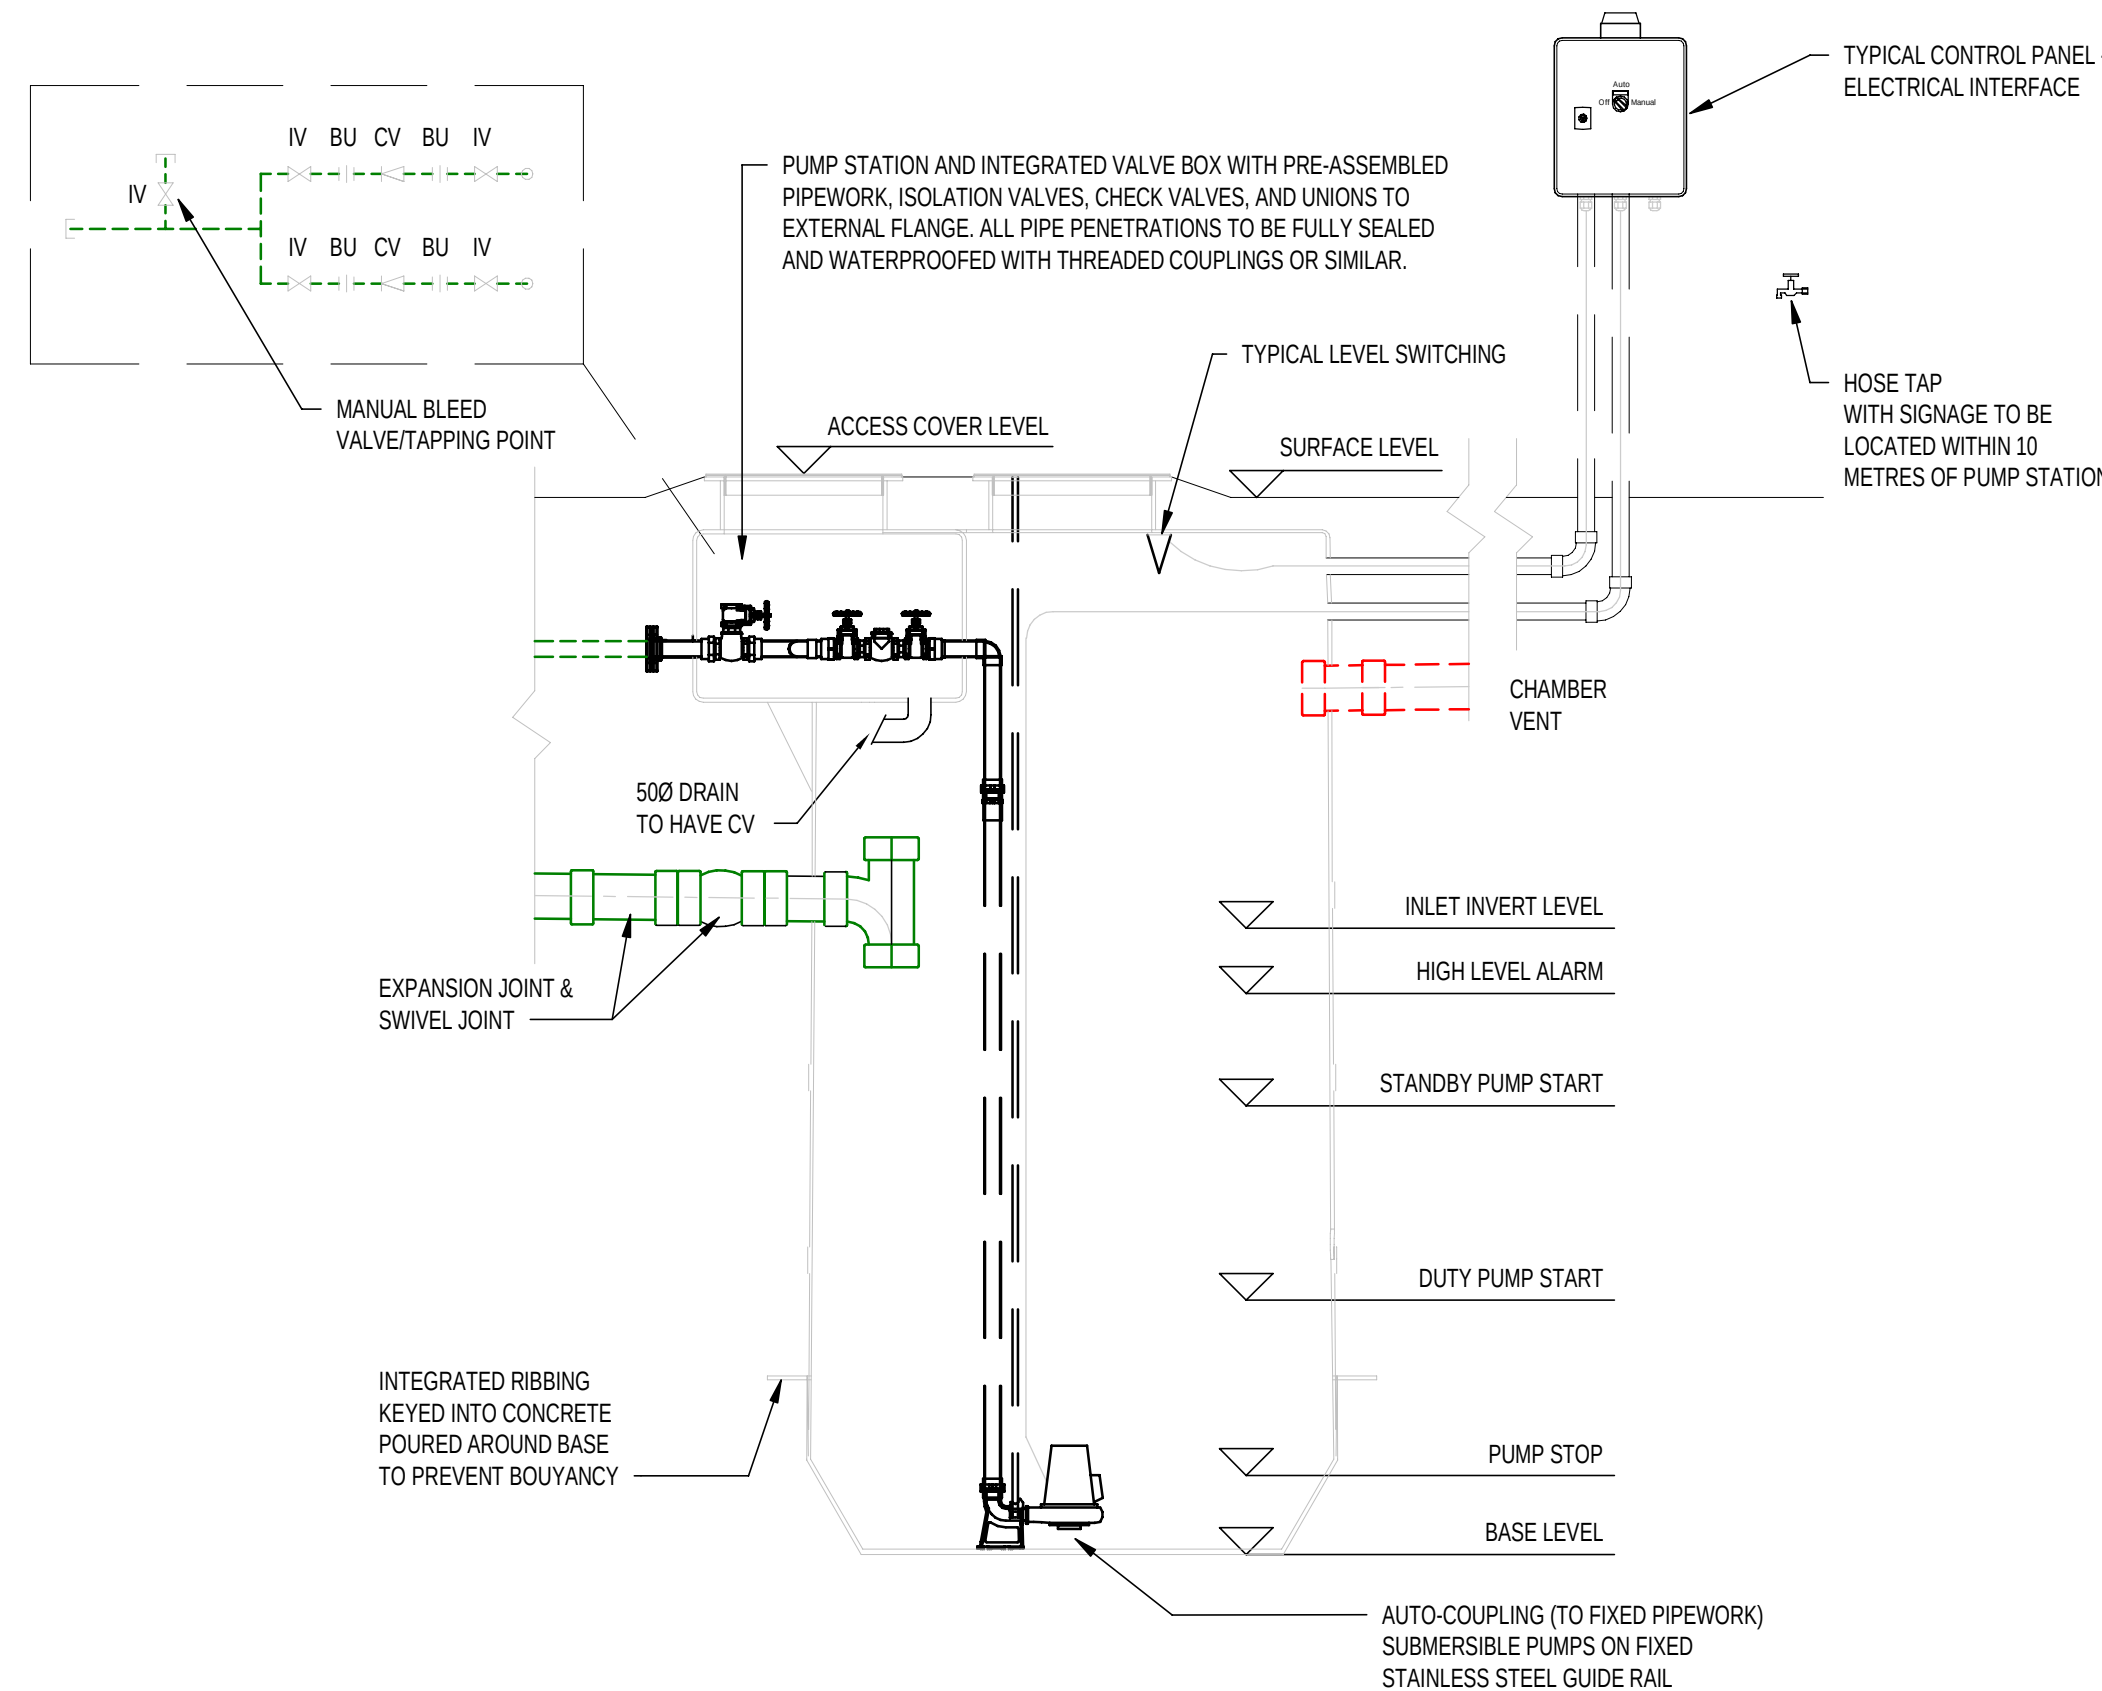


PACKAGED SANITARY DRAINAGE PUMP STATION DETAIL N.T.S.

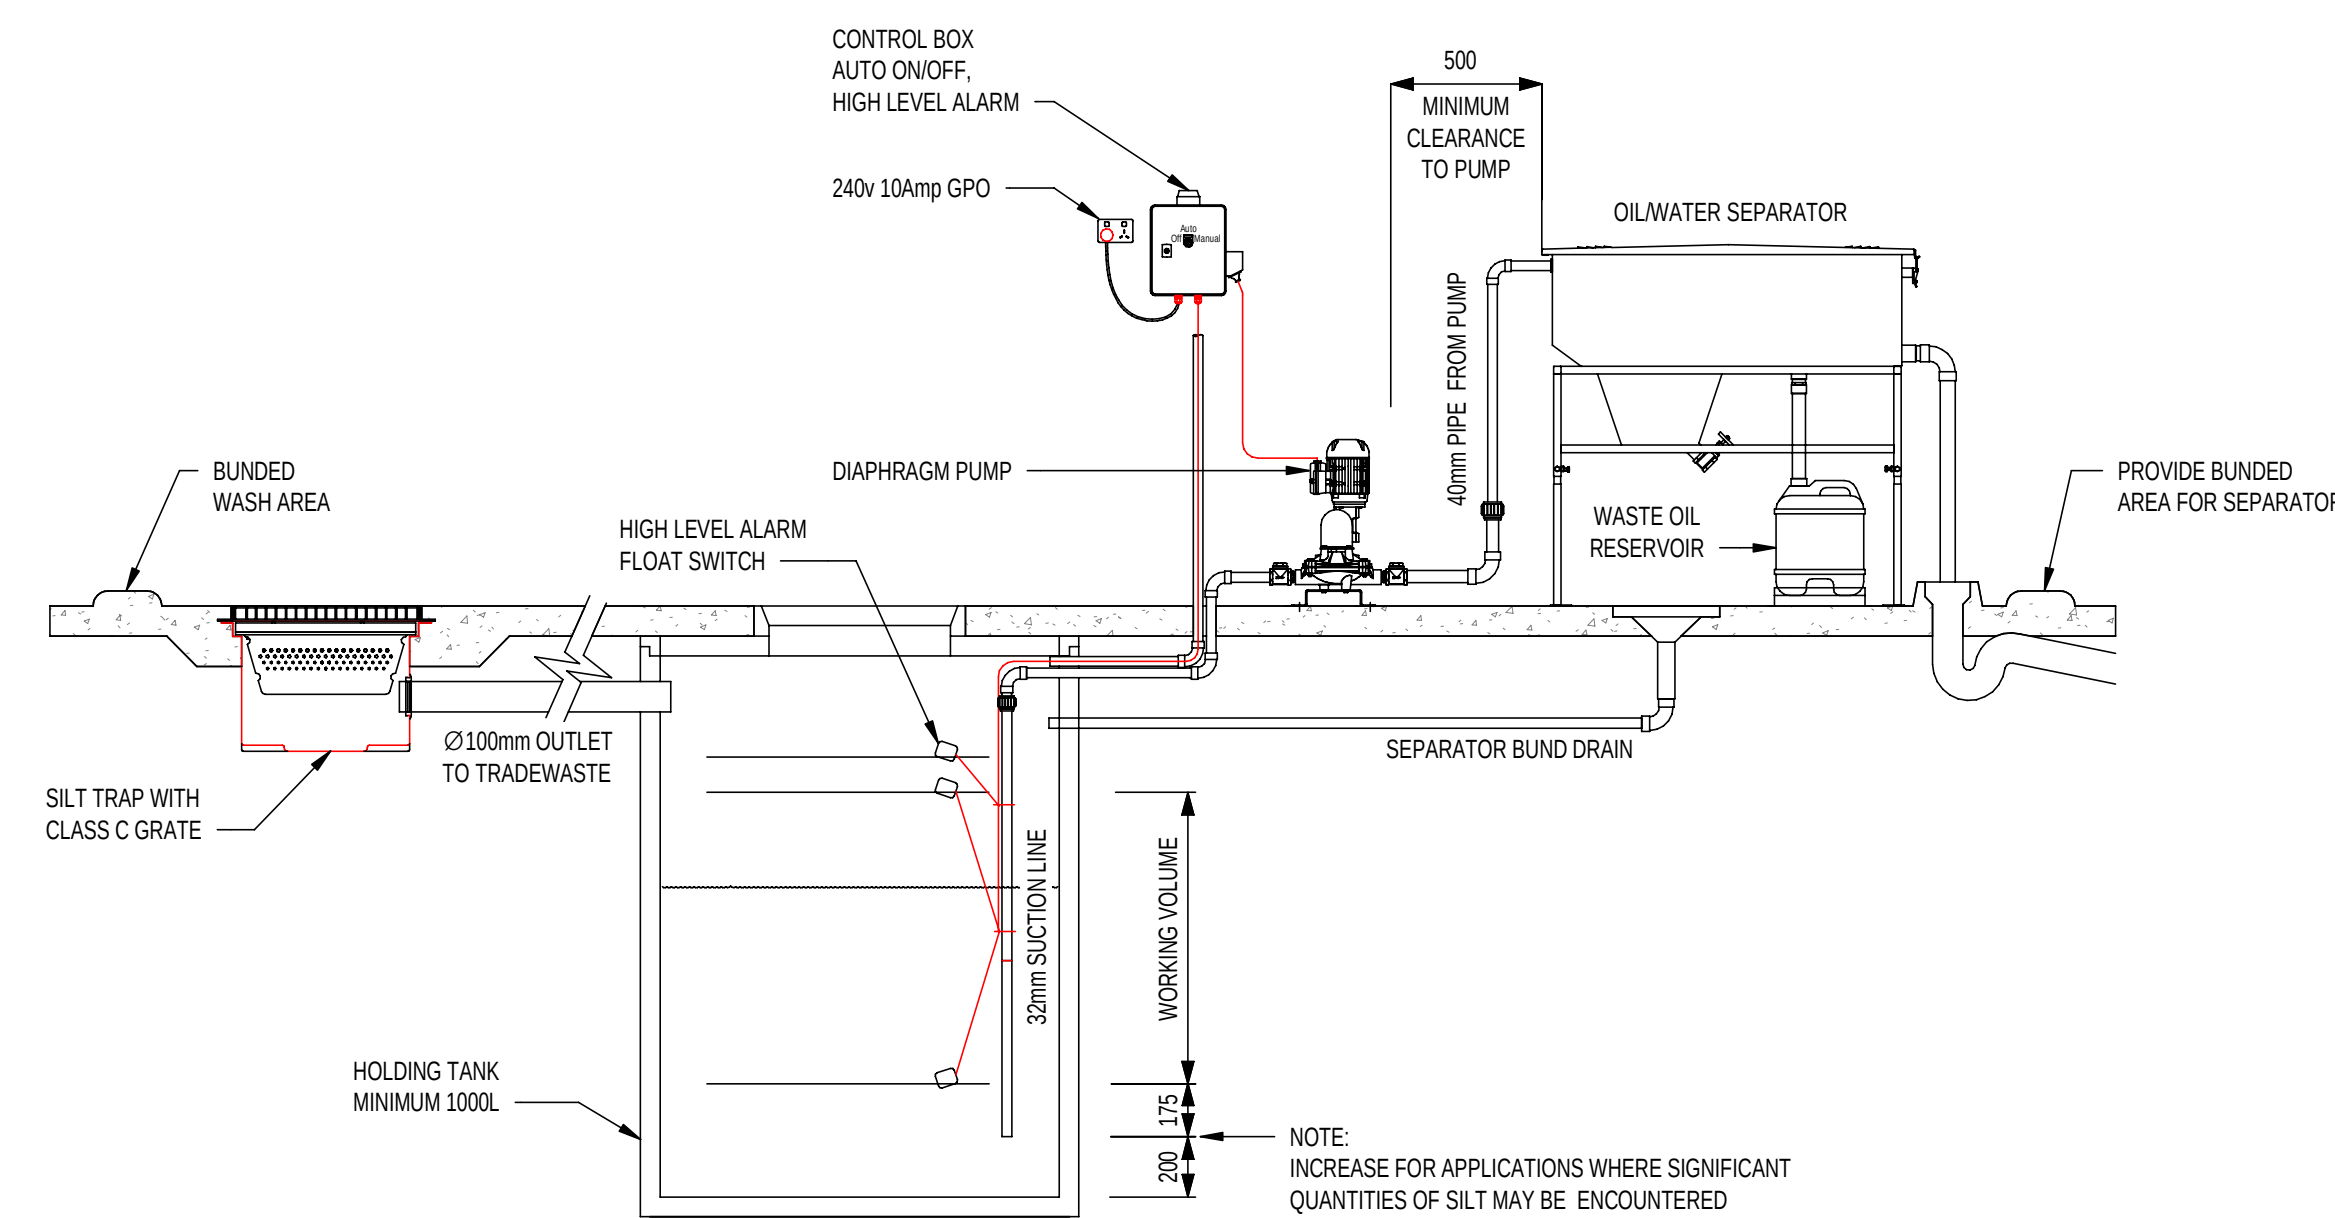


OIL/WATER SEPARATOR DETAIL N.T.S.

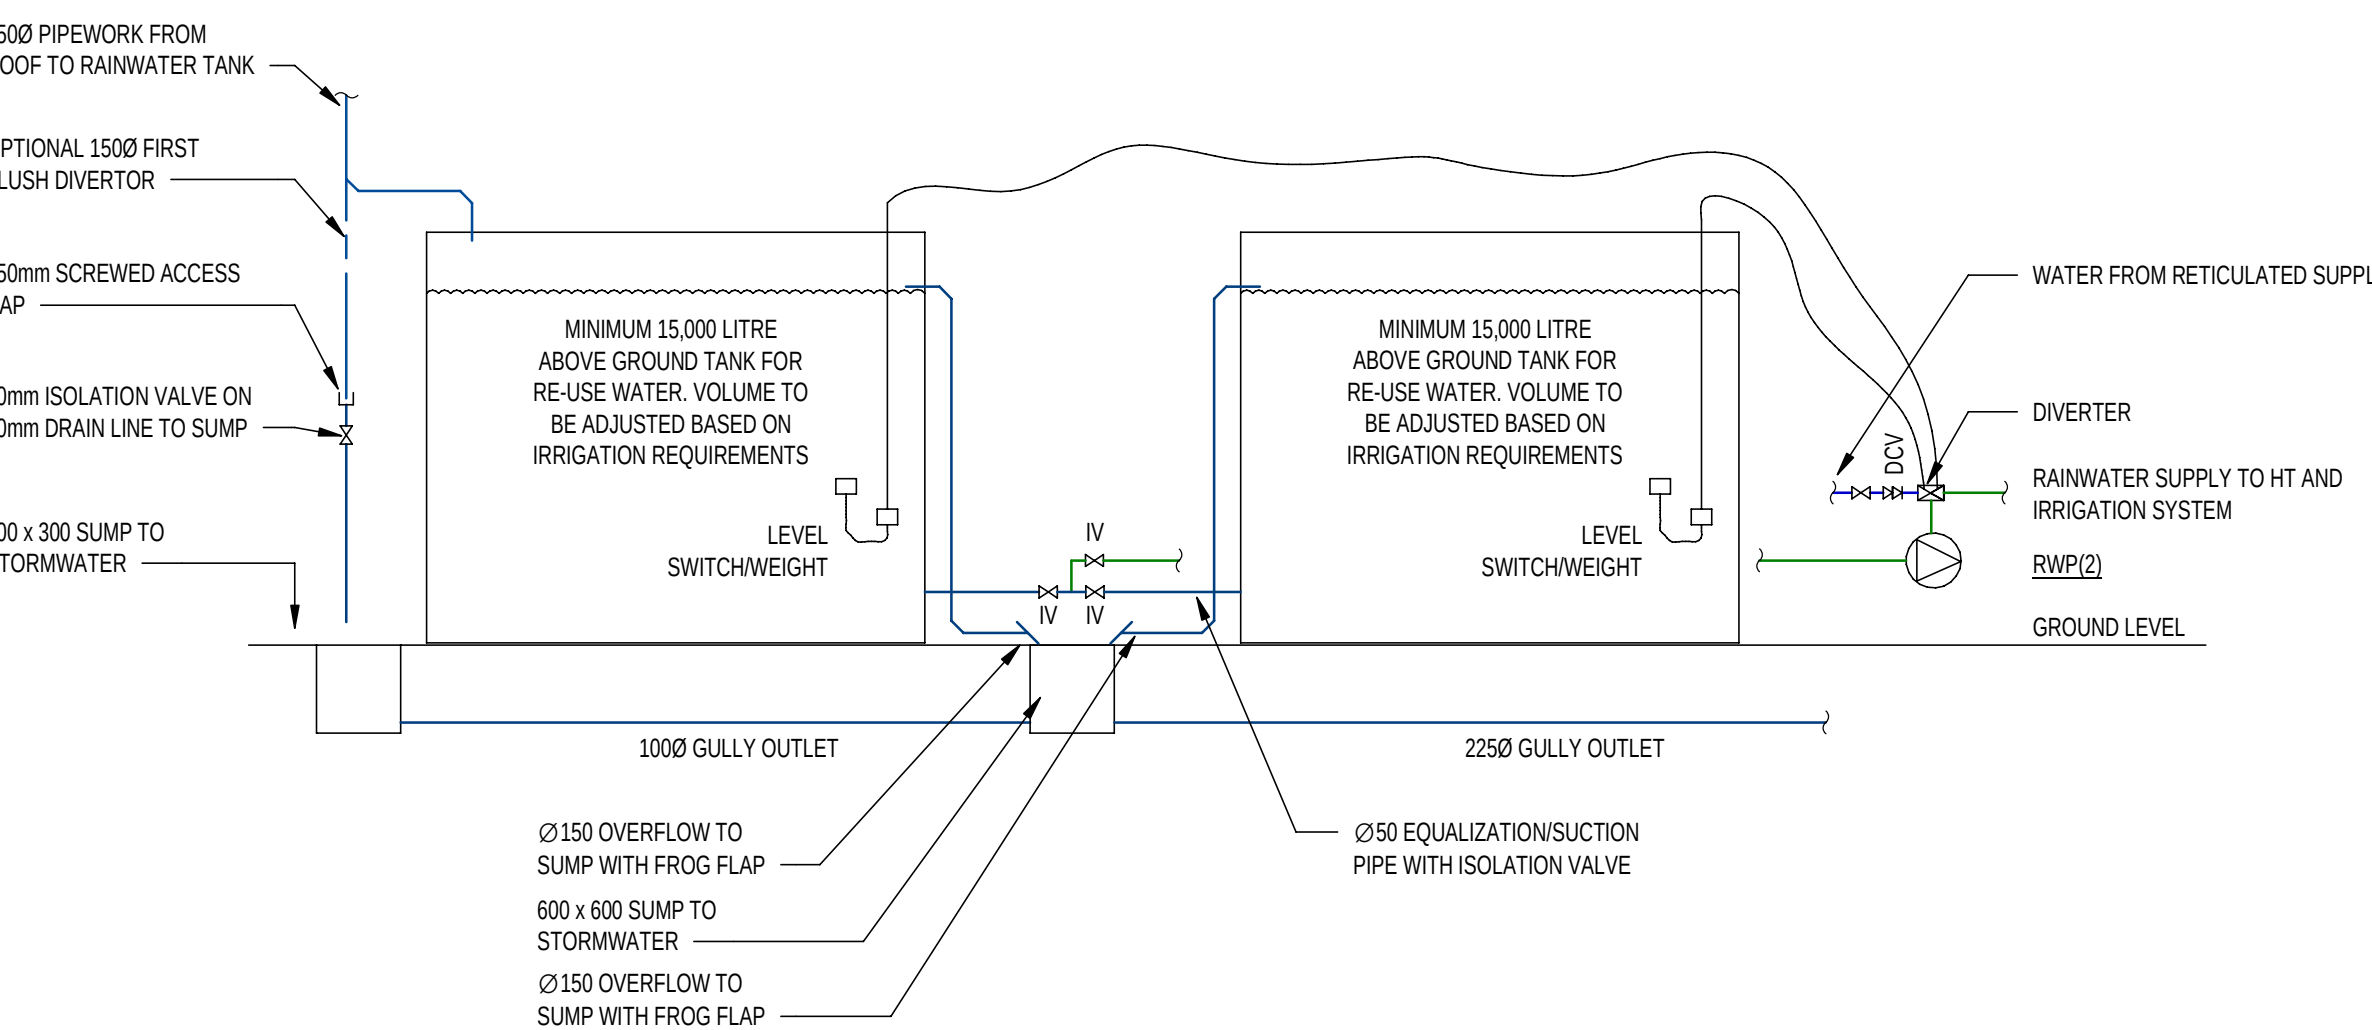


RAINWATER TANK DETAIL - HORTICULTURE BUILDING N.T.S.

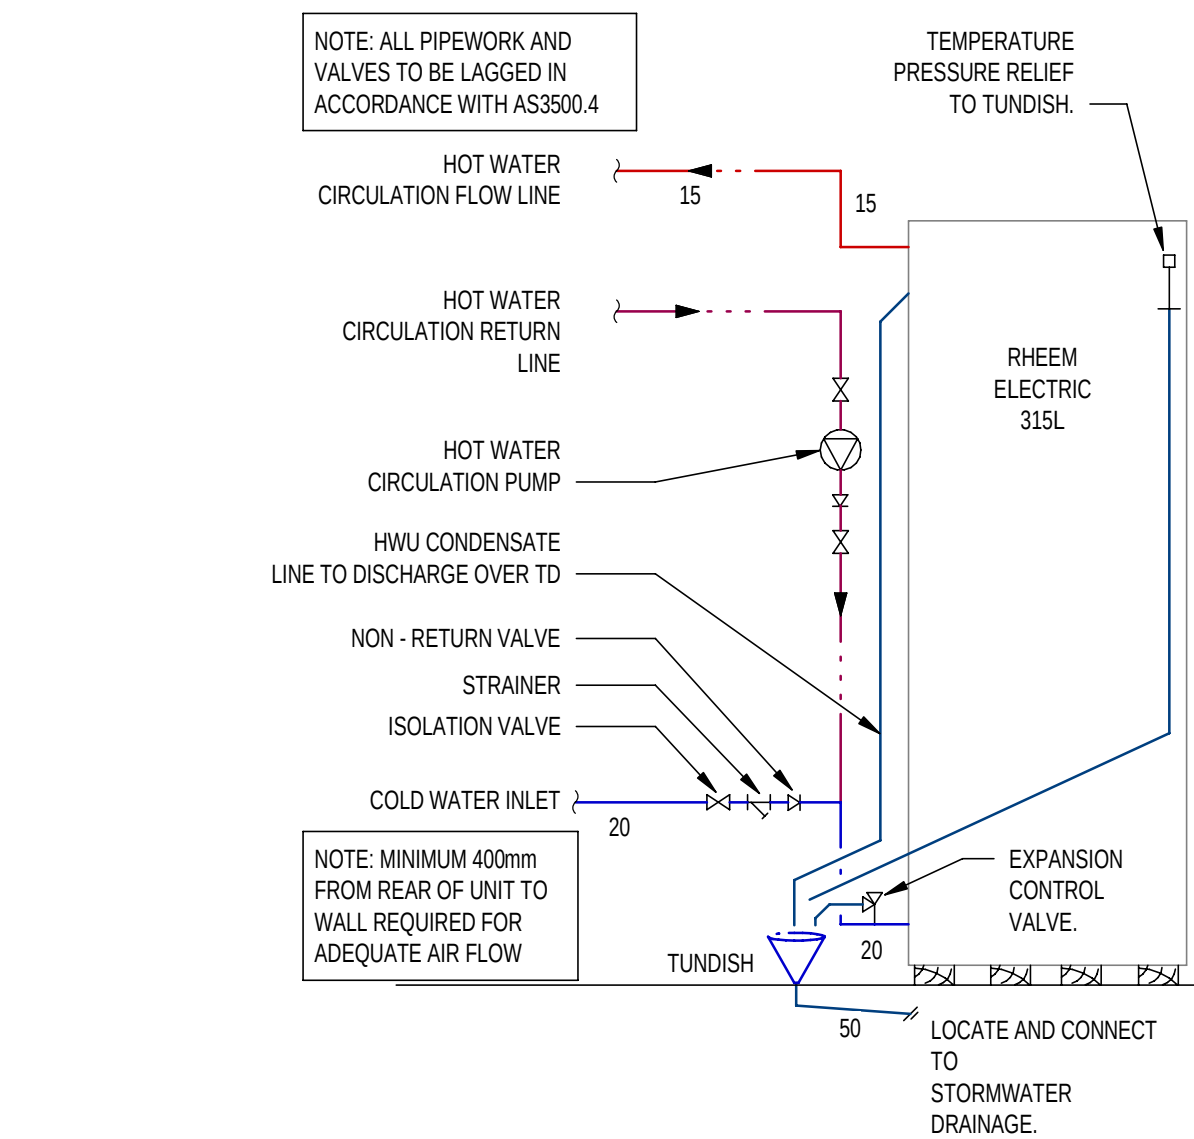

HOT WATER UNIT DETAIL N.T.S.

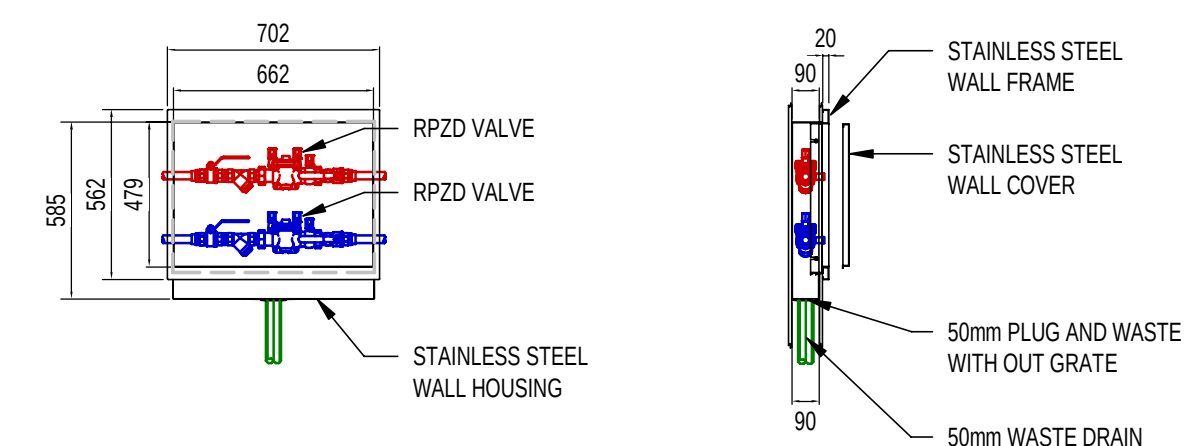

RPZD IN SS WALL BOX DETAIL N.T.S.

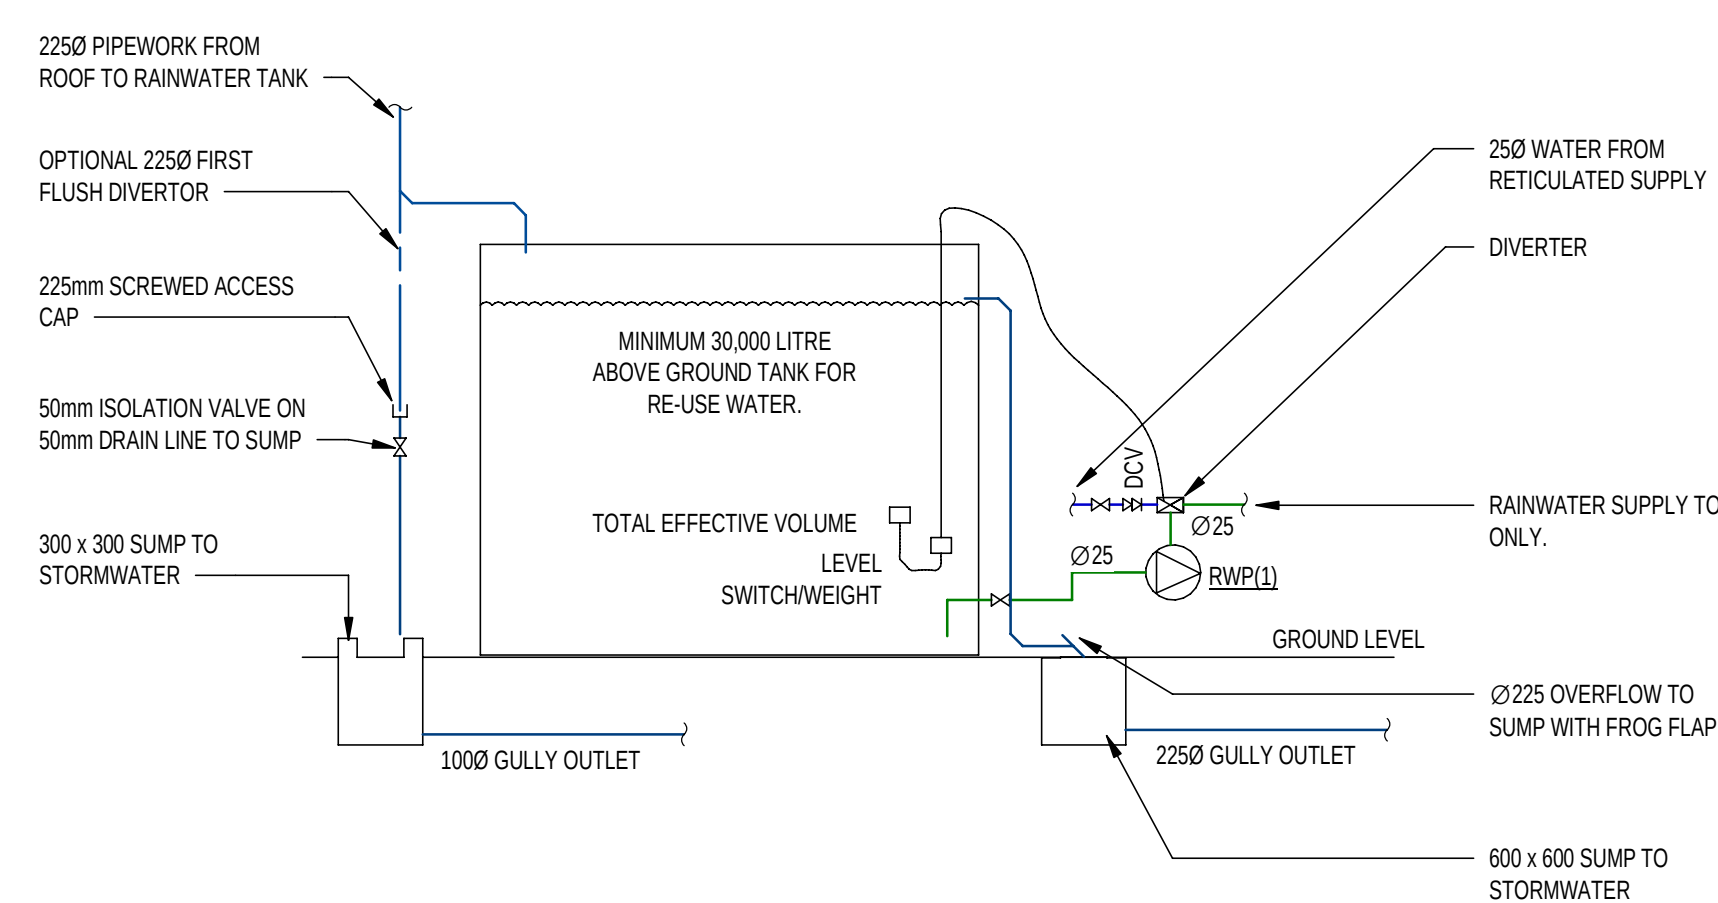

RAINWATER TANK DETAIL - NEW TRADES BUILDING N.T.S.

INFORMATION REFLECTED ON THIS DRAWING REPRESENTS HYDRAULIC SERVICES DESIGN DEVELOPED FOR D&C TENDER ADVISE ONLY, AND SHOULD NOT BE REGARDED AS COMPLETE. THE D&C CONTRACTOR SHOULD REFER TO ALL ASSOCIATED ARCHITECTURAL AND OTHER DISCIPLINE DRAWINGS, PROJECT BRIEFS AND CLIENT REQUIREMENTS AND MAKE ADEQUATE ALLOWANCES FOR ALL NECESSARY HYDRAULIC SERVICES WORKS TO MEET THESE REQUIREMENTS, EQUIPMENT SCHEDULES AND COMPLIANCE WITH THE NCC & APPROPRIATE AUSTRALIAN STANDARDS

--	--	