




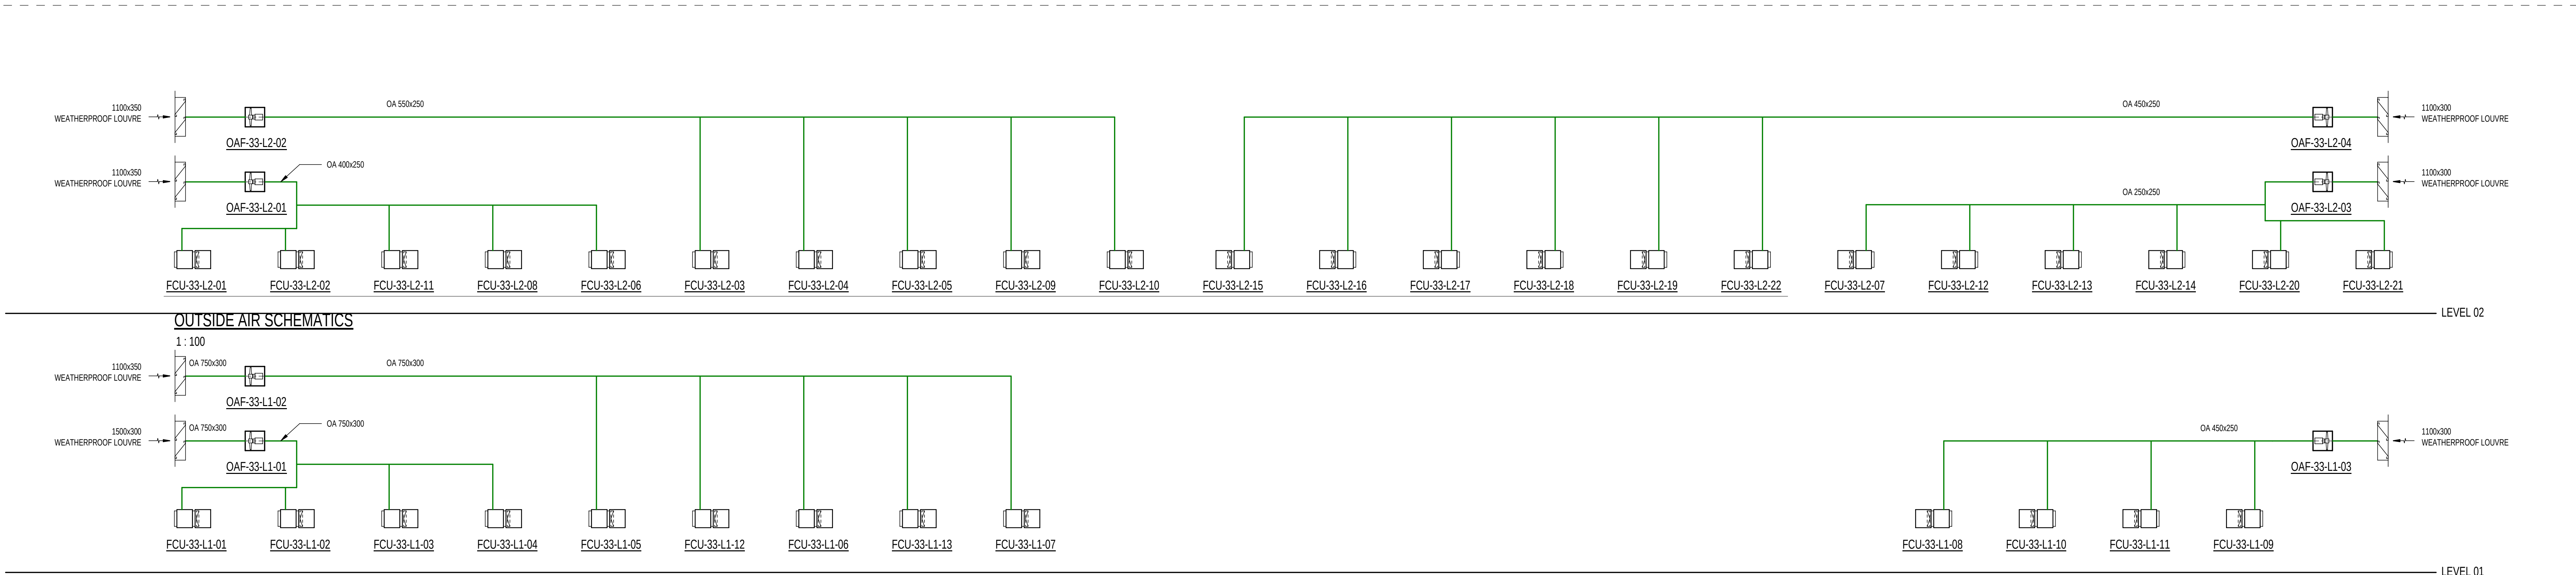

BUILDING 33 OUTSIDE AIR SCHEMATICS

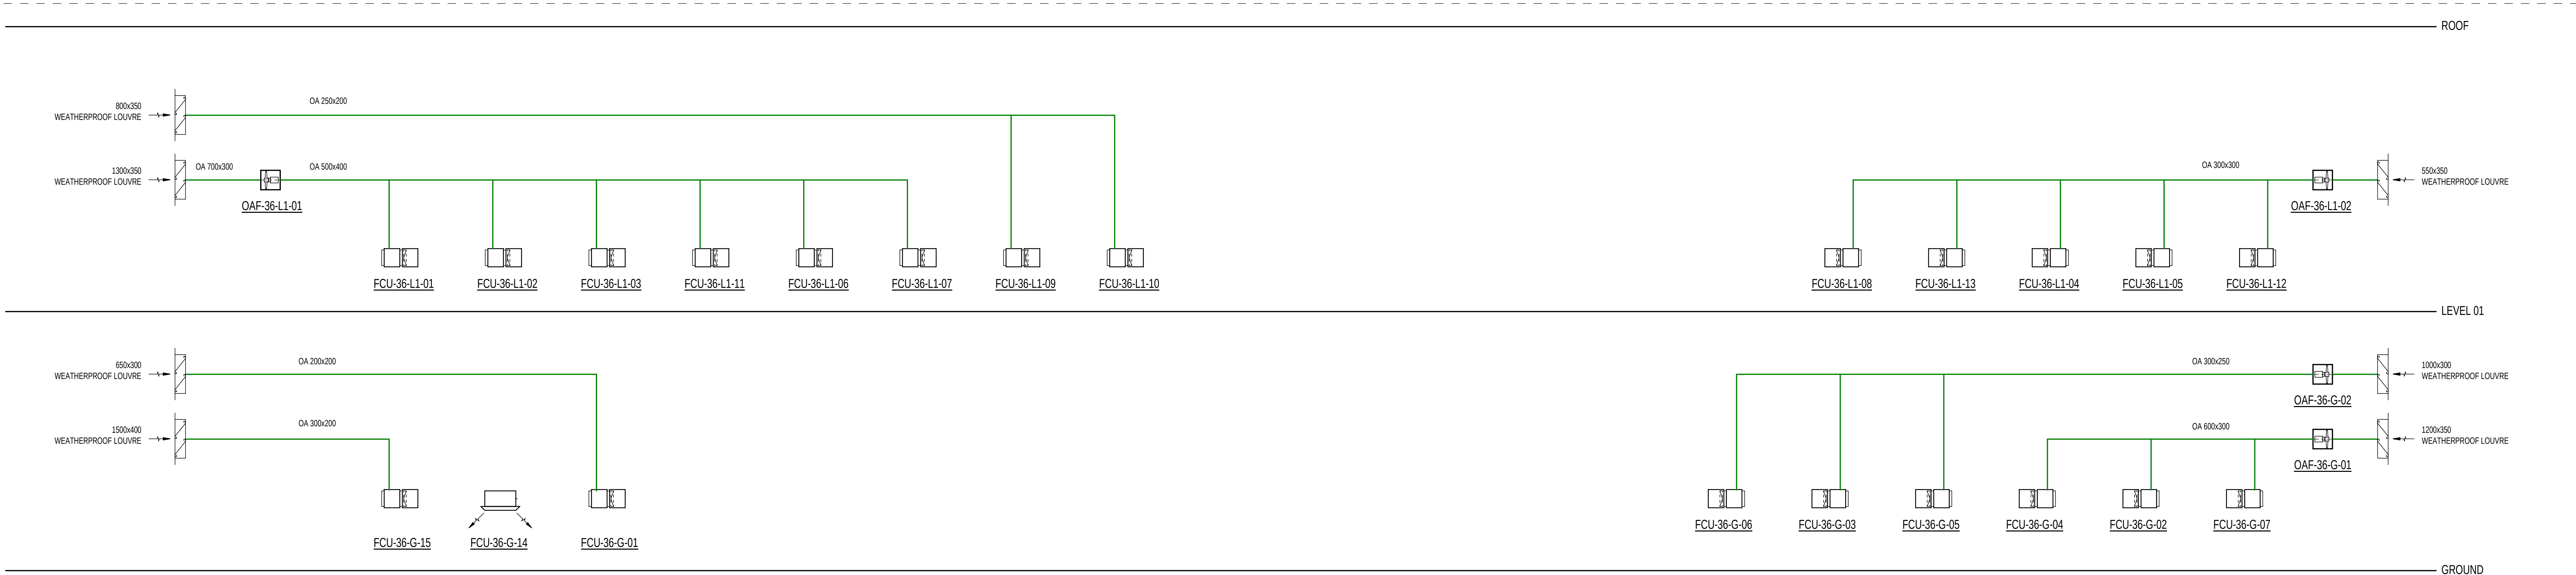

BUILDING 36 OUTSIDE AIR SCHEMATICS

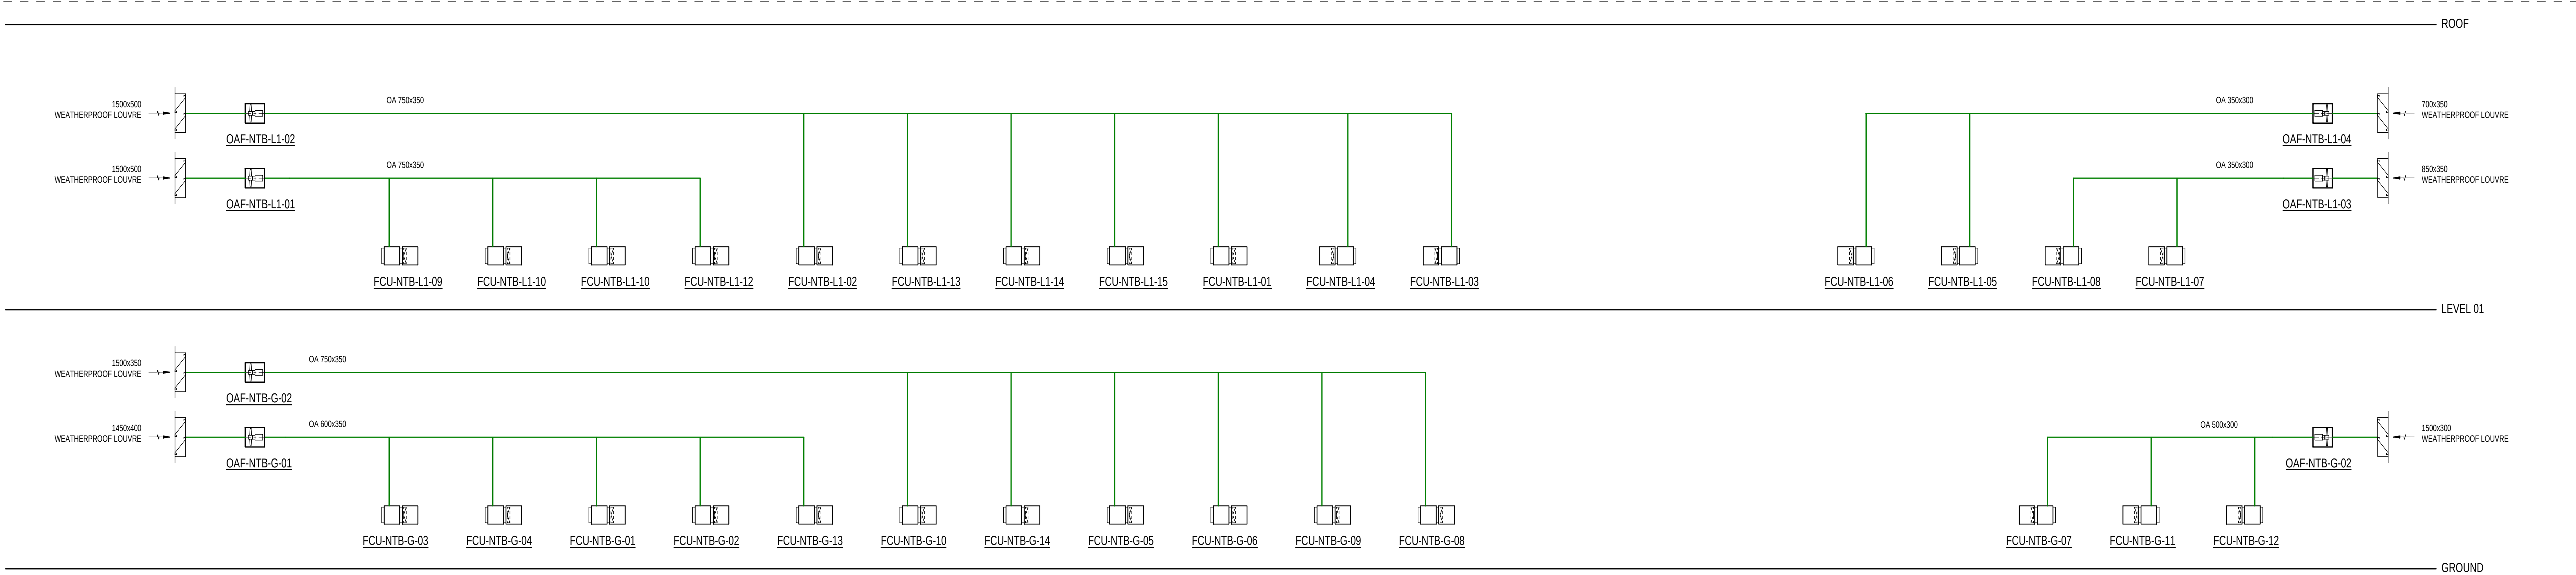

NEW TRADES BUILDING OUTSIDE AIR SCHEMATICS

INFORMATION REFLECTED ON THIS DRAWING REPRESENTS MECHANICAL SERVICES DESIGN DEVELOPED FOR D&C TENDER ADVISE ONLY, AND SHOULD NOT BE REGARDED AS COMPLETE. THE D&C CONTRACTOR SHOULD REFER TO ALL ASSOCIATED ARCHITECTURAL AND OTHER DISCIPLINE DRAWINGS, PROJECT BRIEFS AND CLIENT REQUIREMENTS AND MAKE ADEQUATE ALLOWANCES FOR ALL NECESSARY MECHANICAL SERVICES WORKS TO MEET THESE REQUIREMENTS, EQUIPMENT SCHEDULES AND COMPLIANCE WITH THE NCC & APPROPRIATE AUSTRALIAN STANDARDS

A	12.01.2020	RD	ISSUED FOR D&C TENDER	MB	SM
REV	DATE	BY	DESCRIPTION	CHK	APP

DESIGN DEVELOPMENT



900 Ann Street, Level 12, Fortitude Valley 4006
Tel: +61-7-3854-6200 Fax: +61-7-3854-6500
<http://www.wsp.com>

CLIENT:

CQU

ARCHITECT:

THOMSON ADSETT / PEDDLE THORP

PROJECT:

CQU ROCKHAMPTON TAFE CONSOLIDATION

TITLE:

MECHANICAL SERVICES
MECHANICAL SERVICES - OUTSIDE AIR
SCHEMATICS

SCALE & NO

N.T.S.

CHECKED:

MB

APPROVED:

SM

PROJECT NUMBER:

PS229518

DRAWN:

RD

DATE:

FEB 2026

DRAWING NO:

00-ME-DR-210-A00-00-02

REV

A

© WSP Australia Pty Ltd