


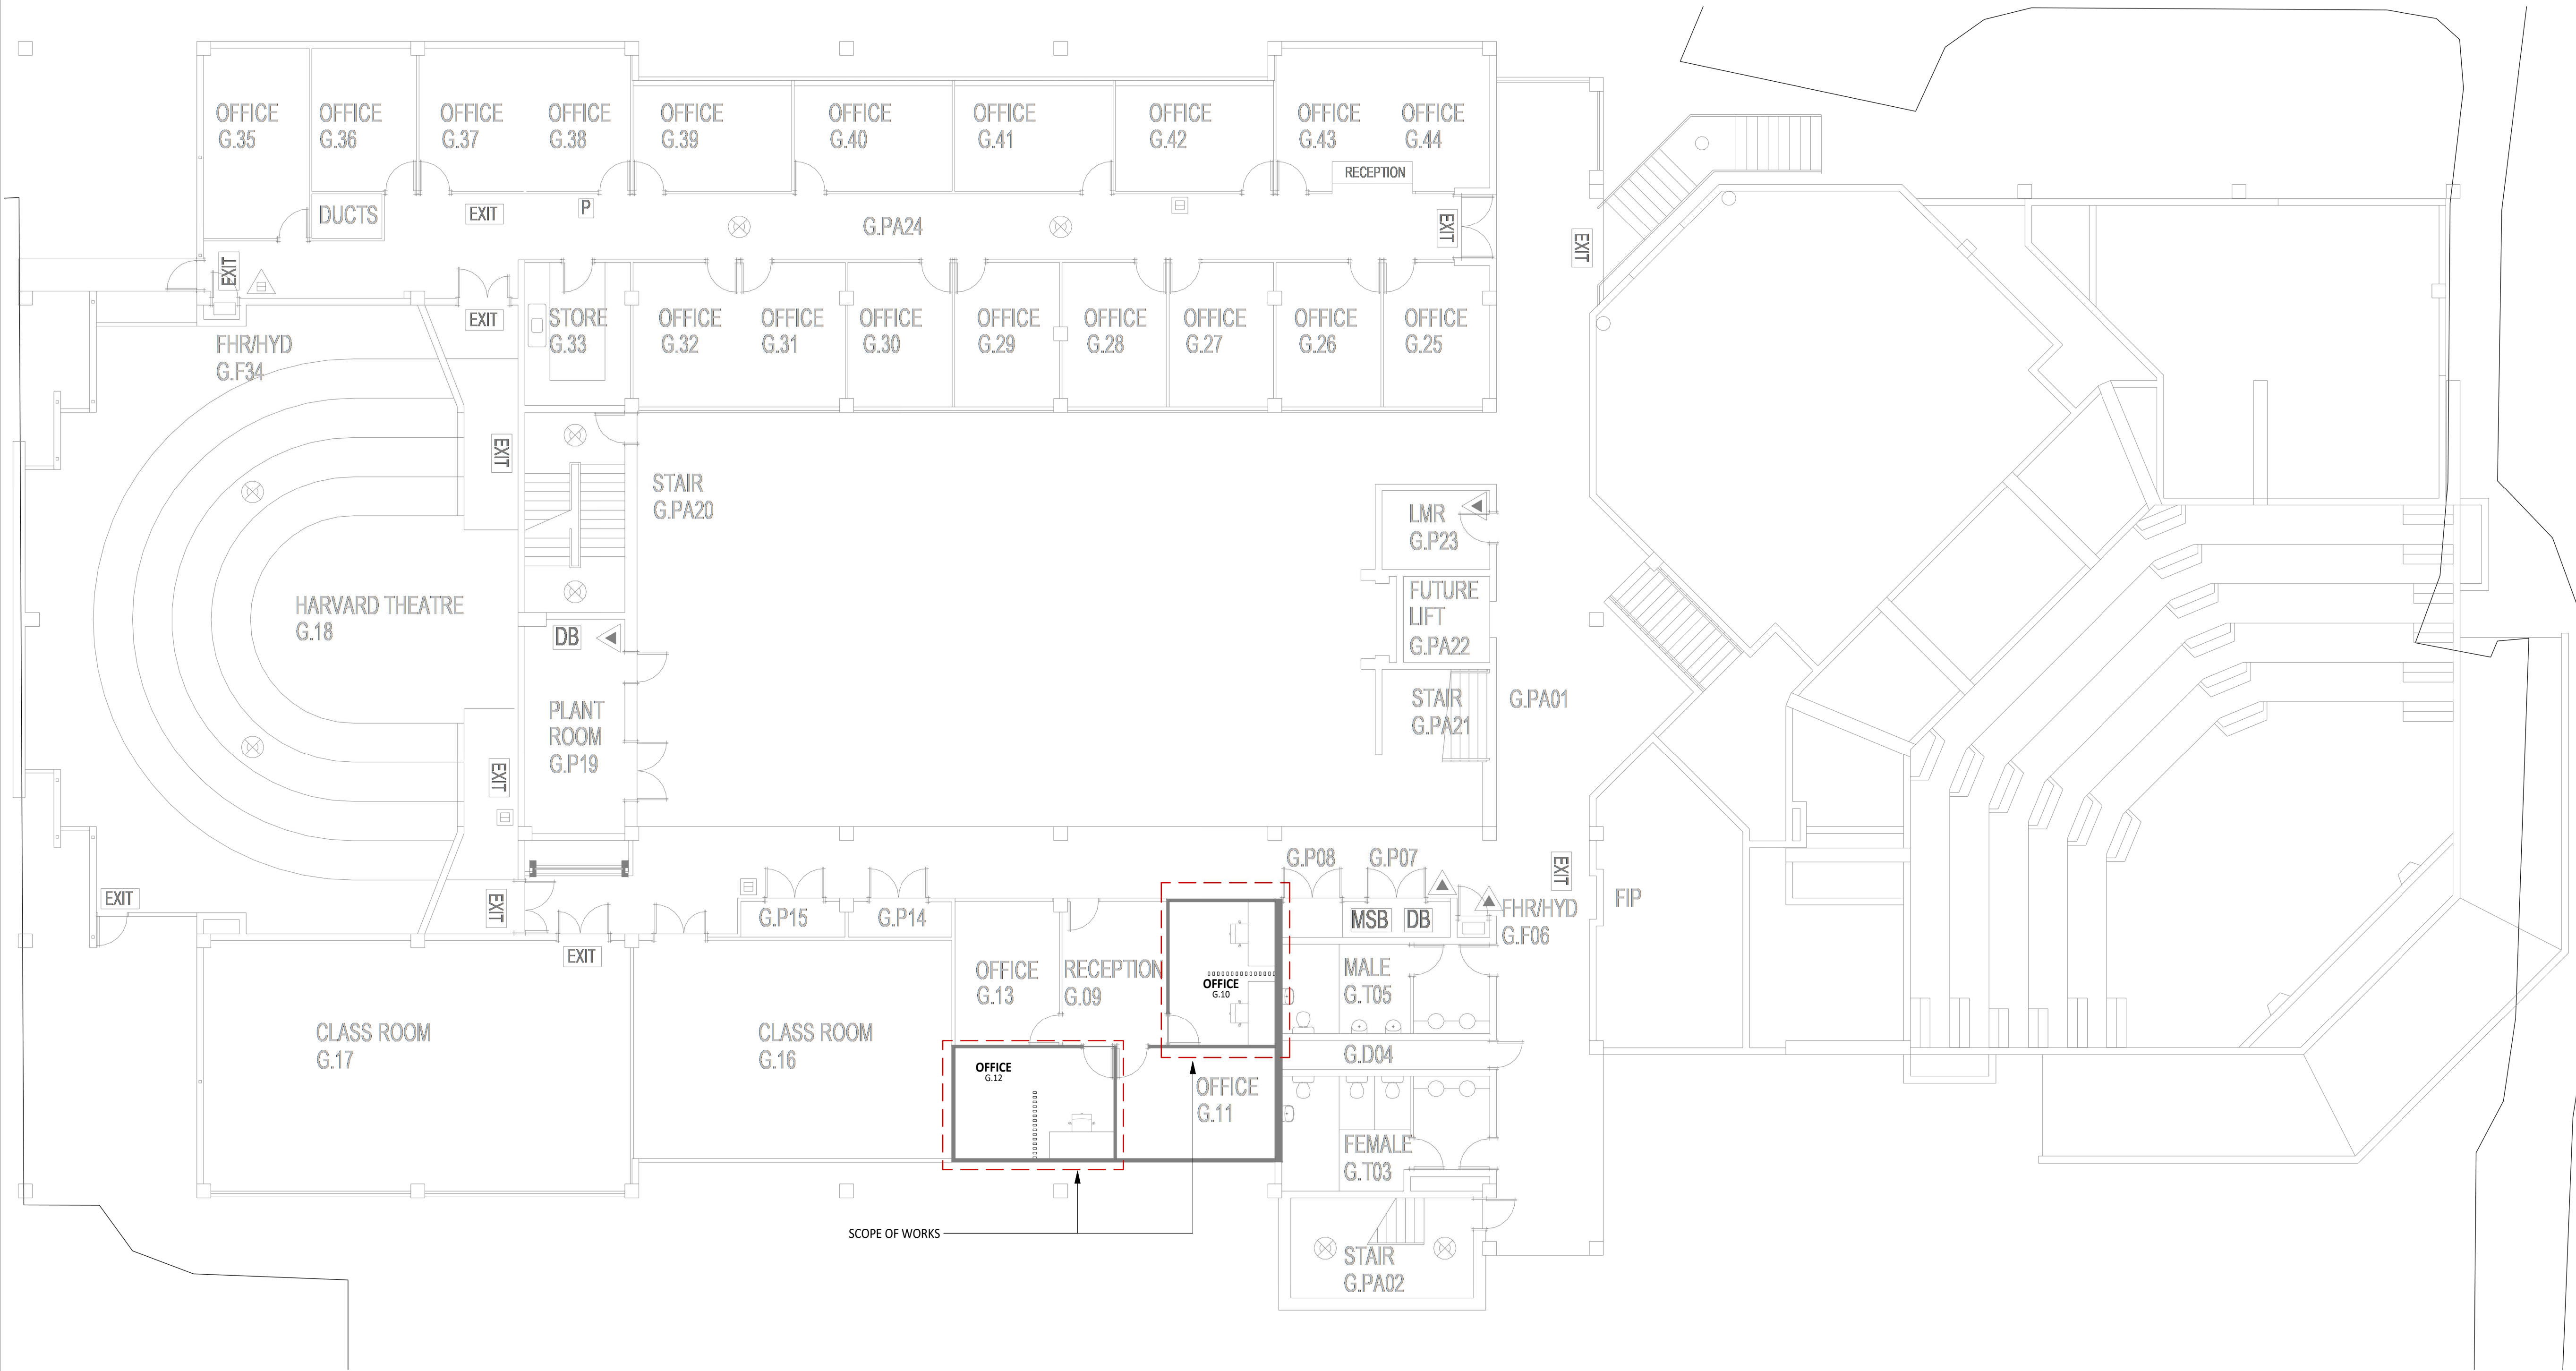

© Copyright
These drawings and designs and the copyright thereof are the property of Thomson Adsett Pty Ltd and must not be used, retained or copied without written permission of Thomson Adsett Pty Ltd. A.B.N 76 105 314 654 Trading as ThomsonAdsett. Dimensions take precedence over scaling. Do not measure off drawings as print sizes may vary

CQU ROCKHAMPTON
TAFE
CONSOLIDATION -
STAGE 2
ROCKHAMPTON, QUEENSLAND




A	12/02/26	ISSUED FOR TENDER	SM
3	30/01/26	60% DRAFT ISSUE	SM
2	23/01/26	FOR COORDINATION ISSUE	JT
1	25/11/25	50% COSTING ISSUE	BS

rev	date	details	init.
-----	------	---------	-------

drawn	date
TA/PT	11/25/25
checked	date
JT	11/25/25
verified	date
BS	11/25/25

scale

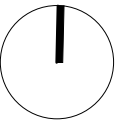

BLDG 32 - GROUND FLOOR

scale	project no.
1 : 100 @ A1	260018
revision	
A	
sheet no.	
CQU-ROK-032-GN-ARC-03-02	

ISSUE FOR TENDER