


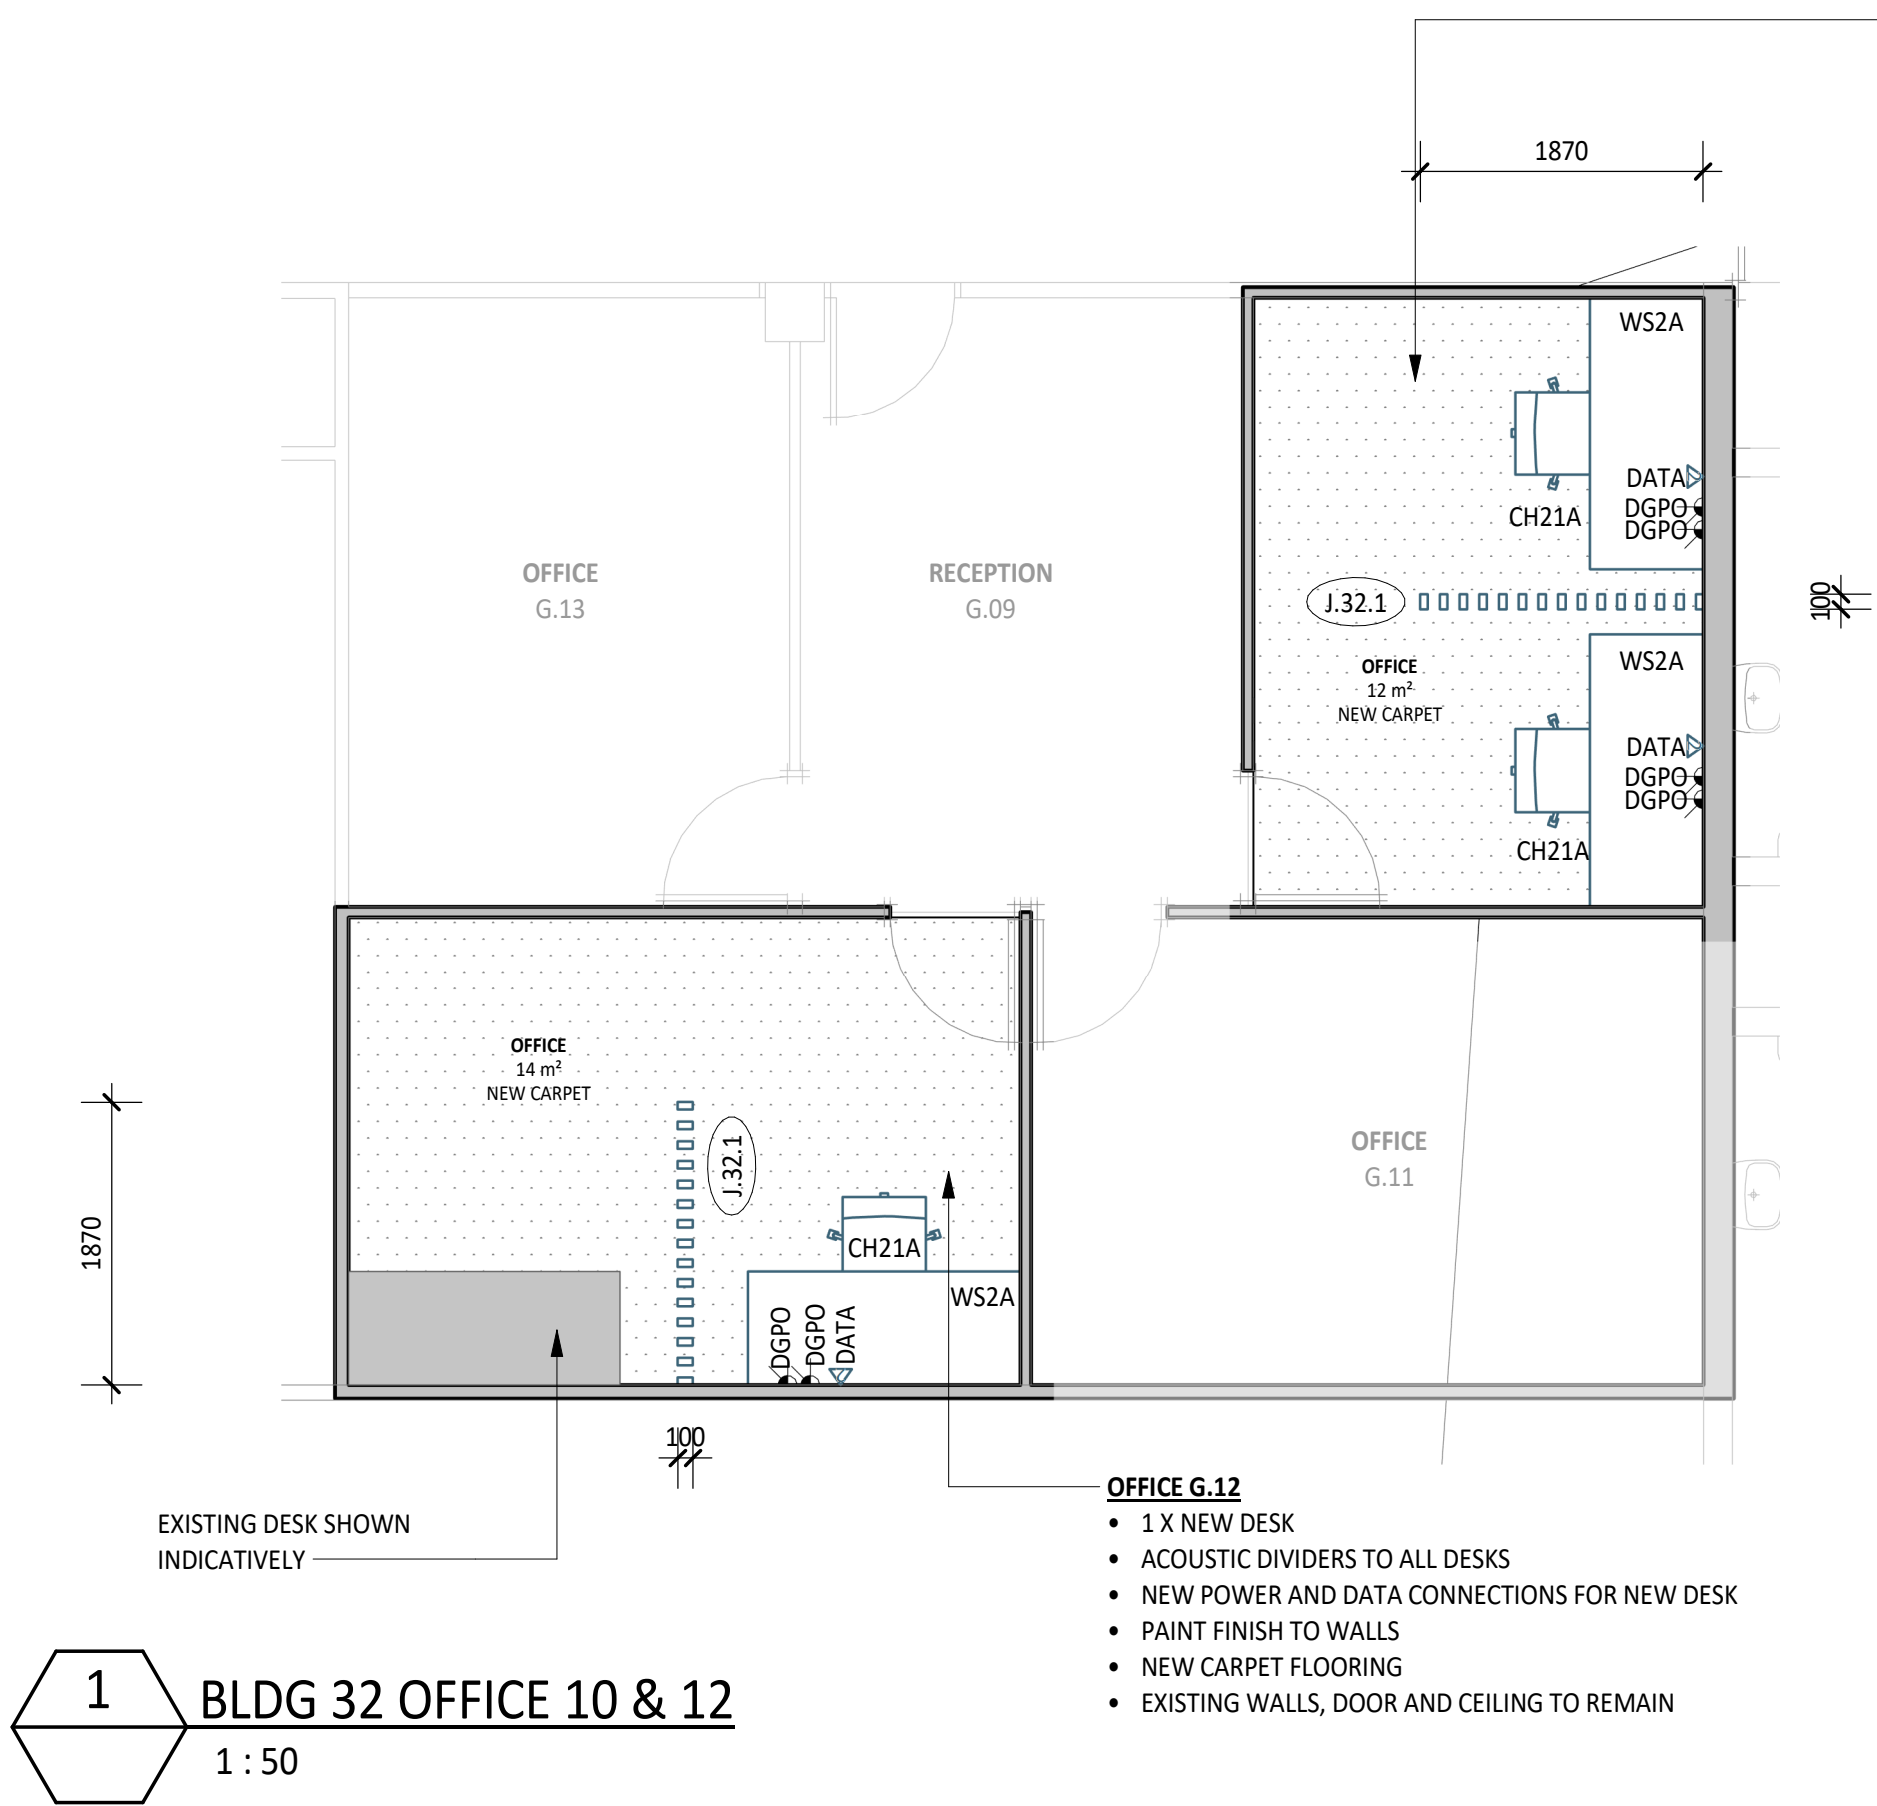

- OFFICE G.10**
- 2 X NEW DESKS
 - ACOUSTIC DIVIDERS TO ALL DESKS
 - NEW POWER AND DATA CONNECTIONS FOR NEW DESKS
 - PAINT FINISH TO WALLS
 - NEW CARPET FLOORING
 - NEW LIGHTS
 - EXISTING WALLS, DOOR AND CEILING TO REMAIN

40-LEGEND FFE - OFFICE B32 G.10			
Code	Description	Group	Count
CH21A	Chair - Task	1	2
WS2A	Workstation: Office 1800mm (W) x 750mm(D) – Sit/Stand	1	2

60-LEGEND JOINERY - BUILDING 32 - OFFICE G10	
FFE_Mark	Comments

J.32.1	Full Height Timber Battens
--------	----------------------------

40-LEGEND FFE - OFFICE B32 G.12			
Code	Description	Group	Count
CH21A	Chair - Task	1	1
WS2A	Workstation: Office 1800mm (W) x 750mm(D) – Sit/Stand	1	1

60-LEGEND JOINERY - BUILDING 32 - OFFICE G12	
FFE_Mark	Comments

J.32.1	Full Height Timber Battens
--------	----------------------------

- OFFICE G.12**
- 1 X NEW DESK
 - ACOUSTIC DIVIDERS TO ALL DESKS
 - NEW POWER AND DATA CONNECTIONS FOR NEW DESK
 - PAINT FINISH TO WALLS
 - NEW CARPET FLOORING
 - EXISTING WALLS, DOOR AND CEILING TO REMAIN

GROUP 1 ITEMS
(PROVIDED & FITTED UNDER CONTRACT)

GROUP 2 ITEMS
(PROVIDED BY CLIENT & FITTED UNDER CONTRACT)

GROUP 2T ITEMS - EXISTING EQUIPMENT
(PROVIDED BY CLIENT & FITTED UNDER CONTRACT)

GROUP 3 ITEMS
(PROVIDED & INSTALLED BY CLIENT)

PLANS TO BE PRINTED IN COLOUR

SCH_CodeFF&E TAG

JO.PROCJOINERY TAG

- RLS NOTES**

 1. ALL ARCHITECTURAL DRAWINGS TO BE READ IN CONJUNCTION WITH OTHER DISCIPLINES.
 2. REFER TO FF&E, SANITARYWARE SCHEDULES FOR ALL FURNITURE, FIXTURES, AND EQUIPMENT.
 3. REFER TO HYDRAULIC ENGINEER'S DRAWINGS FOR HYDRAULIC SERVICES. FINISH OF VALVE/BOX COVERS TO MATCH ADJACENT WALL/JOINERY FINISH.
 4. REFER TO ELECTRICAL DOCUMENTATION FOR OUTLET DETAILS (ie. POWER, DATA, COMMS etc.)
 5. REFER TO AUDIO VISUAL DOCUMENTATION (VideoPro) FOR AV REQUIREMENTS AND DETAILS.
 6. AV SUPPLIER TO CONFIRM EXACT POSITIONS OF EQUIPMENT ON SITE.
 7. ALL FF&E ITEMS ARE TO BE READ IN CONJUNCTION WITH FF&E SCHEDULES AND CQU DESIGN MANUAL.
 8. ALL FF&E AND TRANSFER ITEMS TO BE REVIEWED AND CONFIRMED WITH CLIENT PRIOR TO COMMENCING ON SITE.
 9. PROVIDE ALLOWANCE AND ADD SUPPORT TO WALLS, WHERE FITTINGS ARE WALL MOUNTED. THIS INCLUDES BUT NOT LIMITED TO HANDBASINS, HANDRAILS, SCREENS, PROJECTORS, etc.
 10. FF&E COUNT IS FOR INFORMATION ONLY. THE TOTAL NUMBER OF FF&E ITEMS ARE TO BE CONFIRMED WITH CLIENT AND ARCHITECTS BEFORE PURCHASE OF ITEMS.
 11. CONFIRM ALL DIMENSIONS ON SITE FOR JOINERY ITEMS.
 12. ALL SANITARY FIXINGS & FIXTURES IN PWD TOILETS TO BE INSTALLED IN ACCORDANCE WITH AS1428.1
 13. ALLOW FOR FIRE EXTINGUISHERS & FIRE BLANKETS AS PER AS2444.2001.
 14. POWER AND DATA POINTS SHOWN ON THE ROOM LAYOUT SHEETS WERE SHOWN AND DISCUSSED DURING USER GROUP BRIEFING. THESE RELATE TO PARTICULAR EQUIPMENT THAT WAS DISCUSSED AS REQUIRING POWER AND DATA. THESE REFLECT STAKEHOLDER EXPECTATIONS FOR SPECIFIC POWER AND DATA POINTS AND HAVE REMAINED IN THE DOCUMENTATION AS A USEFUL REFERENCE FOR THE CONTRACTOR. THESE ARE NOT A COMPLETE QUANTITY AND SPECIFICATION OF POWER AND DATA. THE CONTRACTOR IS TO REFER TO ELECTRICAL ENGINEER'S DOCUMENTATION FOR ALLOWANCE. REFER TO ELECTRICAL DOCUMENTATION FOR AMPS AND 3 PHASE POWER REQUIREMENTS. REFER TO AUDIO VISUAL (VIDEOPRO) DOCUMENTATION FOR ADDITIONAL POWER AND DATA REQUIREMENTS
 15. ALLOW FOR STRUCTURAL PLY BACKING BEHIND PLASTERBOARD FOR FULL EXTENT OF WALLS WITH MOUNTED AUDIO VISUAL EQUIPMENT. REFER TO AUDIO VISUAL (VIDEOPRO) DOCUMENTATION FOR LOCATIONS OF WALL MOUNTED EQUIPMENT.
 16. ALLOW FOR PRIVACY FILM TO ALL INTERNAL GLAZING (DOORS AND WINDOWS) TO OFFICES AND MEETING ROOMS. CONFIRM SET OUT PRIOR TO INSTALLATION
 17. ALLOW FOR DOUBLE BLOCK OUT BLINDS TO ALL WINDOWS UNLESS NOTED OTHERWISE
 18. ALL INTERNAL DOORS ARE TO BE SOLID CORE DOORS WITHIN ALUMINIUM FRAMED SUITES UNLESS NOTED OTHERWISE.
 19. FLOOR BOXES MUST BE COORDINATED WITH BOTH THE STRUCTURAL AND ELECTRICAL ENGINEERS. BEFORE ANY CUTTING OF THE EXISTING SLAB OCCURS, CONFIRM THE EXACT LOCATIONS AND REQUIREMENTS WITH THE STRUCTURAL ENGINEER.
 20. HEARING AUGMENTATION TO AUSTRALIAN STANDARDS – REFER VIDEOPRO AND ELECTRICAL SPECIFICATION

ELECTRICAL LEGEND			
	SINGLE POWER OUTLET		LIGHT SWITCH
	DOUBLE POWER OUTLET		TV
	SINGLE DATA		
	DOUBLE DATA		
	REFER TO ELECTRICAL ENGINEER'S DRAWINGS FOR DETAILS		

thomson
adsett

PEDDLE THORP
architecture | interiors | health | planning

Telephone +61 7 3840 9999
bne@thomsonadsett.com
Level 9, 470 St Pauls Terrace
Fortitude Valley
Qld 4006 Australia
thomsonadsett.com

© Copyright
These drawings and designs and the copyright thereof are the property of Thomson Adsett Pty Ltd and must not be used, retained or copied without written permission of Thomson Adsett Pty Ltd. ABN 76 105 314 654 Trading as ThomsonAdsett. Dimensions take precedence over scaling. Do not measure off drawings as print sizes may vary

1

BLDG 32 OFFICE 10 & 12

1 : 50

ISSUE FOR TENDER

RLS - BLD32-GL - OFFICES



A	12/02/26	ISSUED FOR TENDER	SM
2	30/01/26	60% DRAFT ISSUE	SM
1	23/01/26	FOR COORDINATION ISSUE	JT

rev	date	details	init.
drawn	date		
TA/PT	12/02/26		
checked	date		
JT	12/02/26		
verified	date		
JT	12/02/26		

scale

scale

1 : 50 @ A1

project no.

260018

revision

A

sheet no.

CQU-ROK-032-GN-ARC-60-10