
DO NOT SCALE

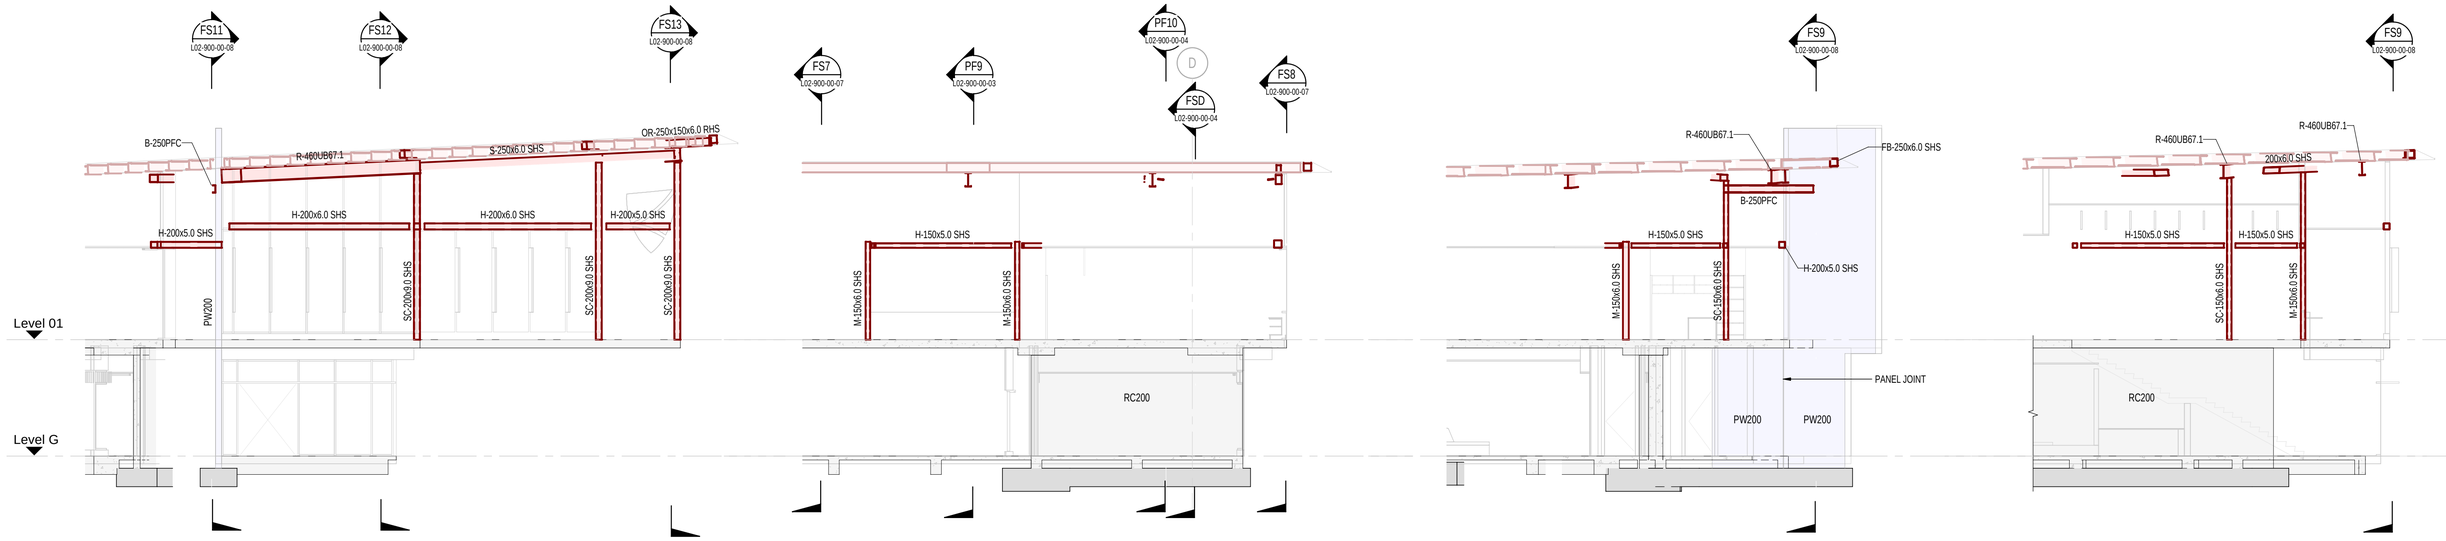


SECTION FS9 — SCALE 1 : 100 — L02-510-00-02

SECTION FS10 — SCALE 1 : 100 — L02-510-00-02

SECTION FS11 — SCALE 1 : 100 — L02-510-00-02

SECTION FS12 — SCALE 1 : 100 — L02-510-00-02

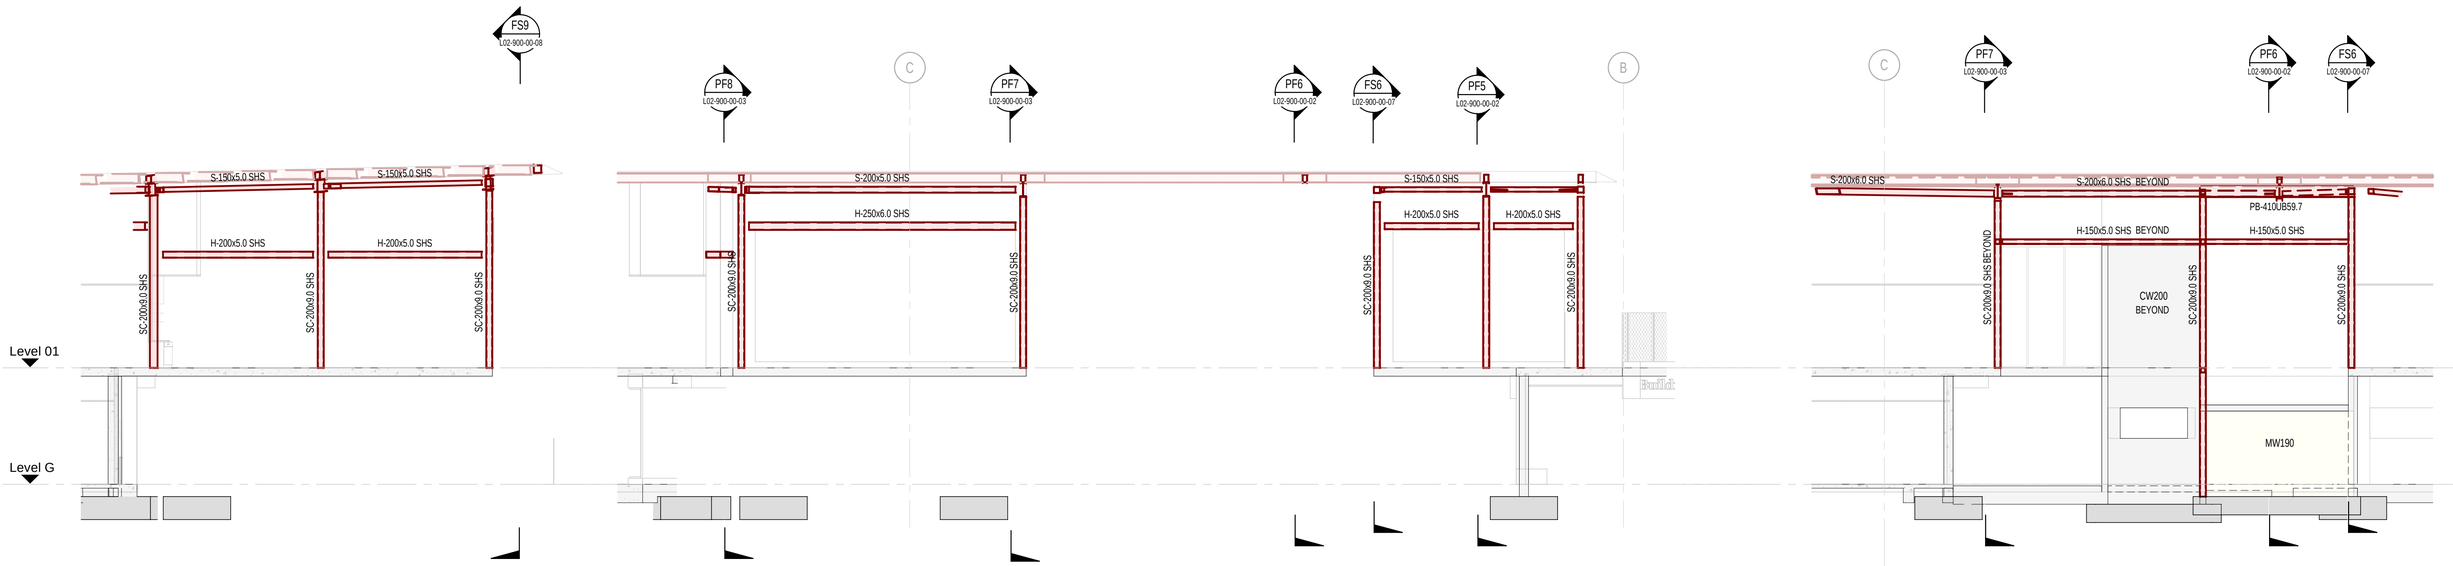

SECTION FS13 — SCALE 1 : 100 — L02-510-00-02

SECTION FS14 — SCALE 1 : 100 — L02-510-00-01

SECTION FS15 — SCALE 1 : 100 — L02-510-00-01

INFORMATION REFLECTED ON THIS DRAWING REPRESENTS STRUCTURAL DESIGN DEVELOPED FOR D&C TENDER ADVICE ONLY, AND SHOULD NOT BE REGARDED AS COMPLETE. THE D&C CONTRACTOR SHOULD REFER TO ALL ASSOCIATED ARCHITECTURAL AND OTHER DISCIPLINE DRAWINGS, PROJECT BRIEFS AND CLIENT REQUIREMENTS AND MAKE ADEQUATE ALLOWANCES FOR ALL NECESSARY STRUCTURAL WORKS TO MEET THESE REQUIREMENTS, EQUIPMENT SCHEDULES AND COMPLIANCE WITH THE NCC & APPROPRIATE AUSTRALIAN STANDARDS

DRAWING CREATED IN REVIT.

REV	DATE	BY	DESCRIPTION	CHK	APP
A	12.02.2026	MSB	ISSUED FOR D&C TENDER	BM	DG
P1	30.01.2026	PJH	DRAFT 60% DD ISSUE FOR REVIEW	BM	DG

DRAWING STATUS: DESIGN DEVELOPMENT

wsp

http://www.wsp.com

CLIENT: CQUniversity AUSTRALIA

ARCHITECT: THOMSON ADSETT + PEDDLE THORP

PROJECT: CQU ROCKHAMPTON TAFE CONSOLIDATION - STAGE 2

TITLE: BuildingName LEVEL 02 - FRAMING SECTIONS - SHEET 08

SCALE @ A1:	CHECKED:	APPROVED:
1:100	BM	DG
PROJECT NUMBER:	DRAWN:	DATE:
PS229518	PJH	14.01.2016

DRAWING No: 92-ST-DR-L02-900-00-08 REV: A

© WSP Australia Pty Ltd